

▲ LISTE PLAN & I-A & I-B  
S-20 FOUNDATION PLAN, DETAILS  
S-30 ROOF & ROOF ELEVATIONS  
F-4 ROOF PLAN BASEMENT PLAN  
F-5 GROUND FLOOR PLAN

FLOOR PLAN  
E-WEST & SOUTH ELEVATIONS  
E-S " & NORTH "

E-W-EAST ELEVATIONS  
I-O SECTIONS & DETAILS  
I-T " " "

I-V " " "  
I-X " " "  
I-L " " "

I-5 GROUND FLOOR REFLECTED PLAN  
I-6 BASEMENT & LOFTS " "

P-I POWER PLAN  
P-I-8 " PLANS


S-M FOUNDATION & FRAMING PLANS  
F-20 FLOOR & LOFT PLANS  
F-21 REFLECTED & ROOF CEILING PLANS  
B-22 ELEVATIONS  
B-23 SECTIONS & DETAILS

R-1  
R-2  
R-3  
R-4

**LOT 3**

## "GREEN"

- 1. CHECK LIST OF CONSTRUCTION TECHNIQUES & ADDITIONS TO THE CONSIDERED FOR THE IMPLEMENTATION INFO PROVIDED.
- 2. LITTLE & GRAVEL SPACE WITHIN INSULATED ENVELOPE.
- 3. FROST INSULATION.
- 4. REMOVABLE MATERIALS.
- 5. SOLAR ELECTRICAL PANELS.
- 6. EXISTING & FROST WATER RUNOFF.
- 7. INSTANT HOT WATER.
- 8. TIRED LIGHTING.
- 9. SWIMMING SOLAR HEAT GAIN.
- 10. STEADY HVAC SYSTEM.
- 11. HIGH THERMAL LAMP.
- 12. HIGH VELOCITY FLOW SYSTEM.
- 13. NO DIRECT FROST/HEAT EXCHANGE.

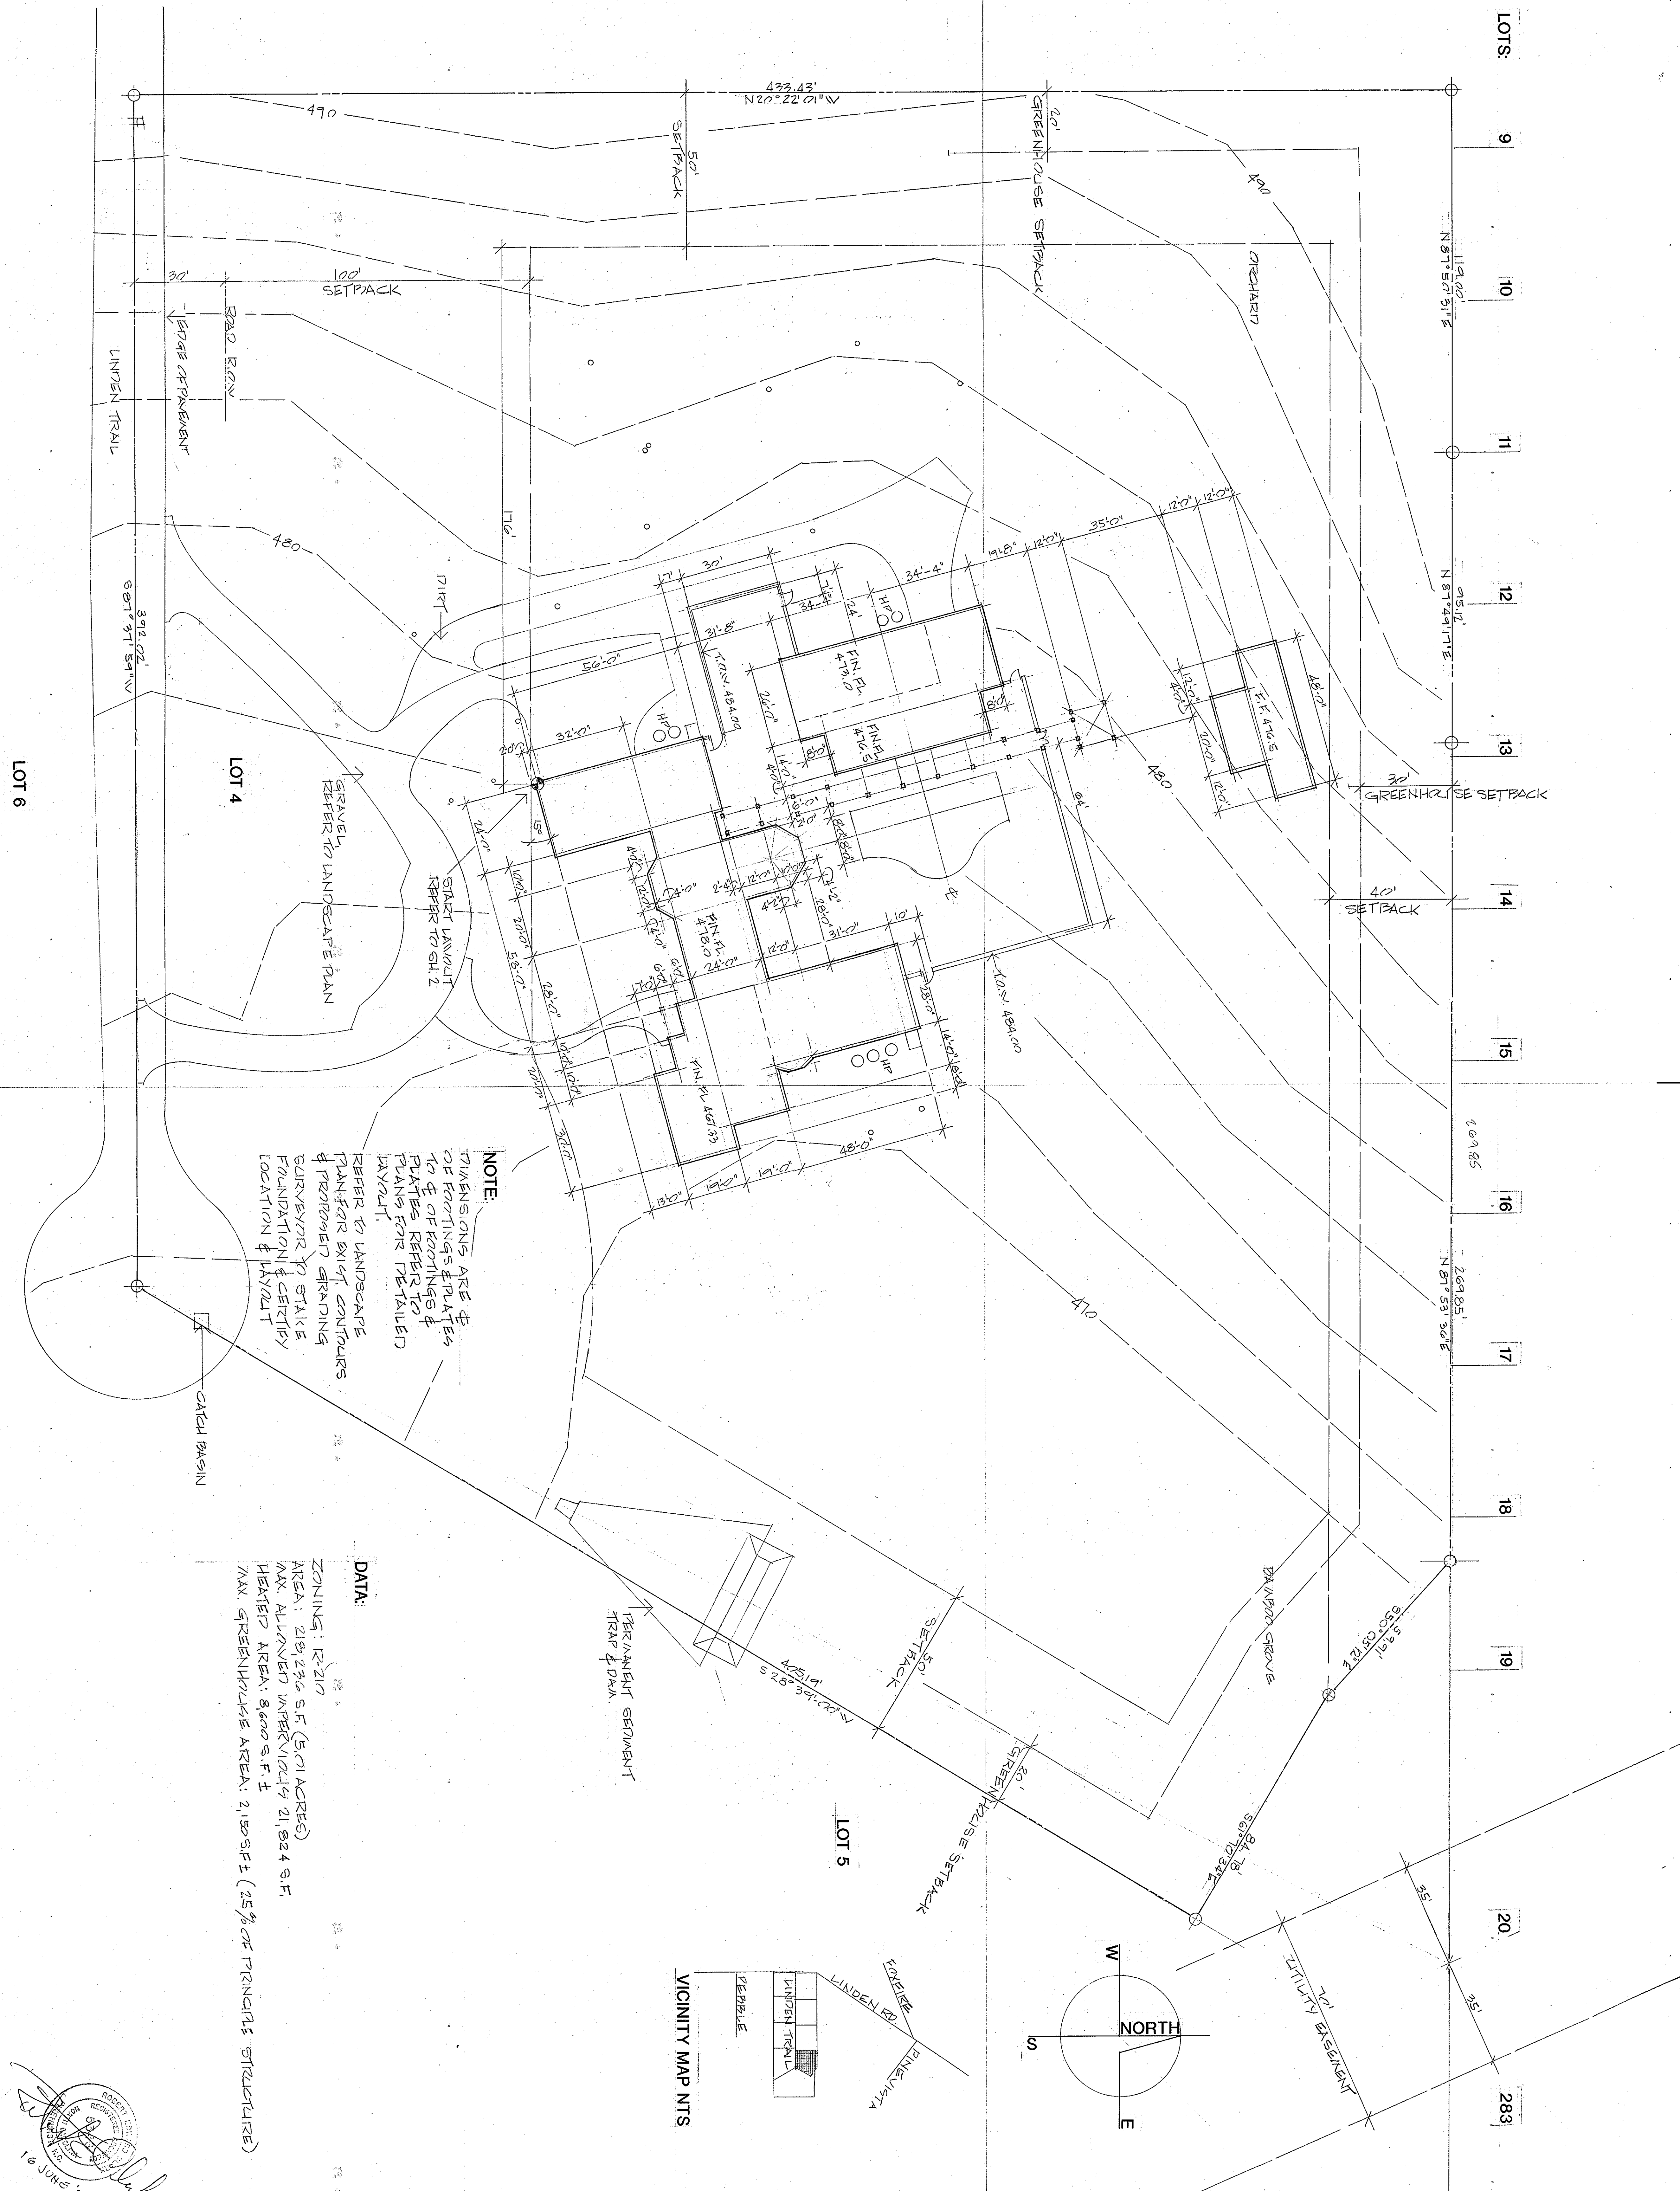

**SITE PLAN 1"=20'**

EPSTEIN/LATHAM RESIDENCE LOT 4 LINDEN TRAIL PINEHURST, NC

 7-11-08  
 (APPROVED & ACCEPTED      DATE

## REVISIONS

THE ARCHITECT RETAINS THE RIGHT OF AUTHORSHIP FOR IDEAS EXPRESSED AS HIS WORK, AND AS SUCH ALL DRAWINGS AND SPECIFICATIONS REMAIN THE PROPERTY OF THE ARCHITECT WHETHER THE PROJECT FOR WHICH THEY ARE INTENDED IS EXECUTED OR NOT AND MAY NOT BE USED ON OTHER PROJECTS OR EXTENSIONS OF THIS PROJECT EXCEPT BY AGREEMENT WITH THE ARCHITECT.

ROBERT E. CLARK AIA ARCHITECT


**910 295 4683**

FAX **910 295 5684**

P O BOX 205

65 COMMUNITY ROAD  
PINEHURST NORTH CAROLINA 28370



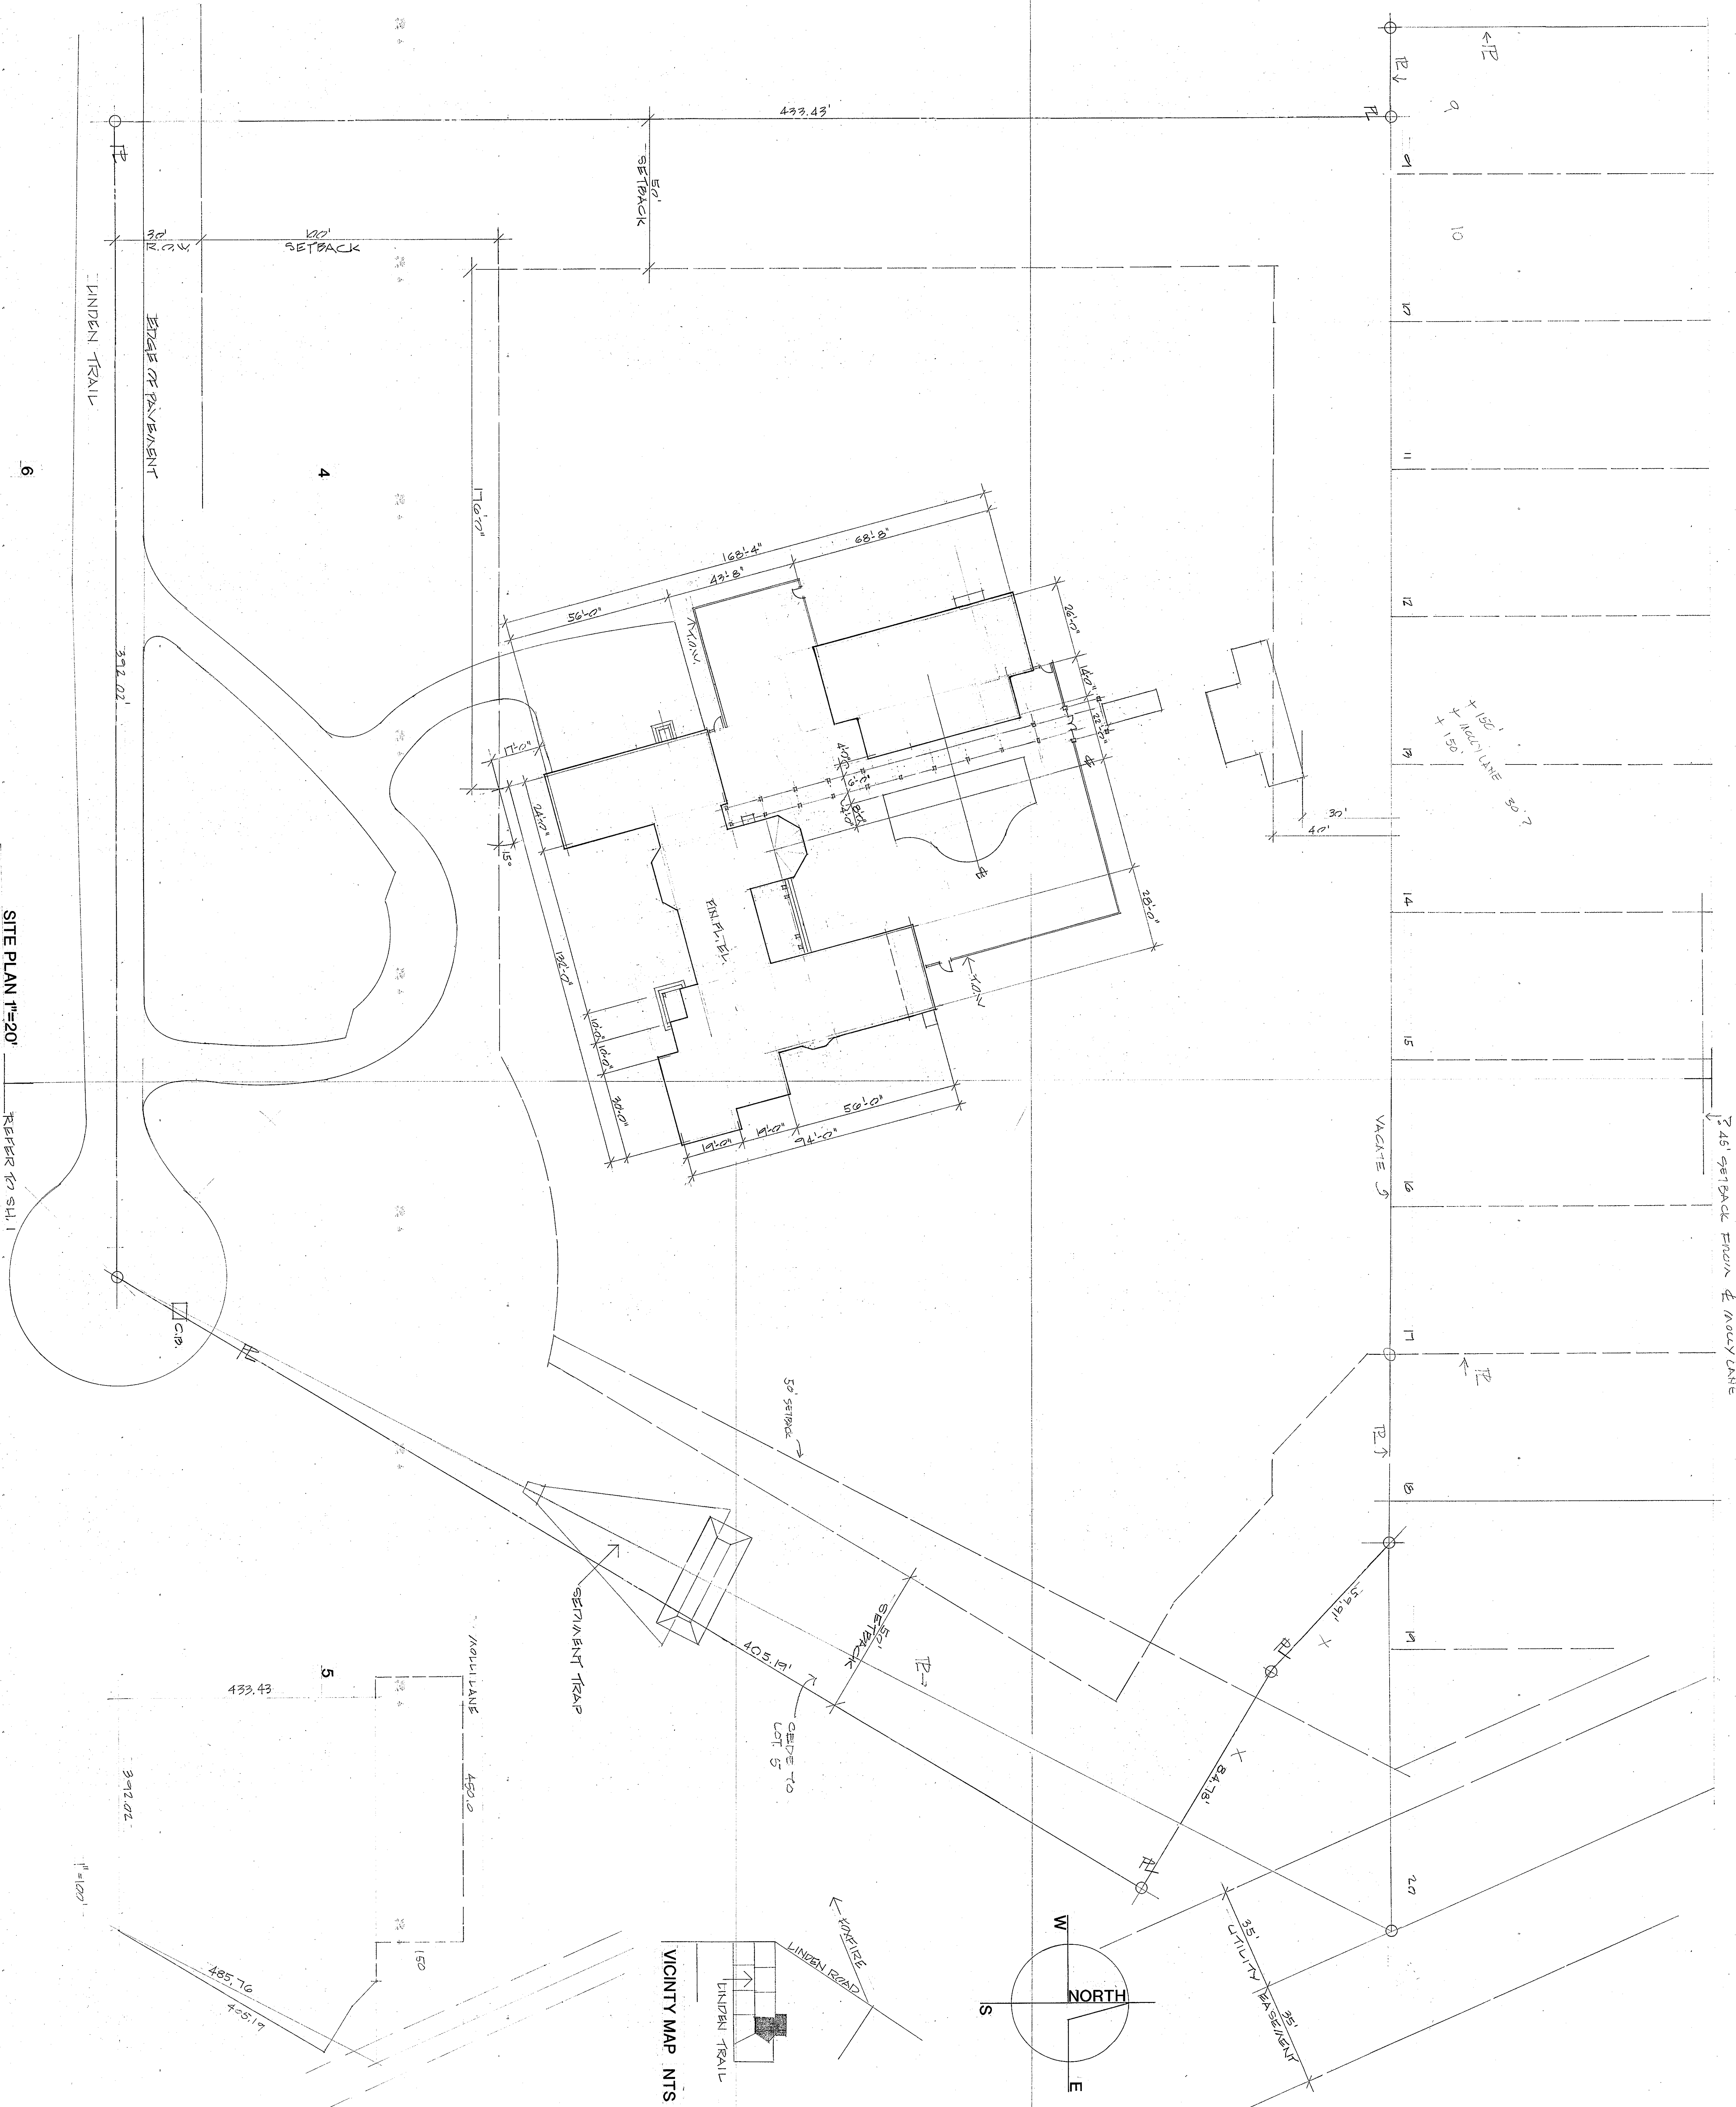



12 MAR 07 REC  
28 JAN 04 REC  
15 DEC 02 REC  
6 NOV 02 REC


EPSTEIN/LATHAM RESIDENCE LOT 4 LINDEN TRAIL, PINEHURST, NC

APPROVED & ACCEPTED  
DATE

REVISIONS

THE ARCHITECT RETAINS THE RIGHT OF AUTHORSHIP FOR  
IDEAS EXPRESSED AS HIS WORK AND AS SUCH ALL  
DRAWINGS AND SPECIFICATIONS REMAIN THE PROPERTY  
OF THE ARCHITECT WHETHER THE PROJECT FOR WHICH  
THEY ARE INTENDED IS EXECUTED OR NOT AND MAY NOT  
BE USED ON OTHER PROJECTS OR EXTENSIONS OF THIS  
PROJECT EXCEPT BY AGREEMENT WITH THE ARCHITECT.

ROBERT E. CLARK AIA ARCHITECT  
910 295 4683  
FAX 910 295 5684  
P O BOX 205  
PINEHURST NORTH CAROLINA 28370

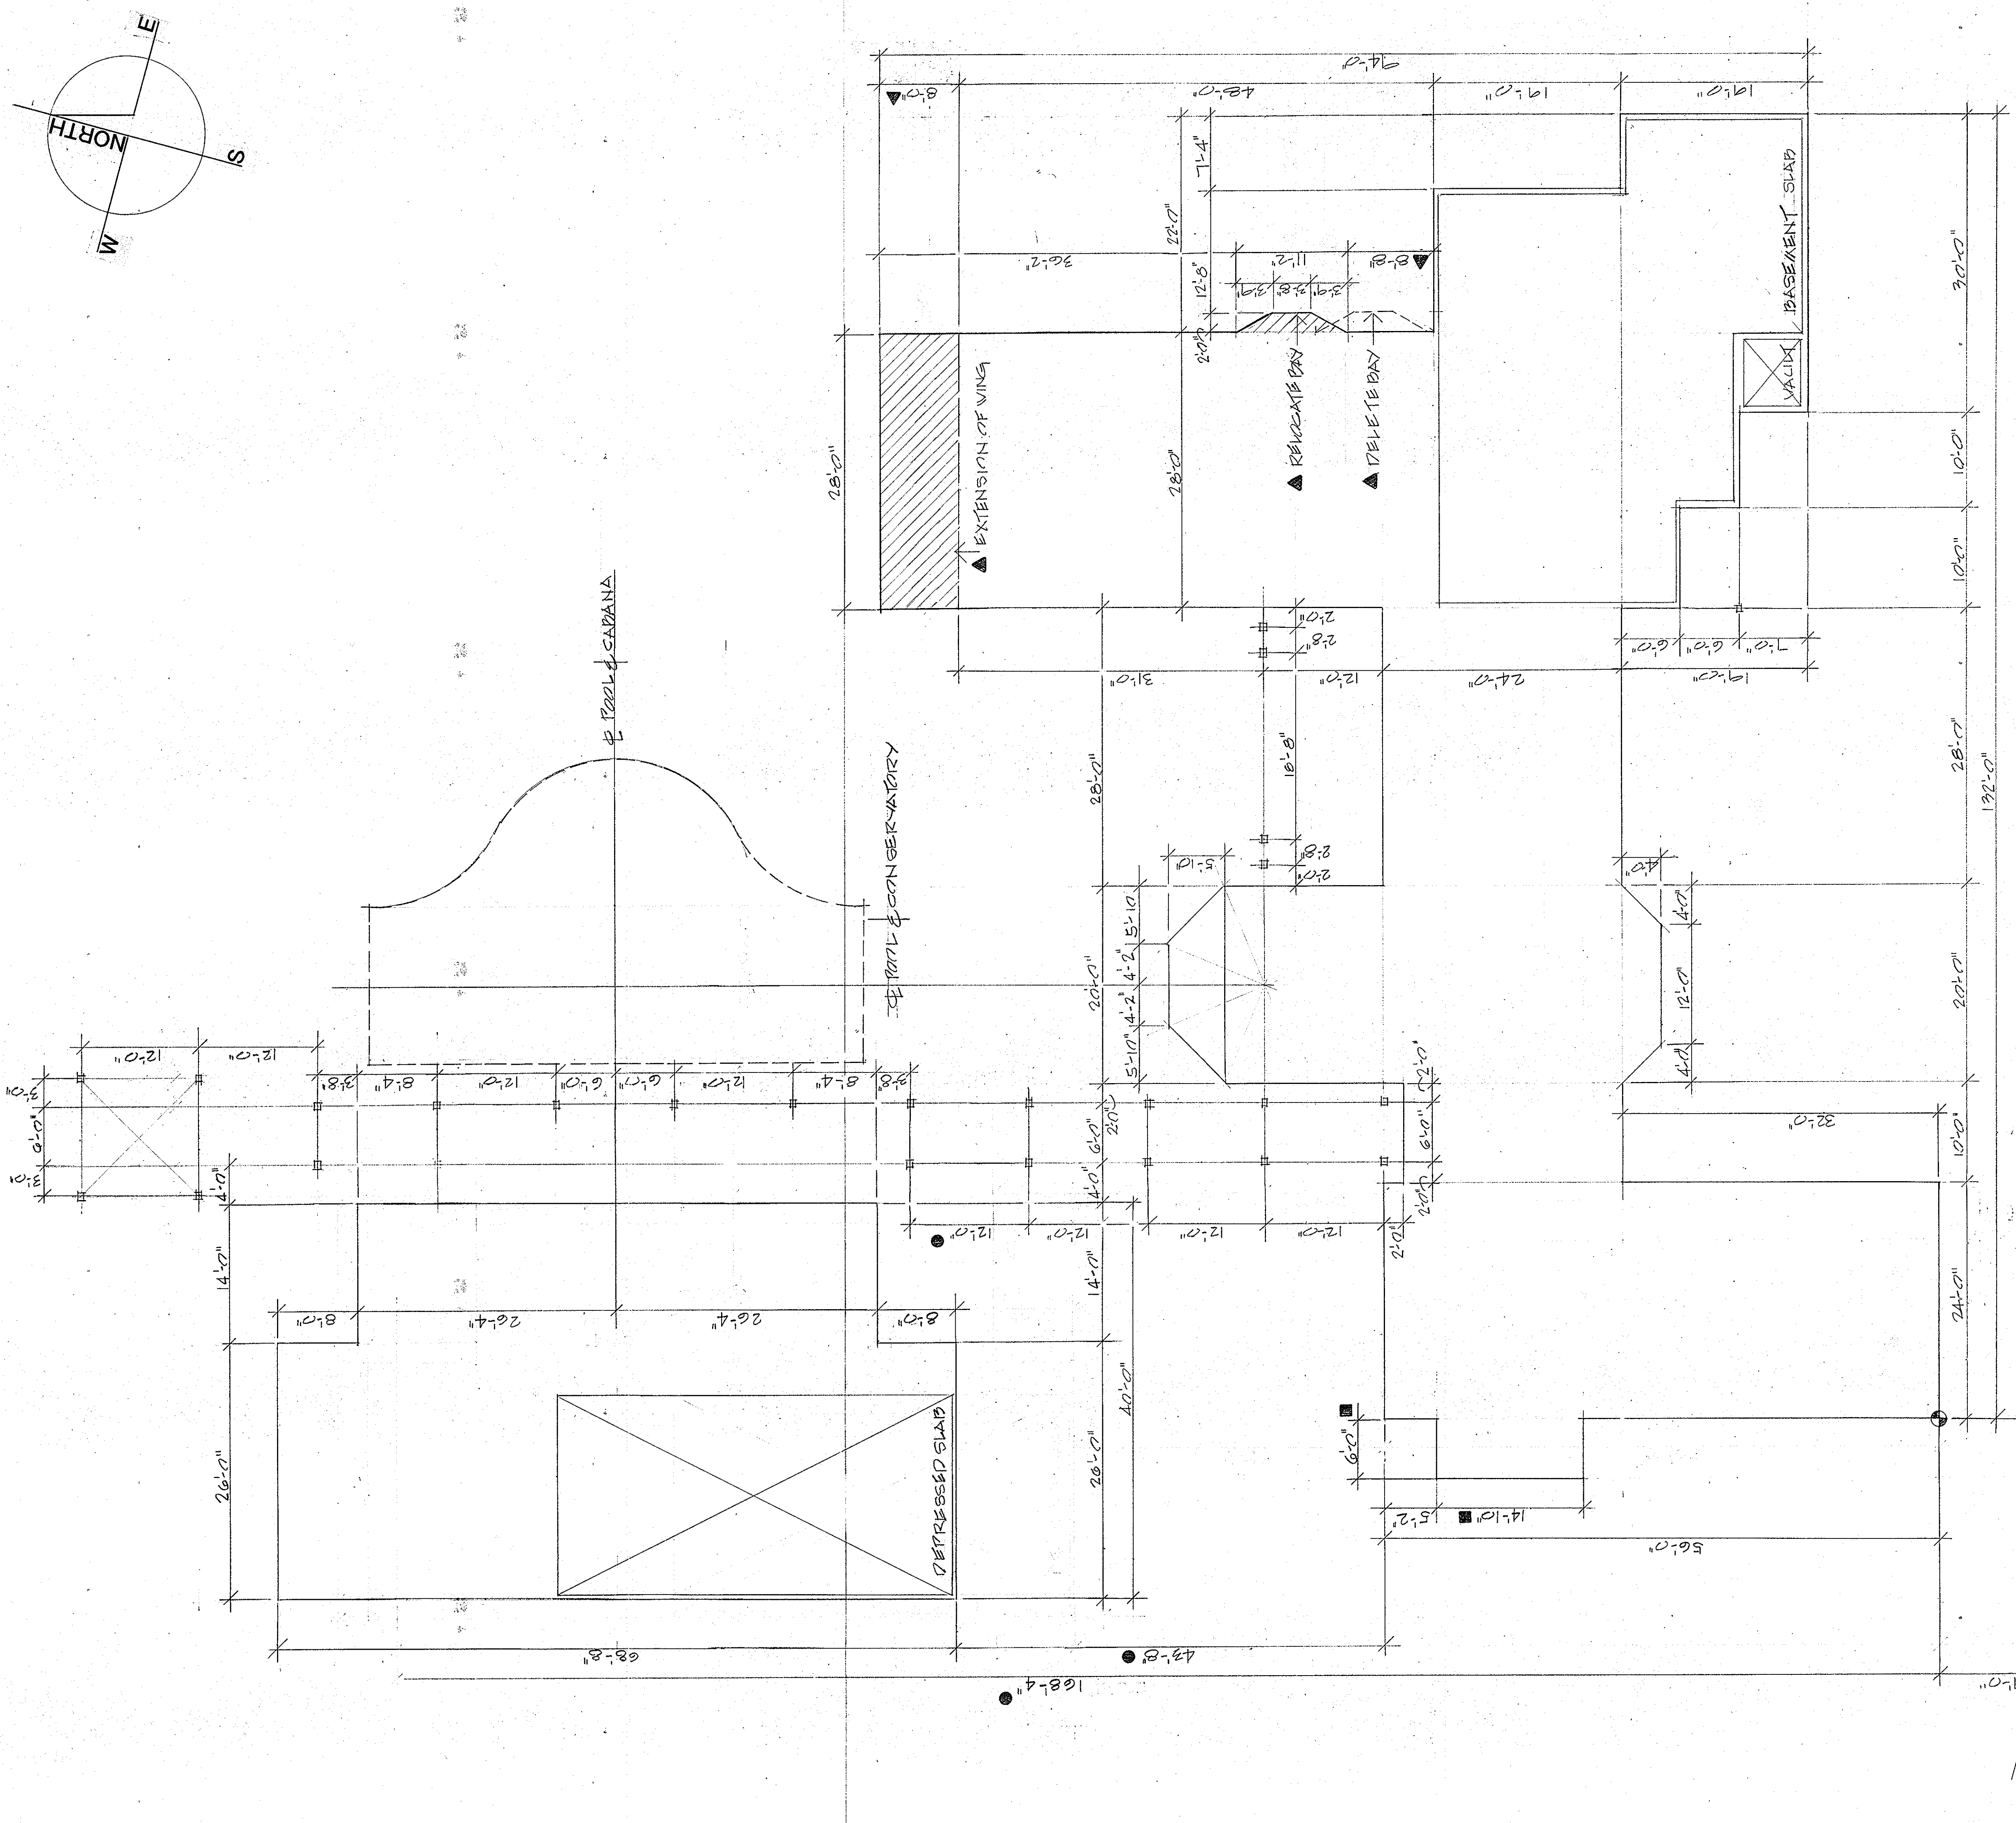


NOTE:  
STRUCTURE OUTLINE IS TO E OF  
EXISTING. 8" CONC. BLOCK FOUNDATION  
WALLS & FRAMING IS UNLESS NOTED  
OTHERWISE. REFER DETAILED PLANS  
& SECTIONS FOR COMPLETE DIMENSIONS.











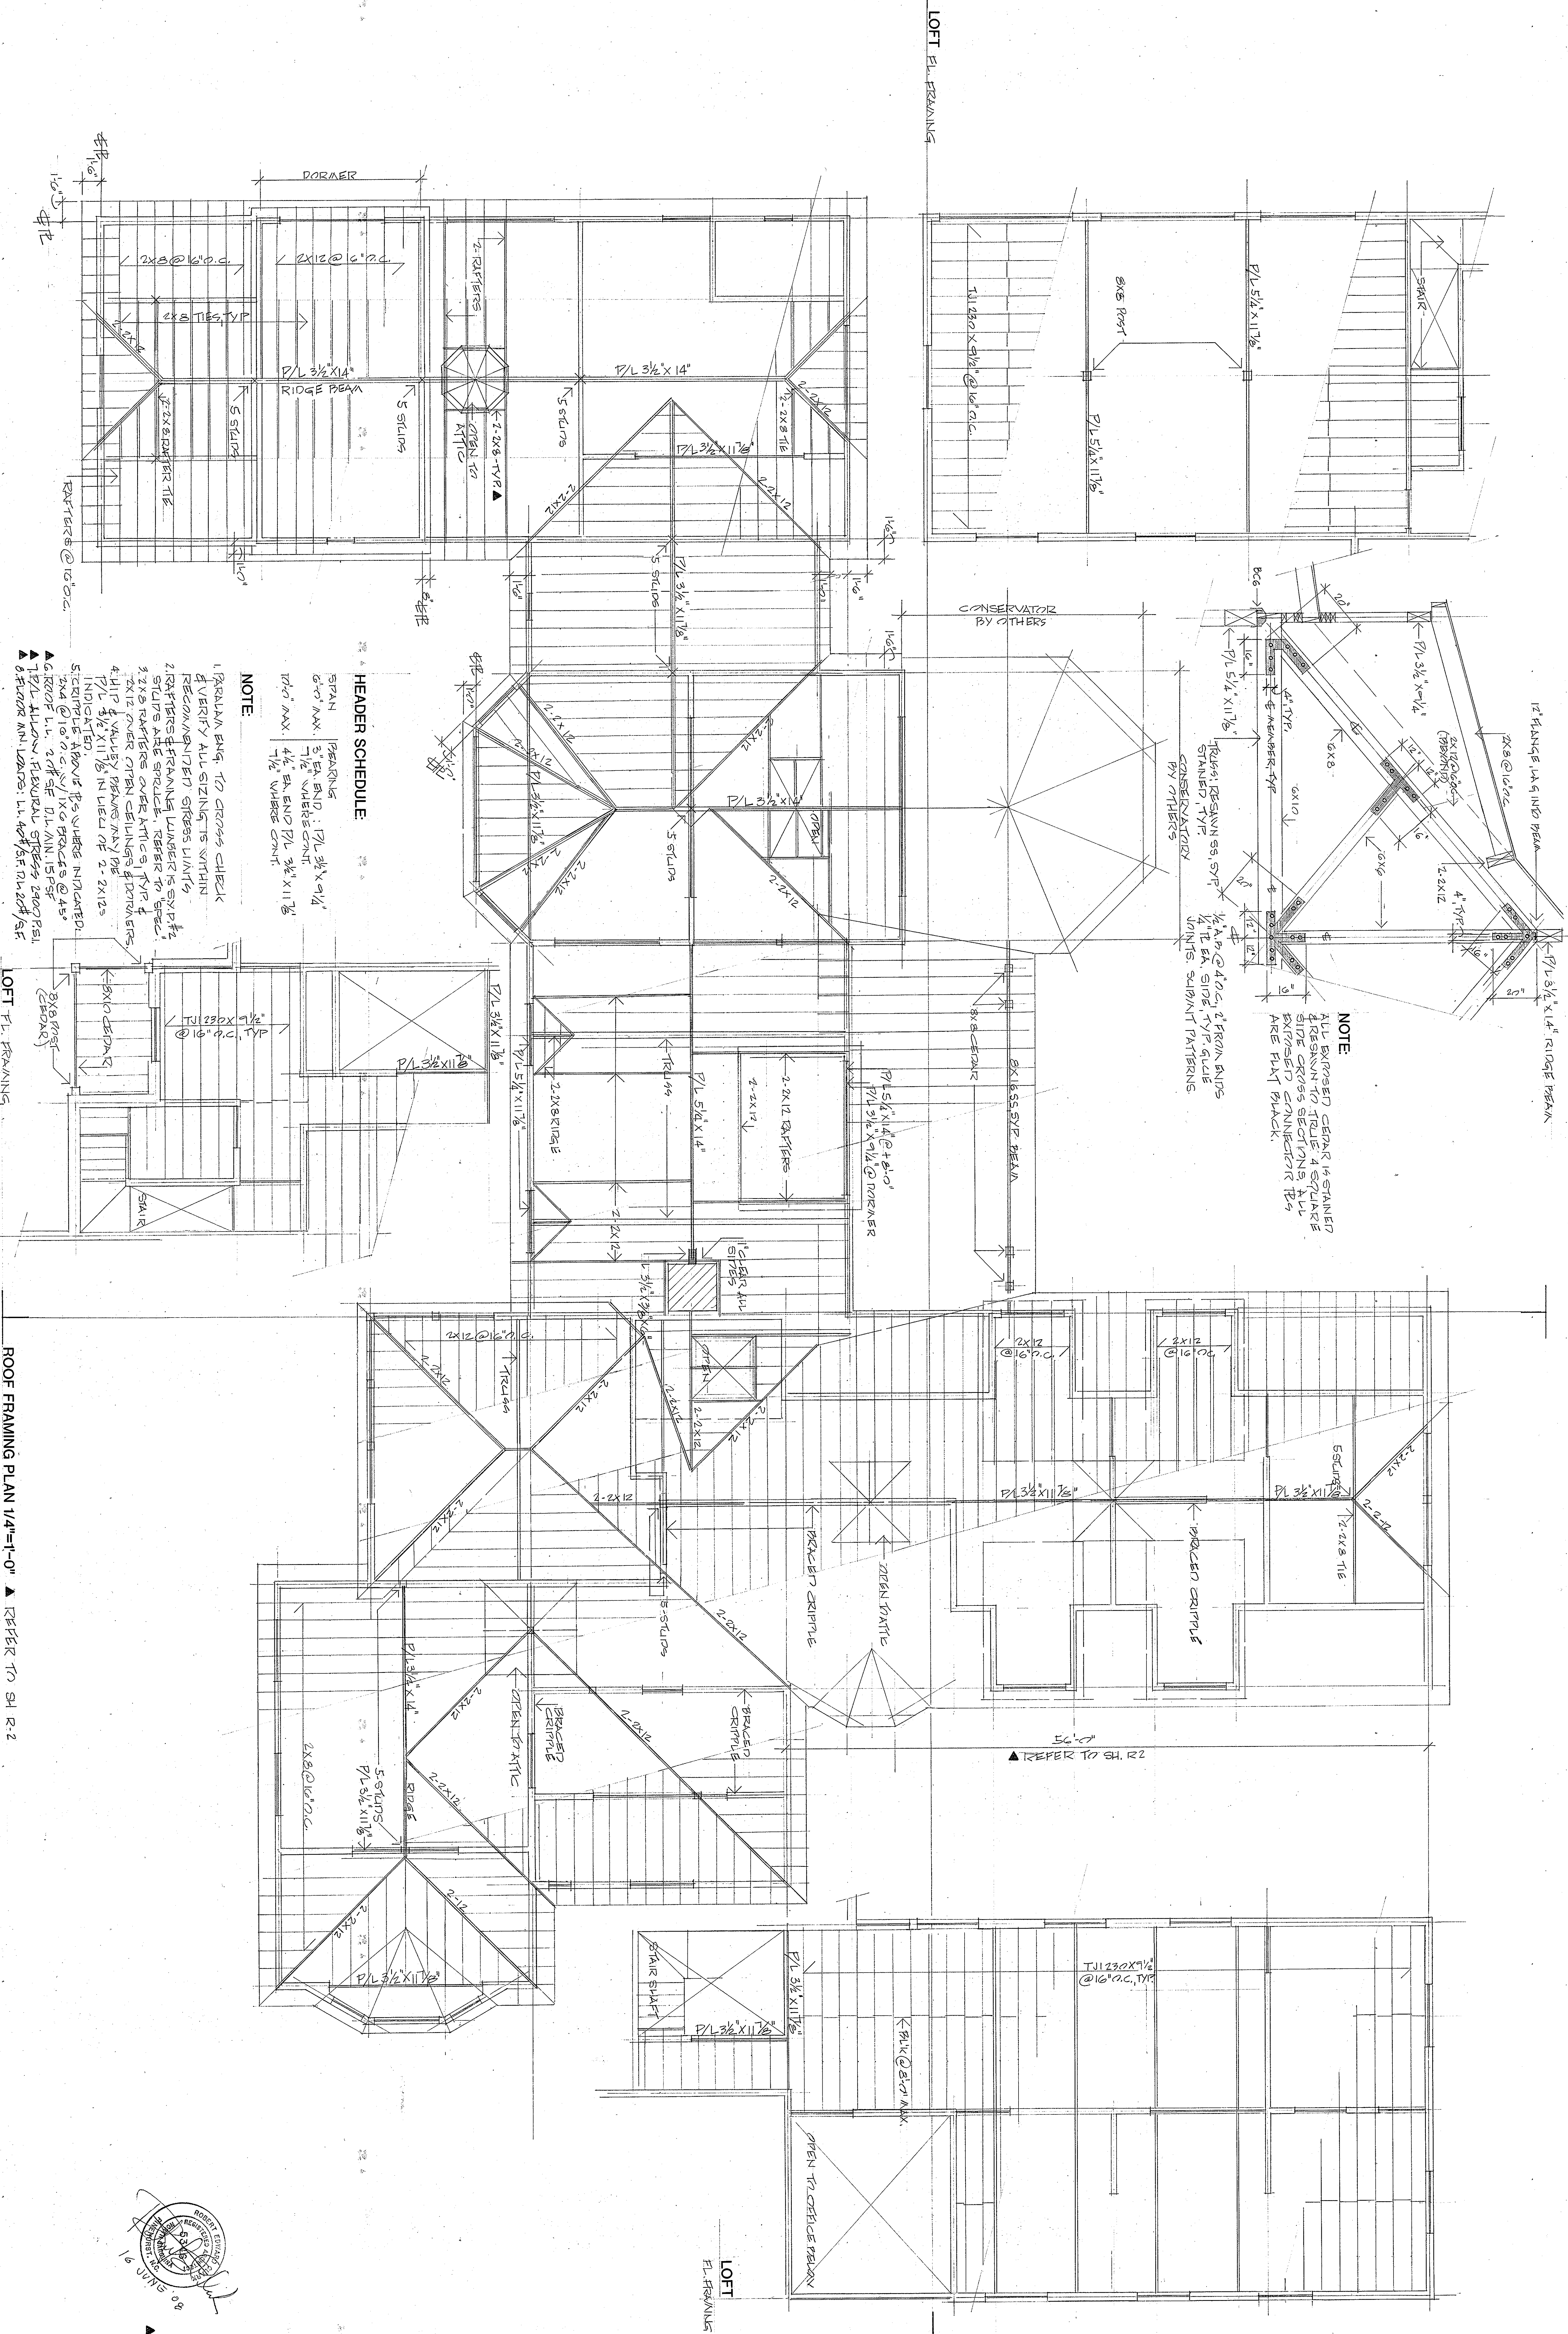



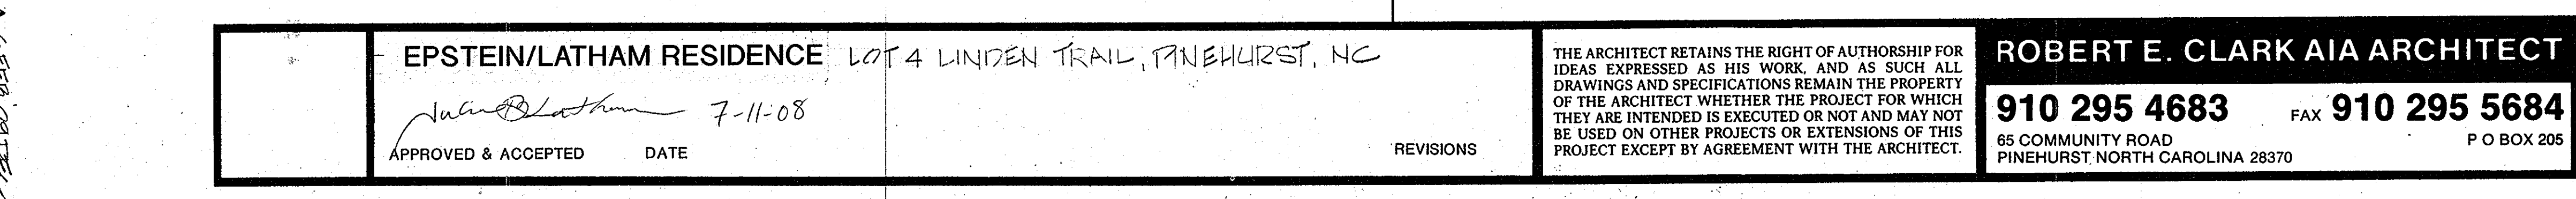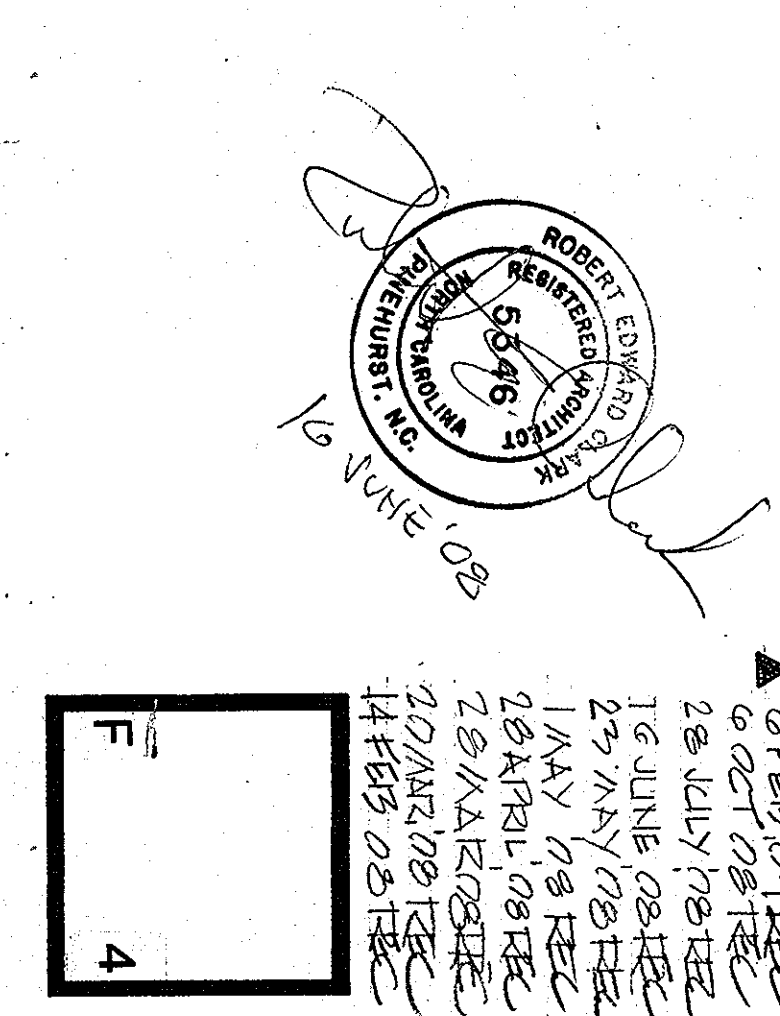



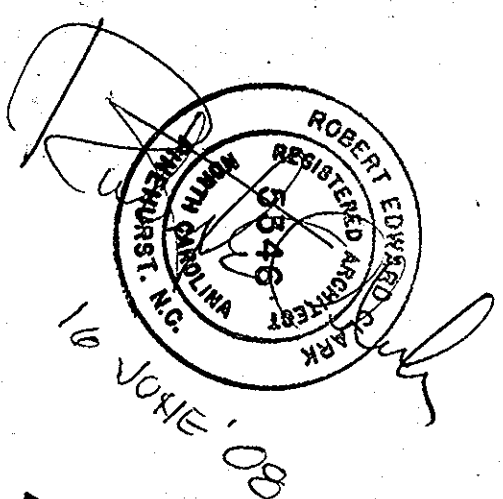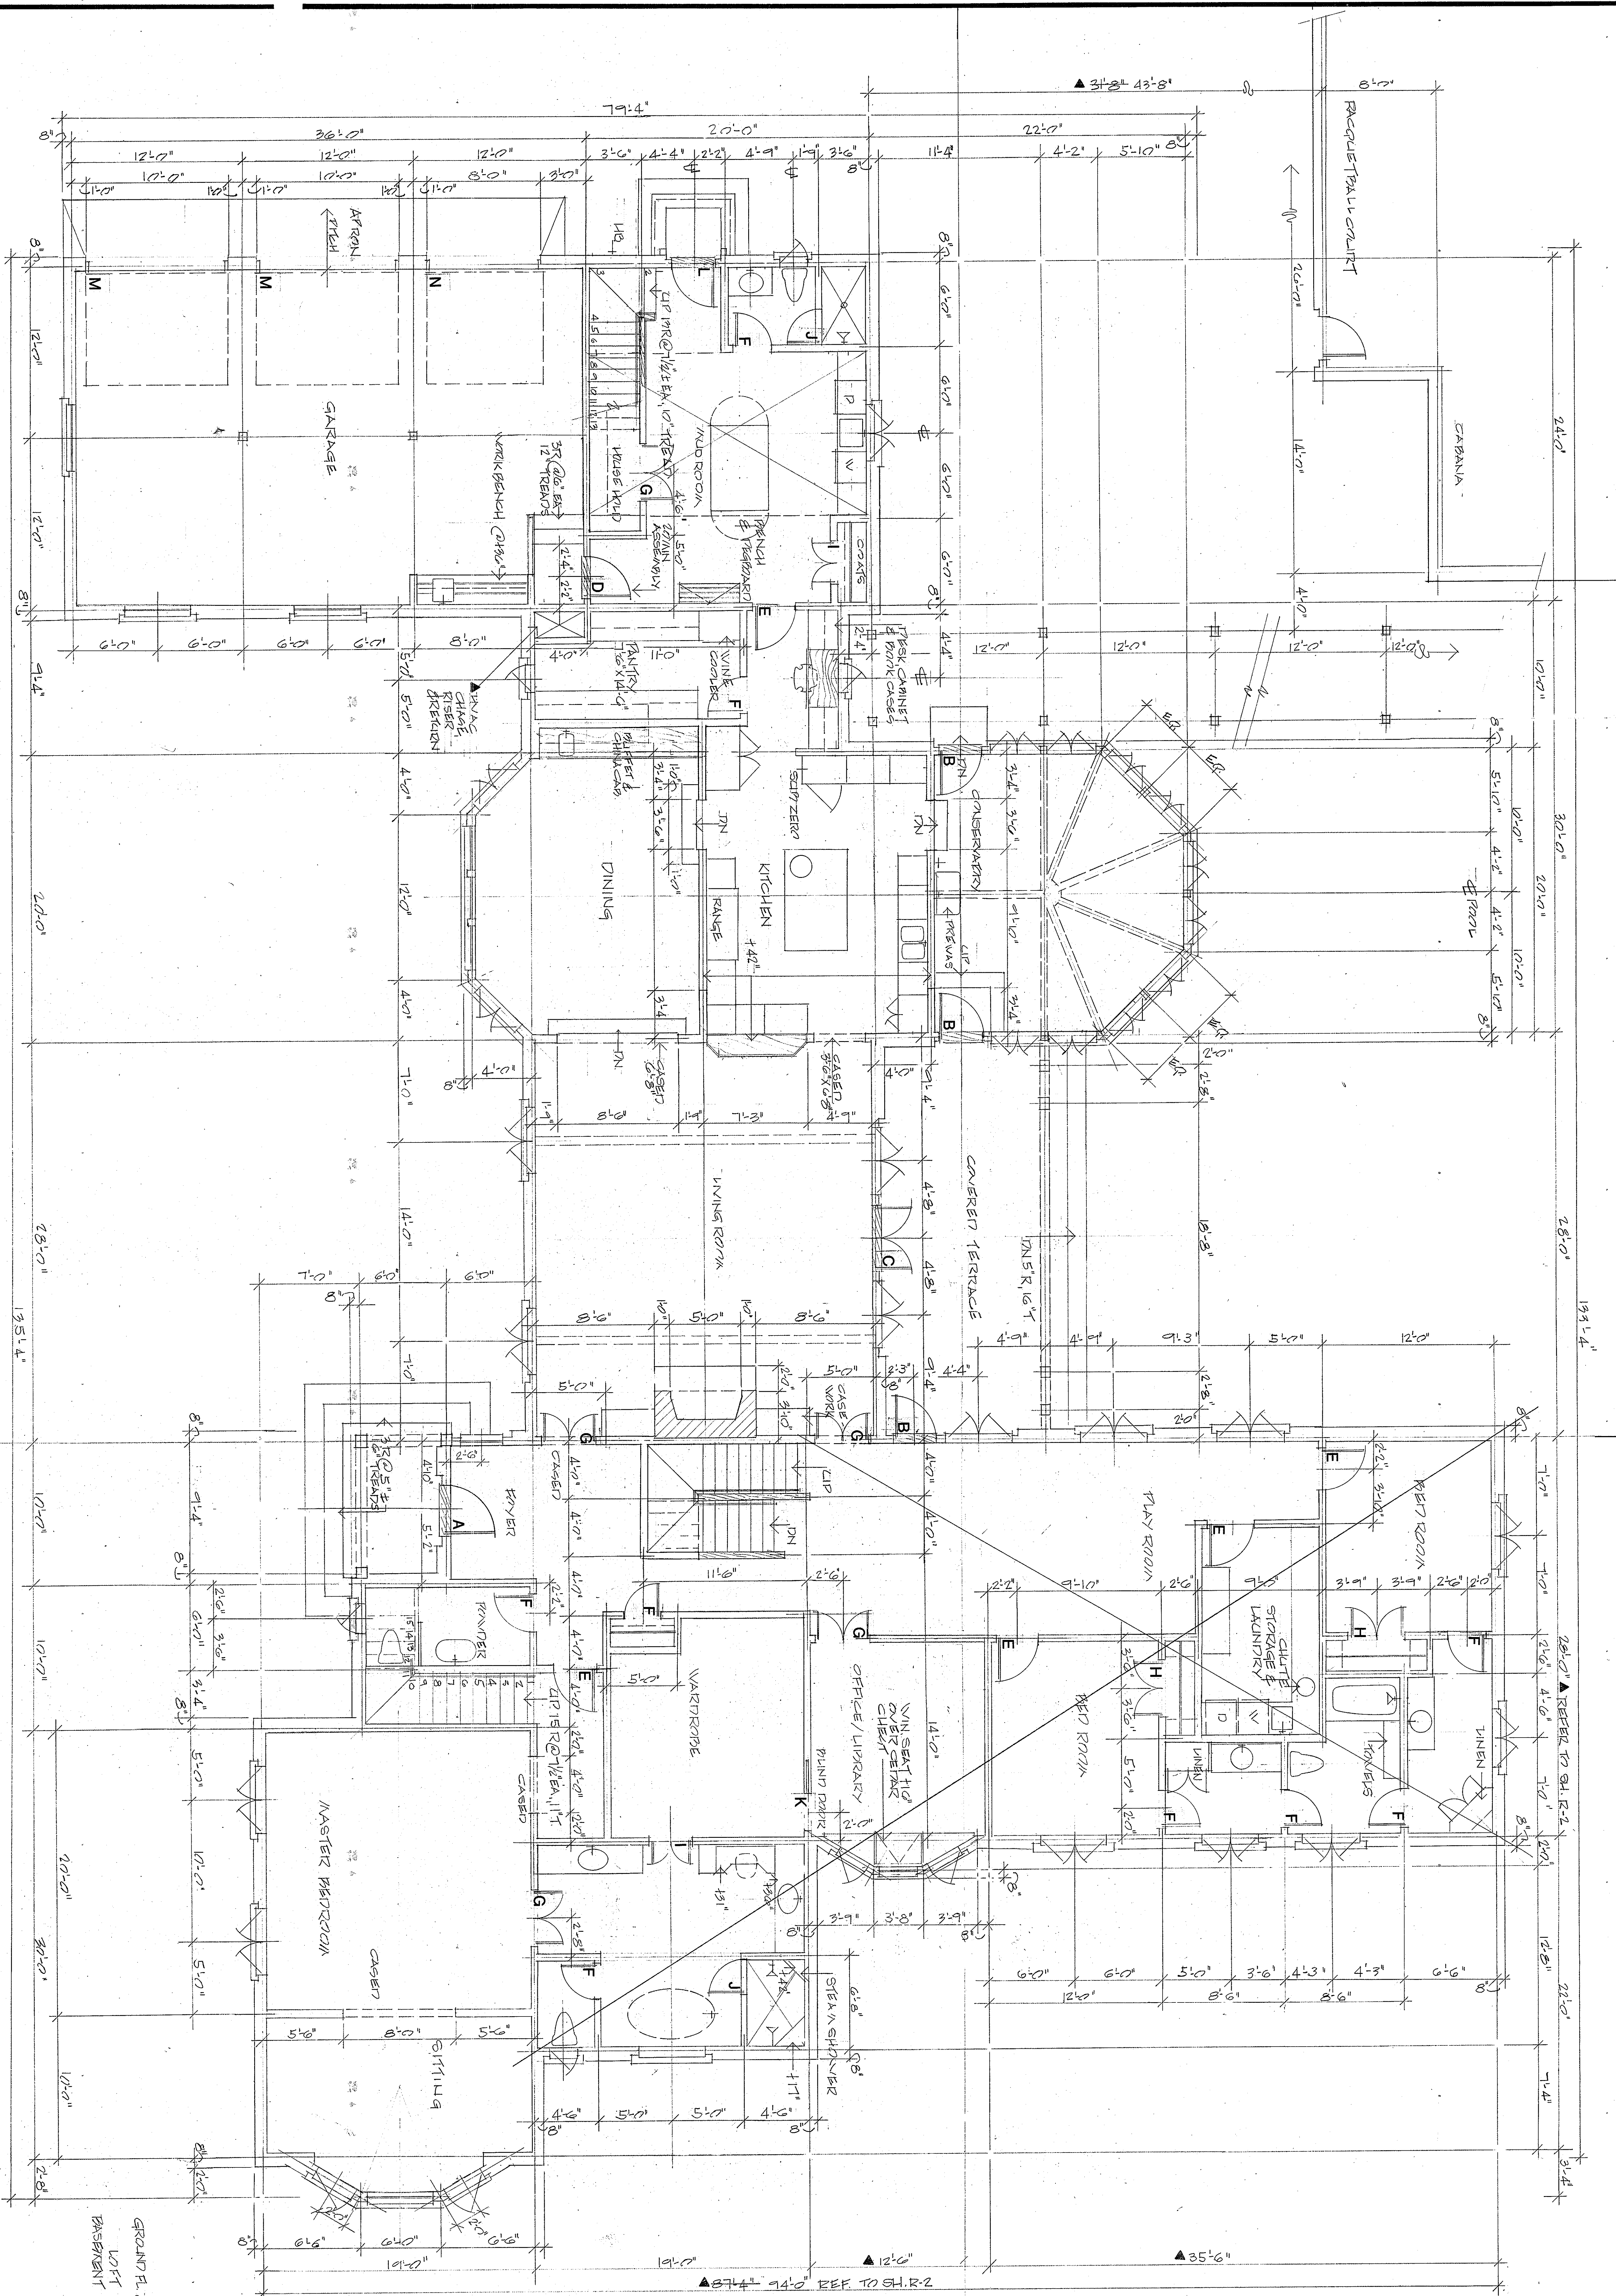

LEGEND:  
1. 6'x6'x6'x6'x6'x6'  
2. 6'x6'x6'x6'x6'x6'  
APPROVED & ACCEPTED

DATE 7-11-08

REVISIONS



THE ARCHITECT RETAINS THE RIGHT OF AUTHORSHIP FOR IDEAS EXPRESSED AS HIS WORK, AND AS SUCH ALL DRAWINGS AND SPECIFICATIONS REMAIN THE PROPERTY OF THE ARCHITECT. WHETHER THE PROJECT FOR WHICH THEY ARE INTENDED IS EXECUTED OR NOT, AND MAY NOT BE USED ON OTHER PROJECTS OR EXTENSIONS OF THIS PROJECT EXCEPT BY AGREEMENT WITH THE ARCHITECT.

ROBERT E. CLARK AIA ARCHITECT

910 295 4683 FAX 910 295 5684

85 COMMUNITY ROAD PINEHURST NORTH CAROLINA 28370 P O BOX 205



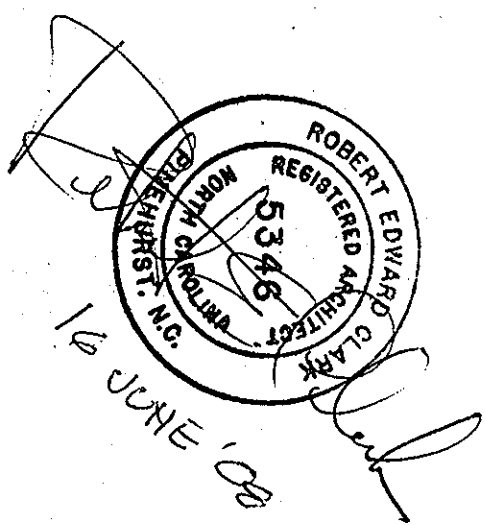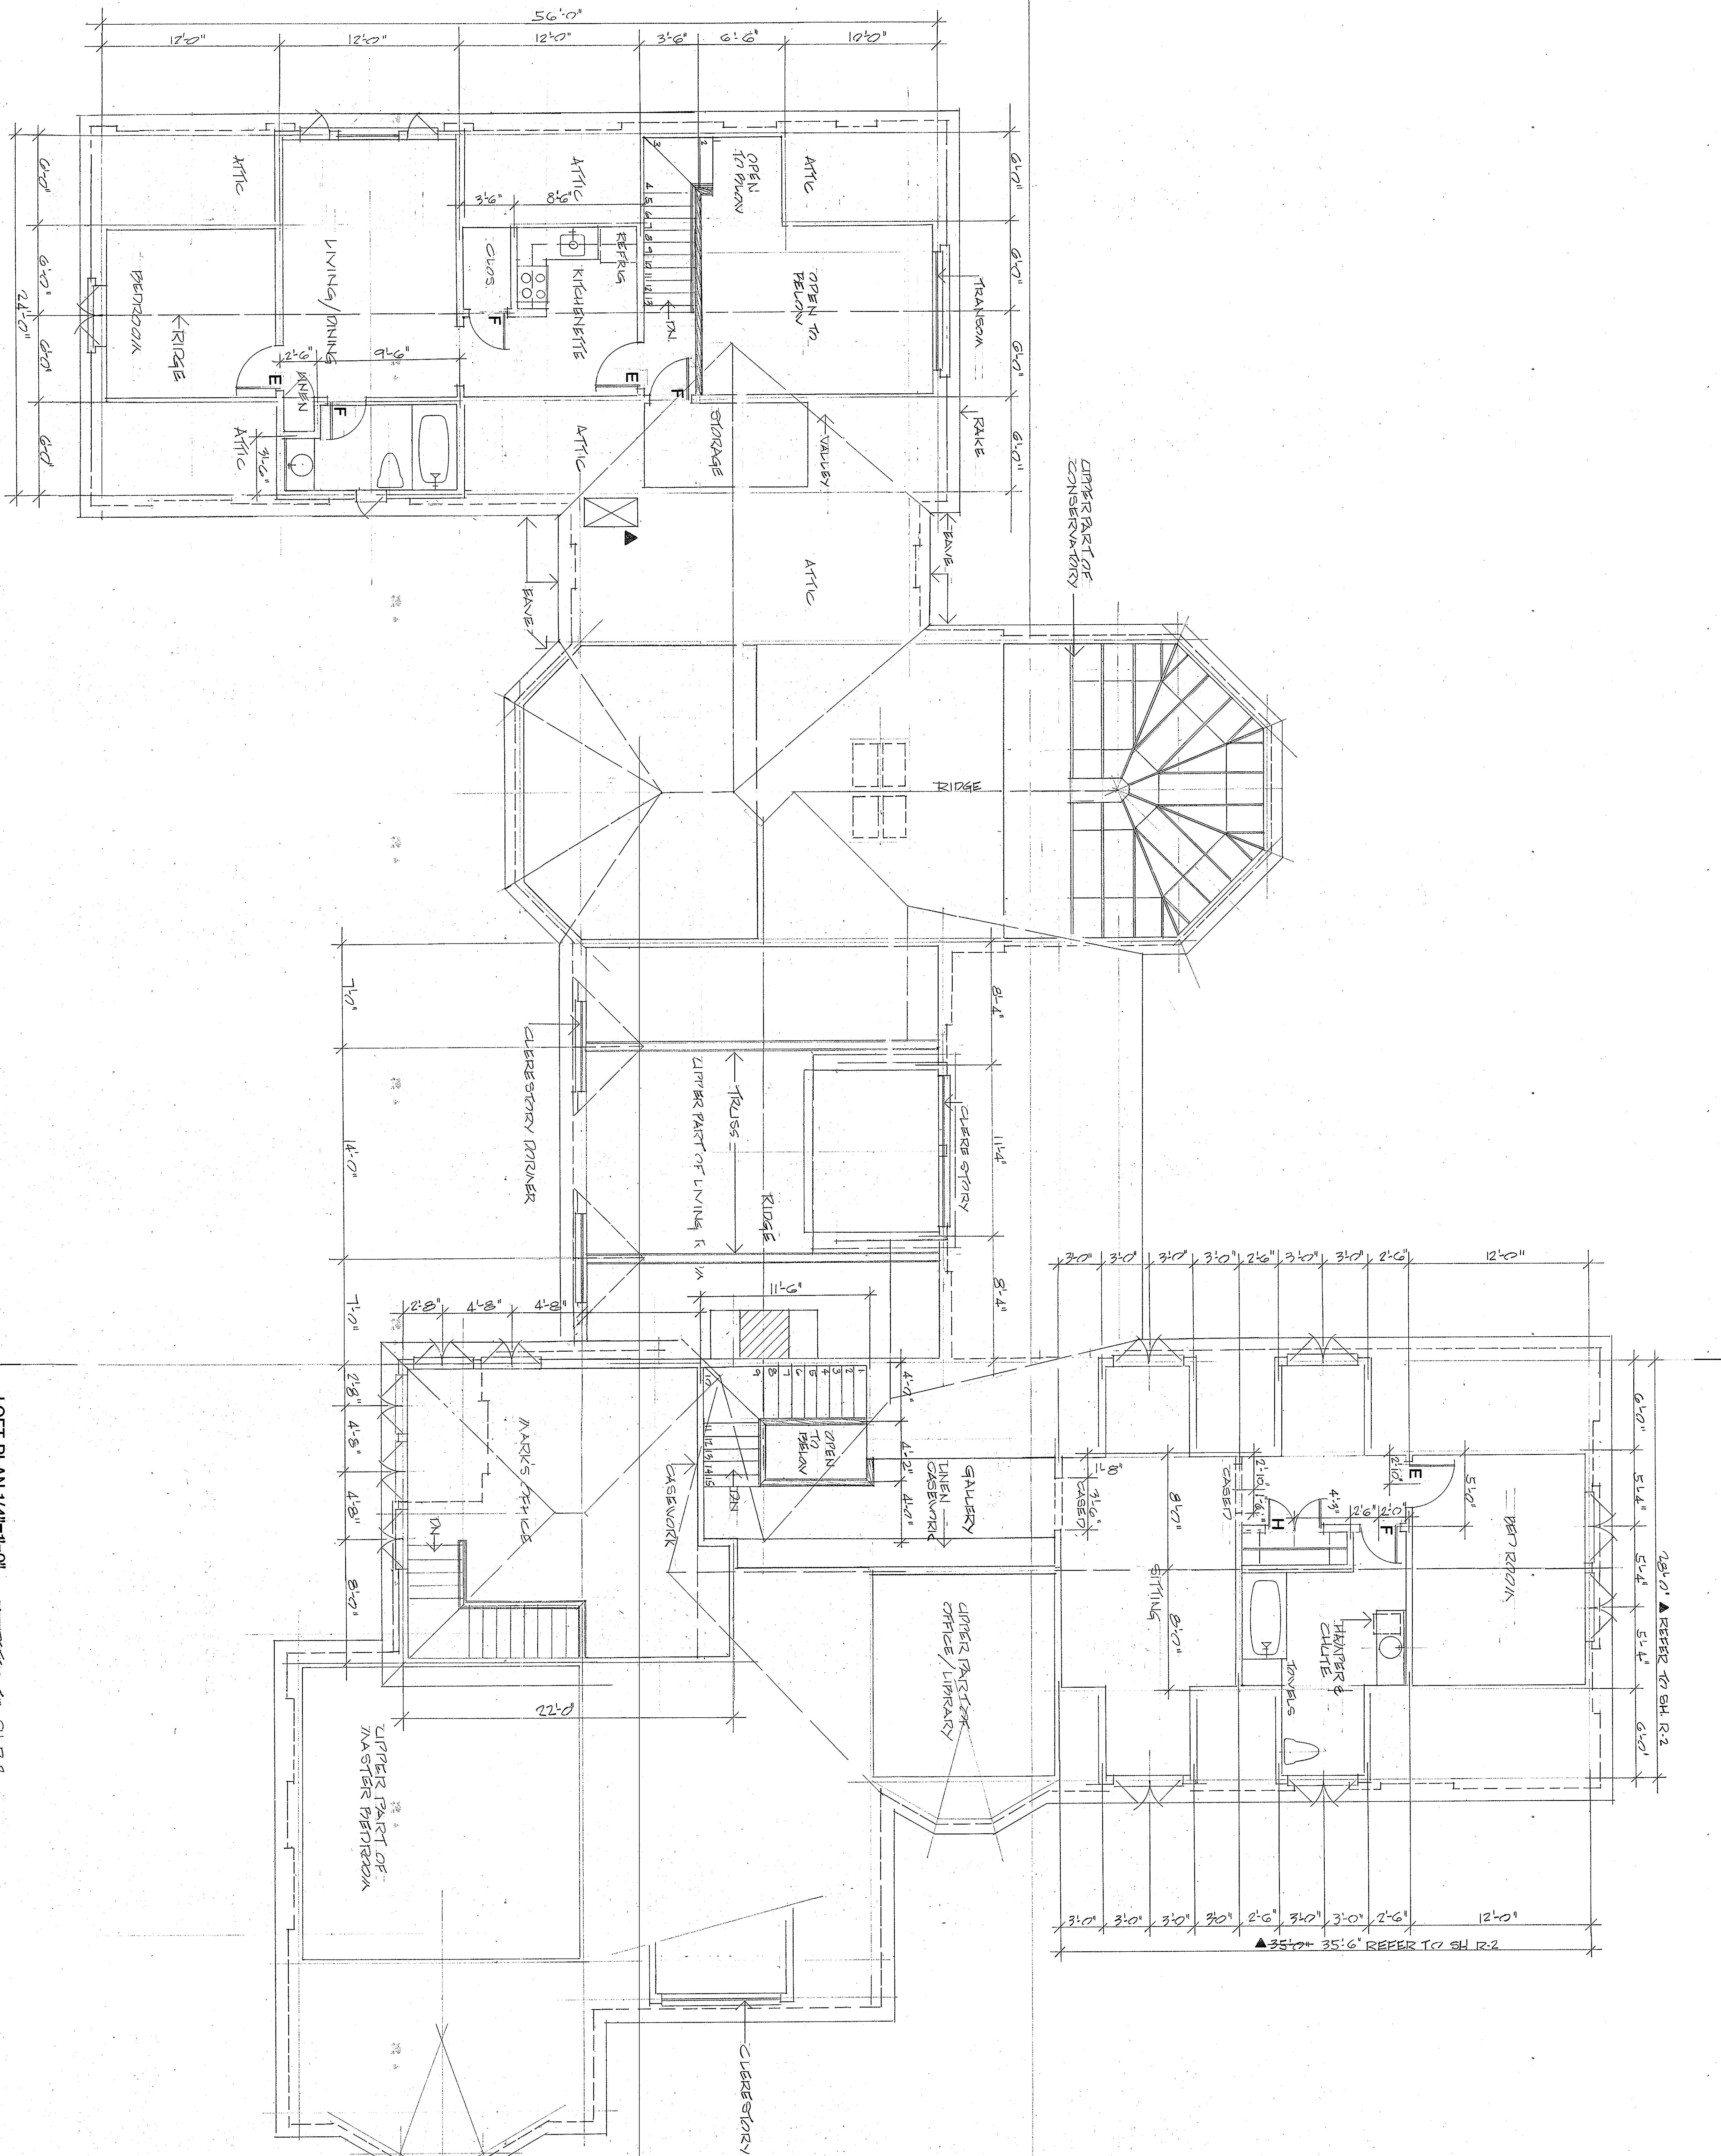

EPSTEIN/LATHAM RESIDENCE LOT 4 LINDEN TRAIL, PINEHURST, NC

APPROVED & ACCEPTED

DATE 7-11-08

## REVISIONS

THE ARCHITECT RETAINS THE RIGHT OF AUTHORSHIP FOR IDEAS EXPRESSED AS HIS WORK. AND AS SUCH ALL DRAWINGS AND SPECIFICATIONS REMAIN THE PROPERTY OF THE ARCHITECT WHETHER THE PROJECT FOR WHICH THEY ARE INTENDED IS EXECUTED OR NOT AND MAY NOT BE USED ON OTHER PROJECTS OR EXTENSIONS OF THIS PROJECT EXCEPT BY AGREEMENT WITH THE ARCHITECT.

ROBERT E. CLARK AIA ARCHITECT

**910 295 4683**

FAX **910 295 5684**


65 COMMUNITY ROAD  
RINEHURST NORTH CAROLINA 28370

P O BOX 205



Architectural drawings of a building facade, including elevations and sections. The drawings are numbered 1 through 17. Elevations 1-10 show the front facade with various window and door arrangements. Elevation 11 shows a side elevation. Elevation 12 shows a section of the building. Elevation 13 shows a section of the building. Elevation 14 shows a section of the building. Elevation 15 shows a section of the building. Elevation 16 shows a section of the building. Elevation 17 shows a section of the building. The drawings include dimensions and labels for materials and construction details.

1. DENTAL GLASS BY DUL. LOW E, CLAR (WHITE), TEARDROPPED WHERE REQUIRED BY PER CODE, INTERIOR HARDWARE (WHITE, MARVIN, ANDERSON OR APPROVED EQUAL INSTALLATION FLASHING AS RECOMMENDED BY MANUFACTURER, TRANCOS WASHER INDICATED 2. SUBSTITUTES AS SELECTED, STAINED CEDAR OR APPROVED EQUAL, HINGED HARDWARE (BUTT PLACK), SIZED TO MATCH ADJACENT SASH INSTALLATION PER MANUFACTURER'S RECOMMENDATIONS. 3. TRANSPIRANE PER APPROVED EQUAL. SEE DETAIL SH-1.9.

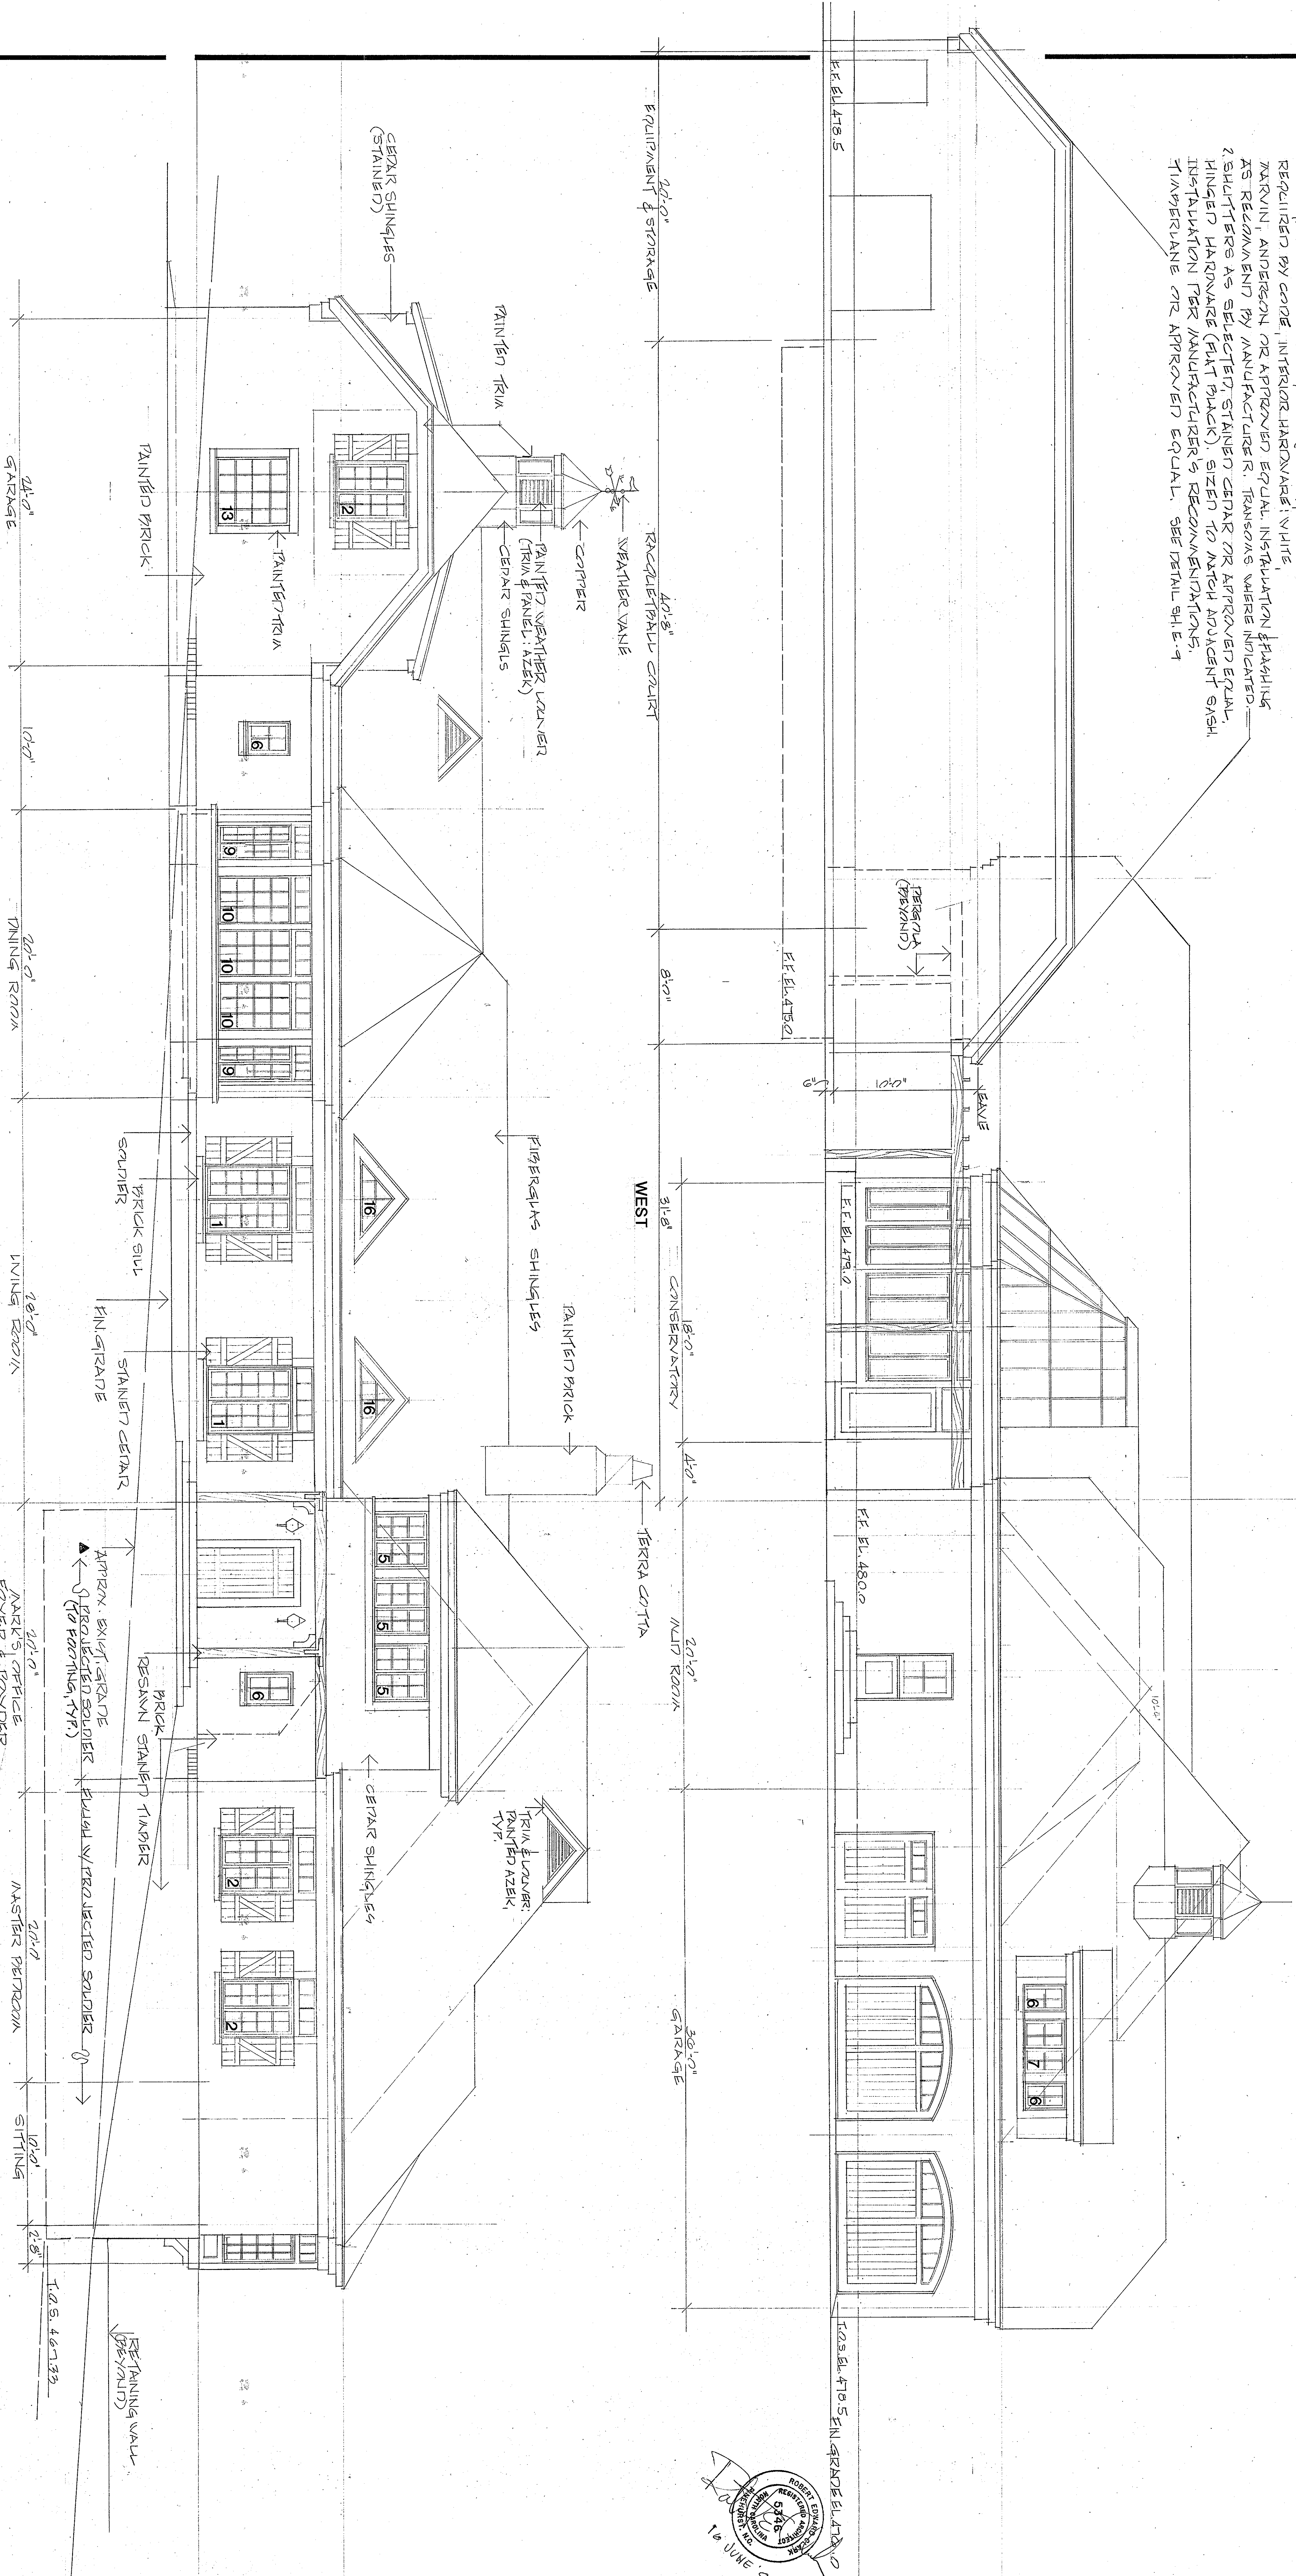

# SOUTH

EXTERIOR ELEVATIONS 1/4"=1'-0"

**NOTE:**

REFER TO DETAILS ON SHEETS 10 & PRI-  
NOTE THAT SOUTHER CRUISE IS PRO-  
JECTED AT FRAINED WALLS & REQUIRE 10N19 FLUSH  
INCLUDING BASEMENT & GARAGE TO FOOTINGS.  
THE CAPANA & RACQUETBALL WING  
DOES NOT HAVE A SOUTHER CRUISE.

# FOYER & COMPANY

401.04

RETAINING WALL  
(BRYAN)

7

EPSTEIN/LATHAM RESIDENCE ~~at~~ 4 LINDEN TRAIL, PINEHURST, NC

APPROVED & ACCEPTED

DATE 7-11-08

## REVISIONS

THE ARCHITECT RETAINS THE RIGHT OF AUTHORSHIP FOR IDEAS EXPRESSED AS HIS WORK, AND AS SUCH ALL DRAWINGS AND SPECIFICATIONS REMAIN THE PROPERTY OF THE ARCHITECT WHETHER THE PROJECT FOR WHICH THEY ARE INTENDED IS EXECUTED OR NOT AND MAY NOT BE USED ON OTHER PROJECTS OR EXTENSIONS OF THIS PROJECT EXCEPT BY AGREEMENT WITH THE ARCHITECT.


**ROBERT E. CLARK AIA ARCHITECT**

**910 295 4683**  
65 COMMUNITY ROAD  
PINEHURST NORTH CAROLINA

FAX **910 295 5684**

P O BOX 205



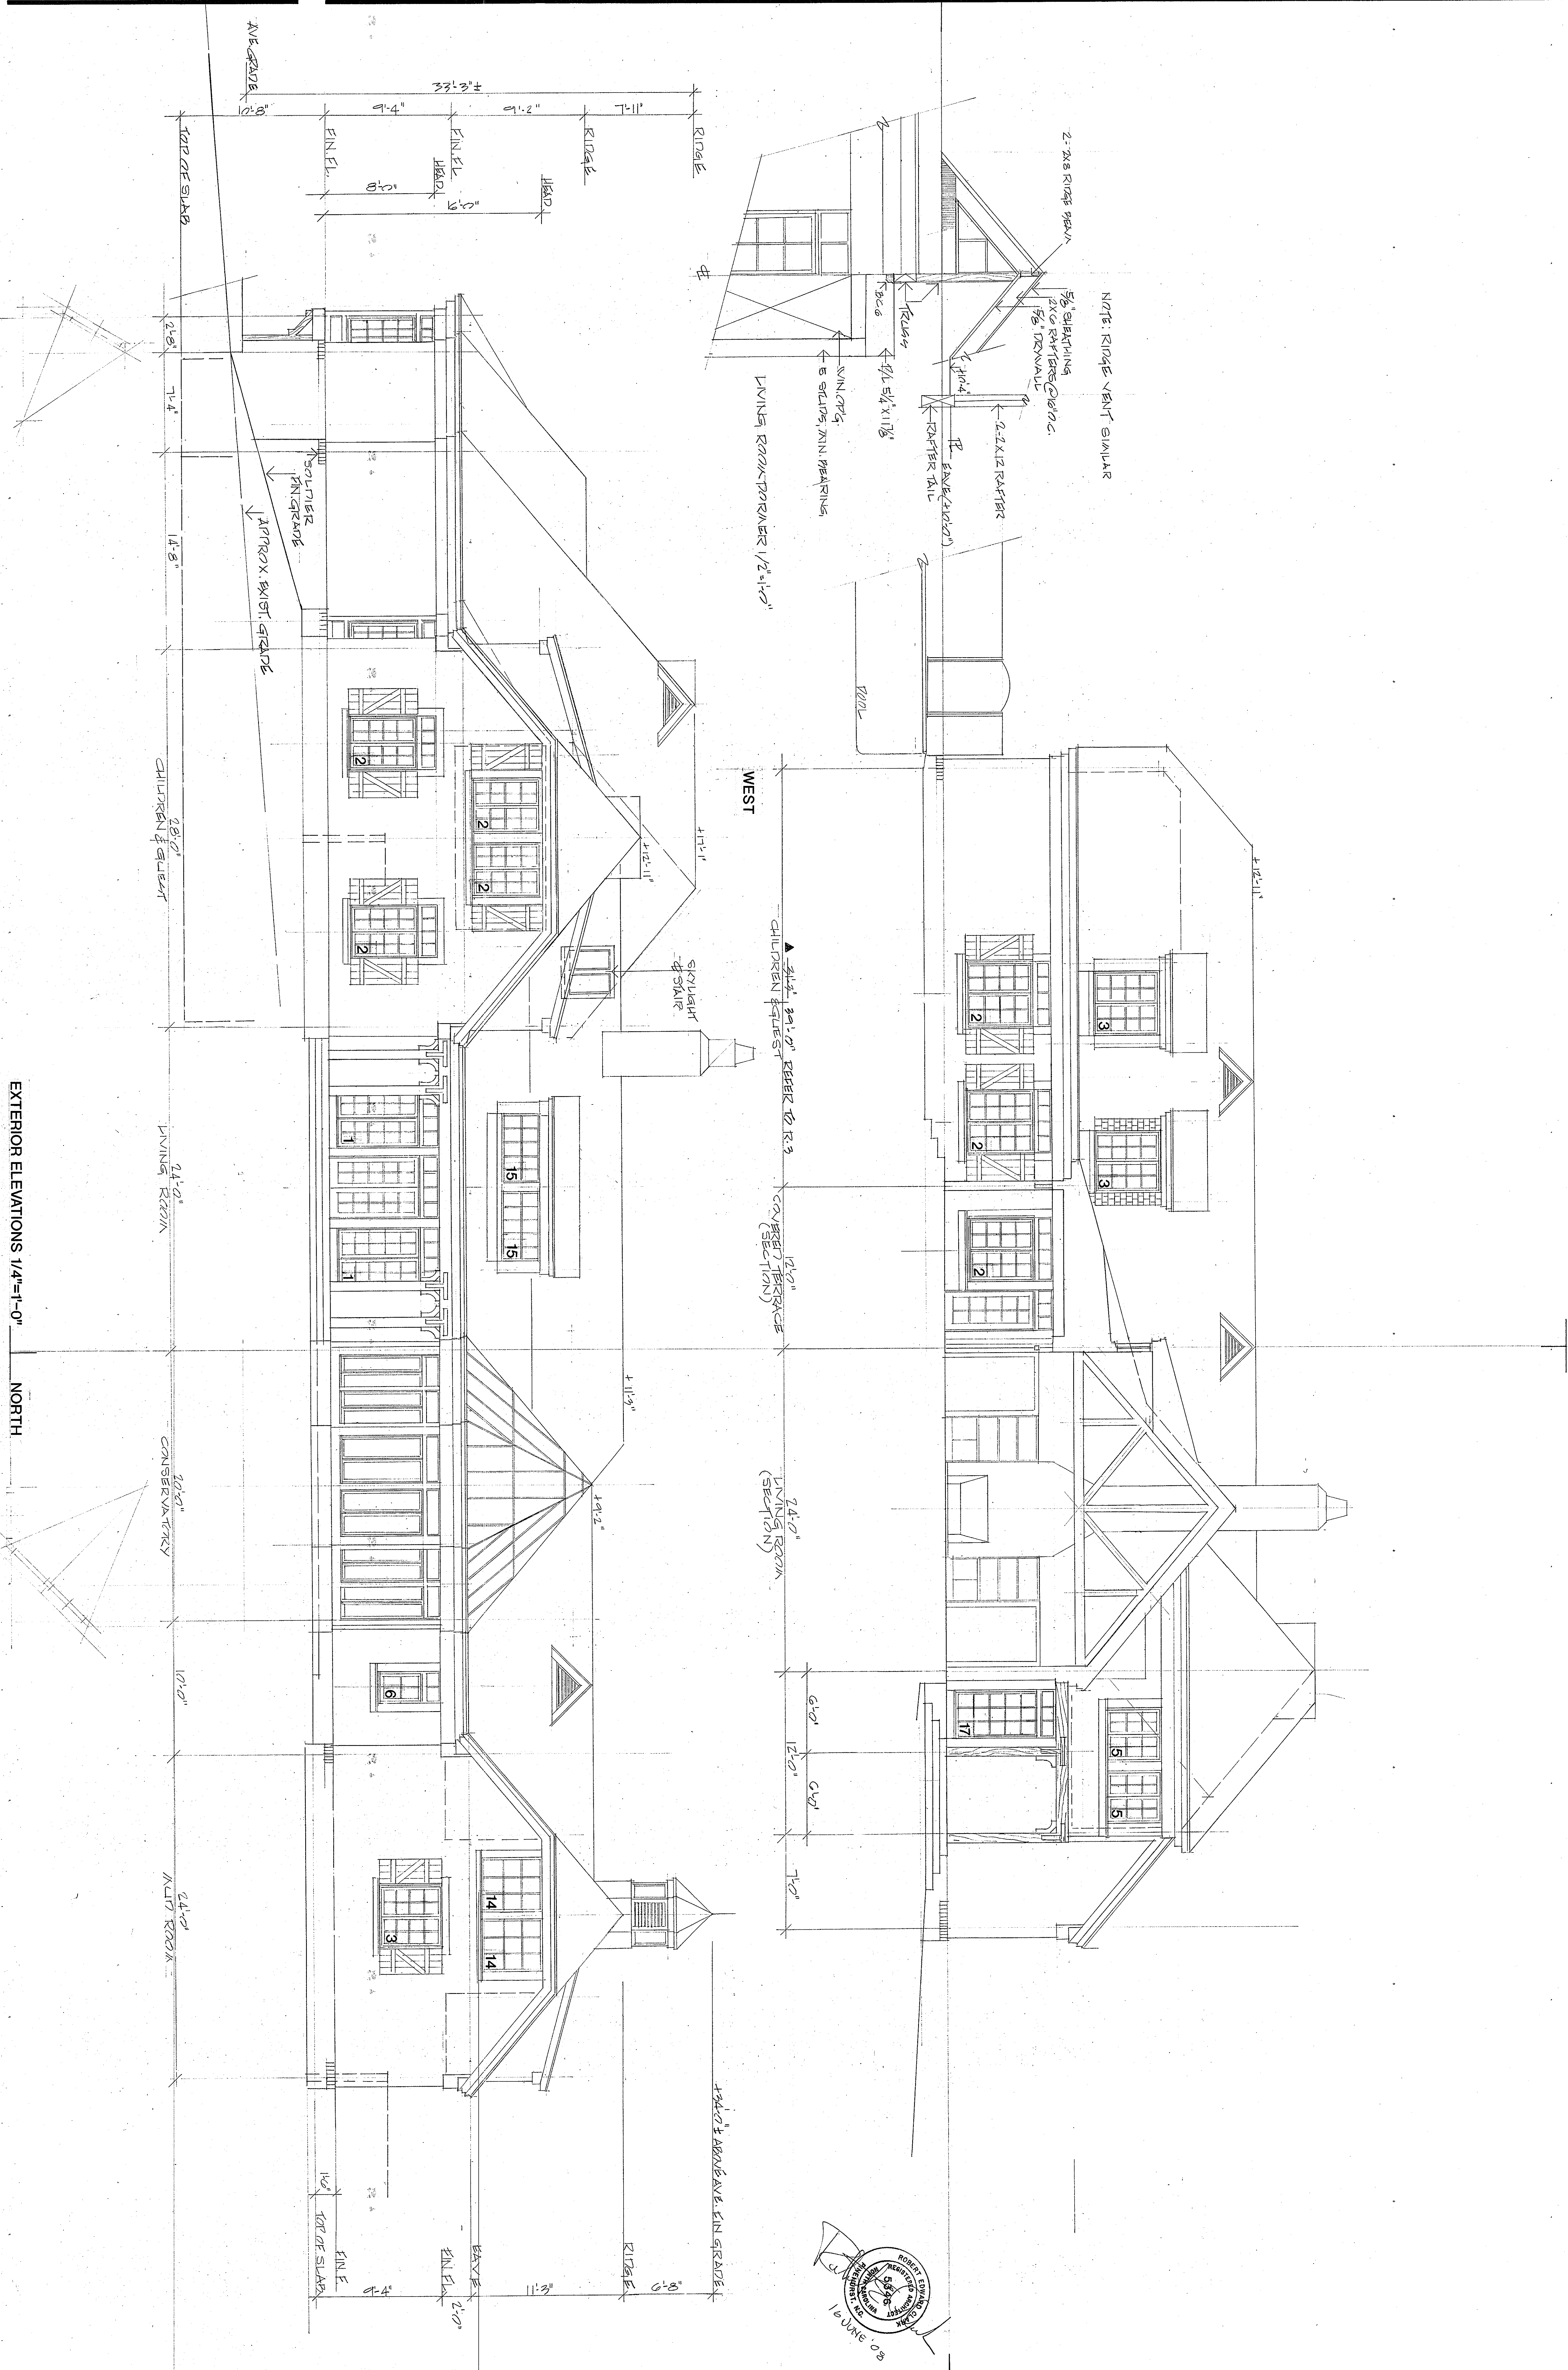

EXTERIOR ELEVATIONS 1/4"=1'-0" NORTH

▲ 6 FEB 07 REC  
6 OCT 08 REC  
28 JULY 08 REC  
16 JUNE 08 REC  
23 MAY 08 REC  
1 MAY 08 REC  
10 MAR 08 REC



|                                                            |                 |
|------------------------------------------------------------|-----------------|
| EPSTEIN/LATHAM RESIDENCE LOT 4 LINDEN TRAIL, PINEHURST, NC |                 |
| APPROVED & ACCEPTED<br><i>Julius B. Latham</i>             | DATE<br>7-11-08 |
| REVISIONS                                                  |                 |

|                                                     |                  |
|-----------------------------------------------------|------------------|
| ROBERT E. CLARK AIA ARCHITECT                       |                  |
| 910 295 4683                                        | FAX 910 295 5684 |
| 65 COMMUNITY ROAD<br>PINEHURST NORTH CAROLINA 28370 |                  |









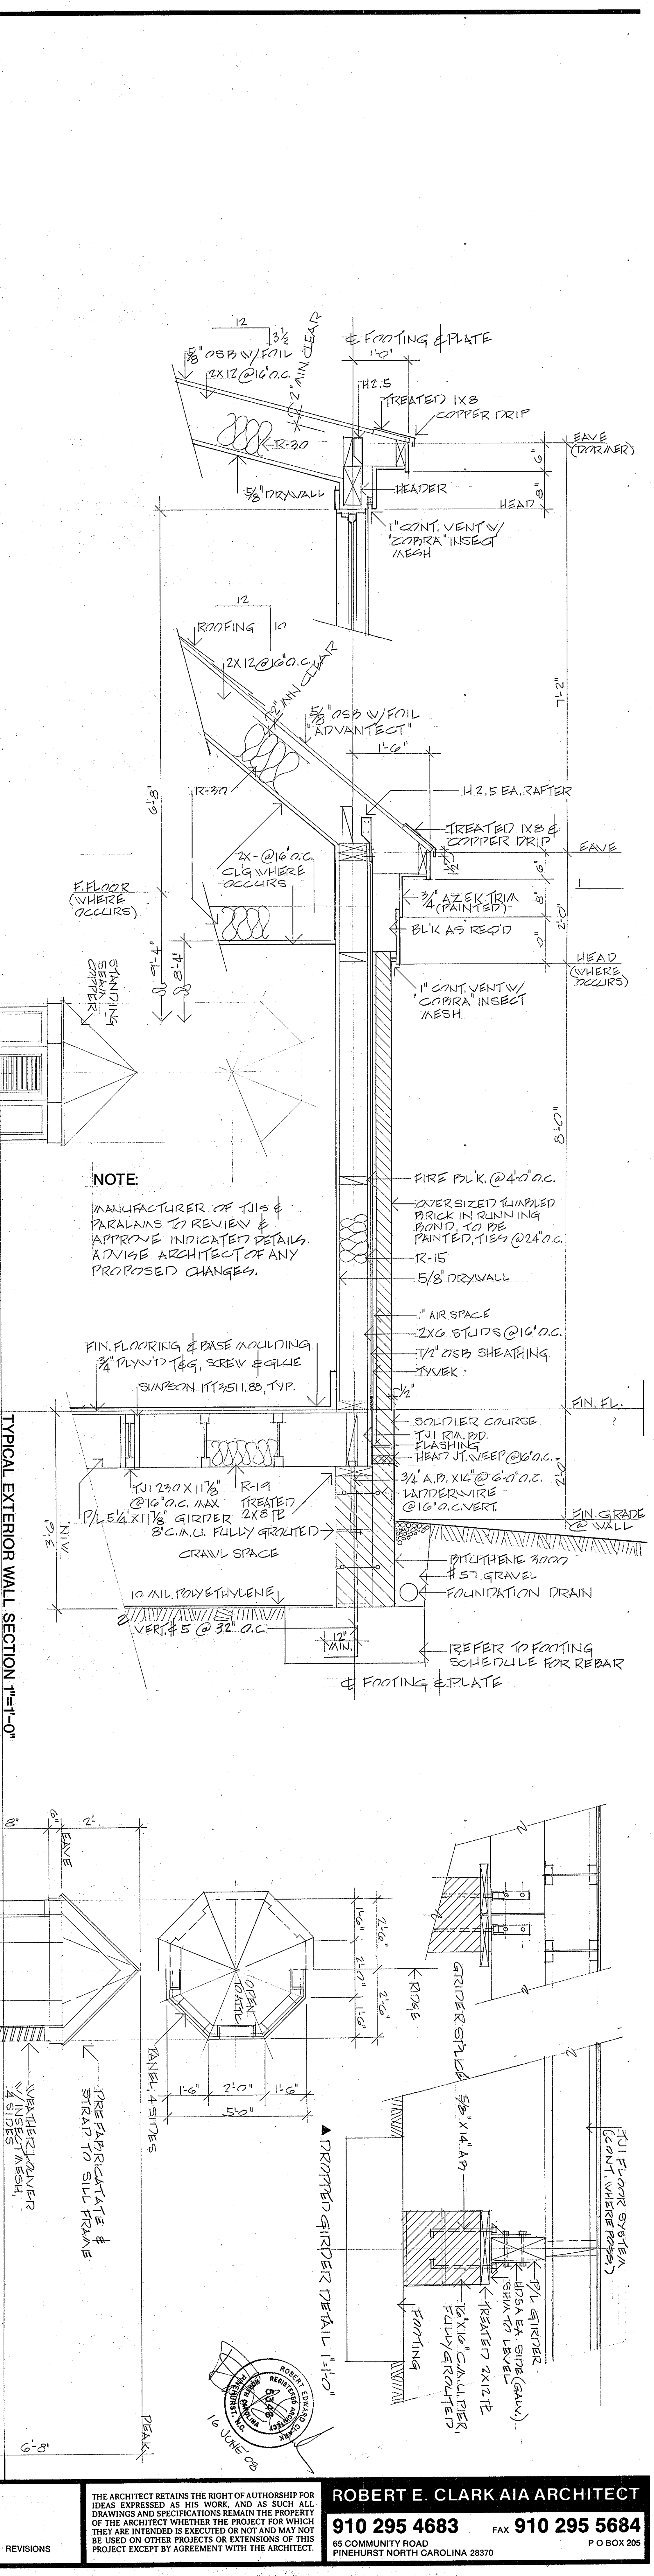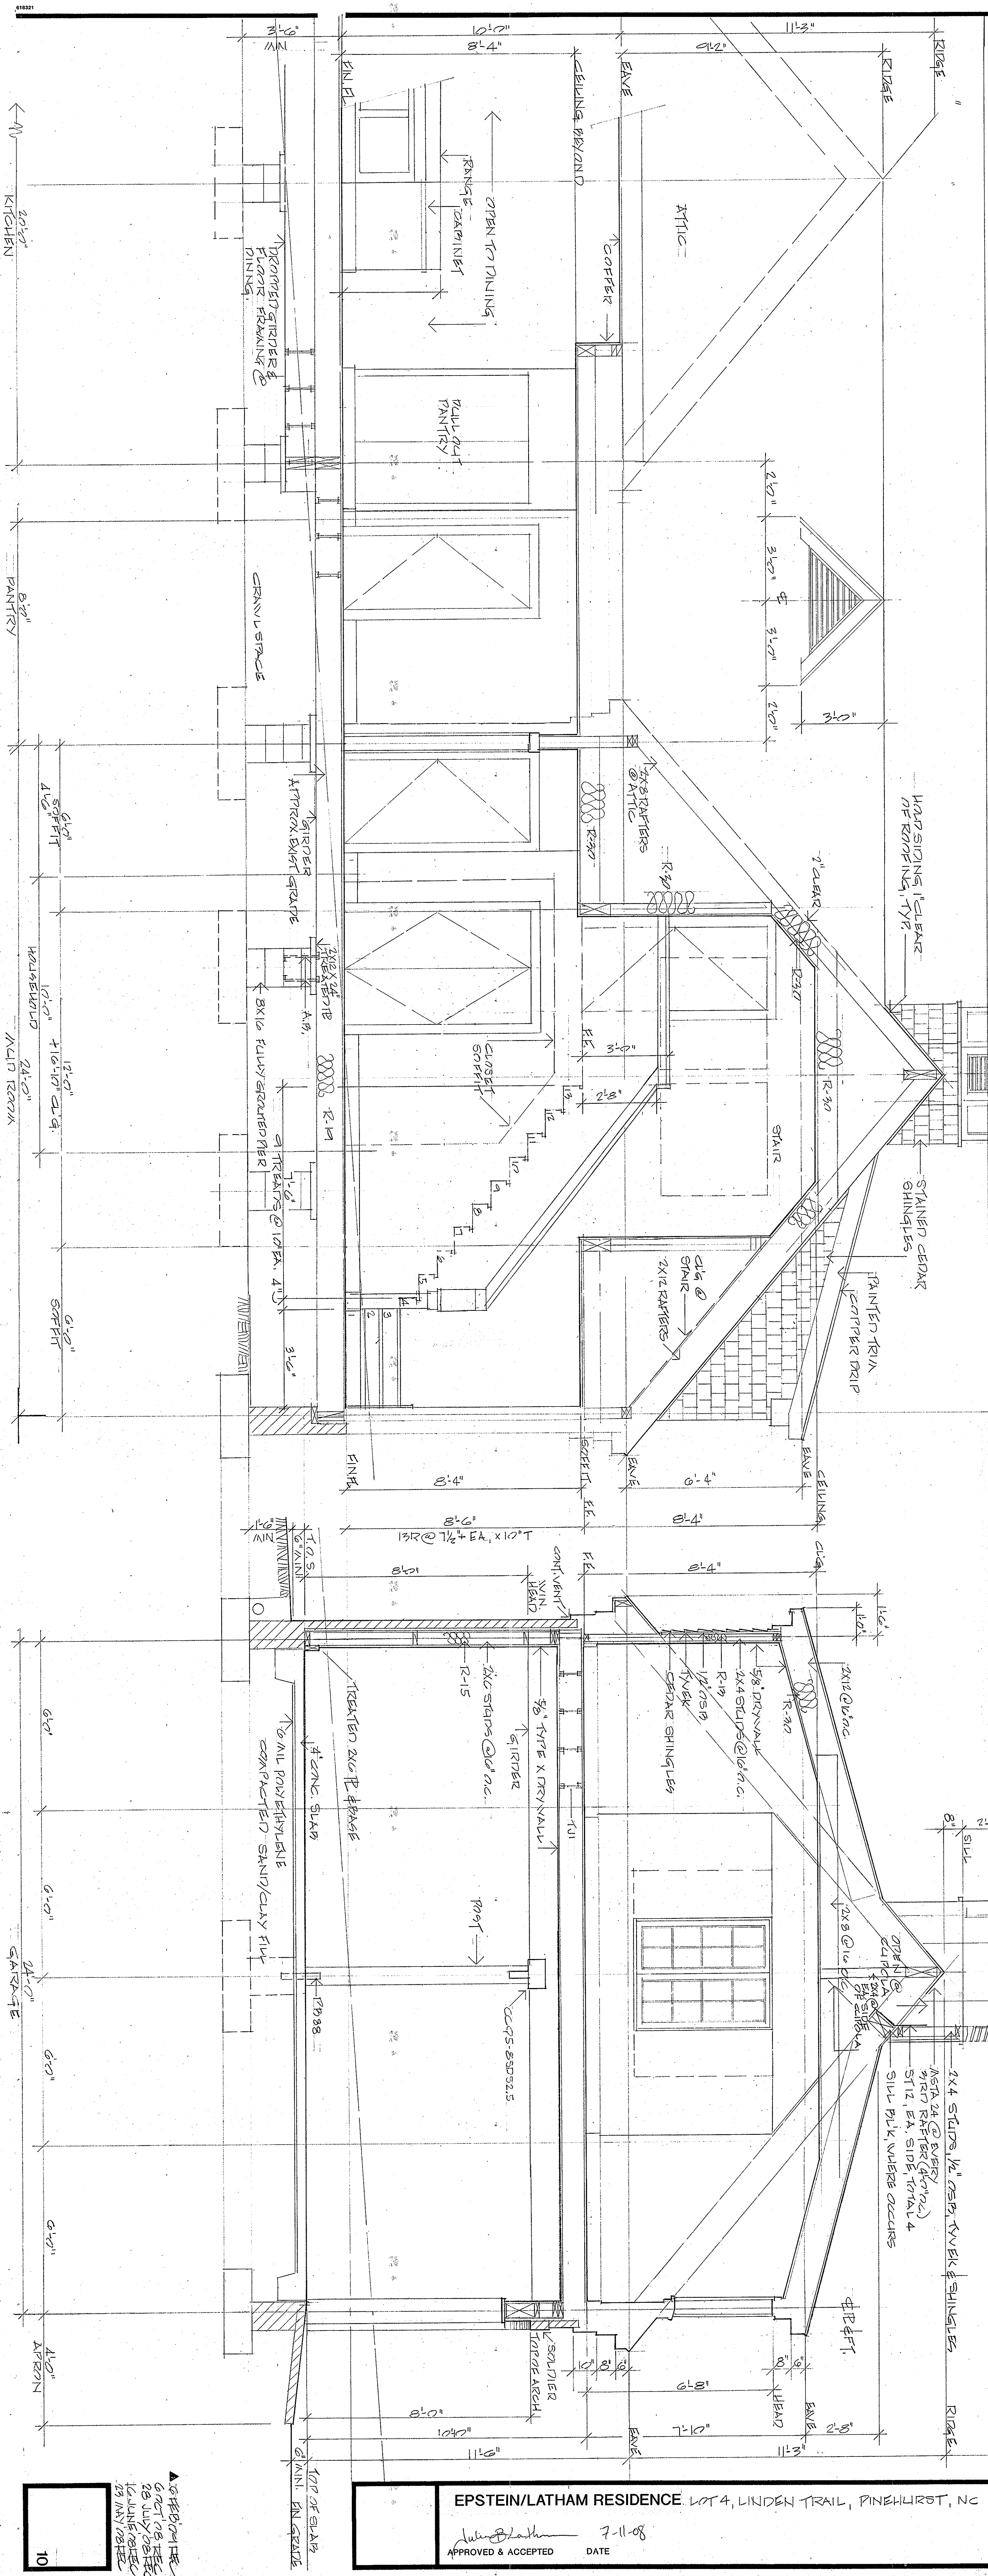




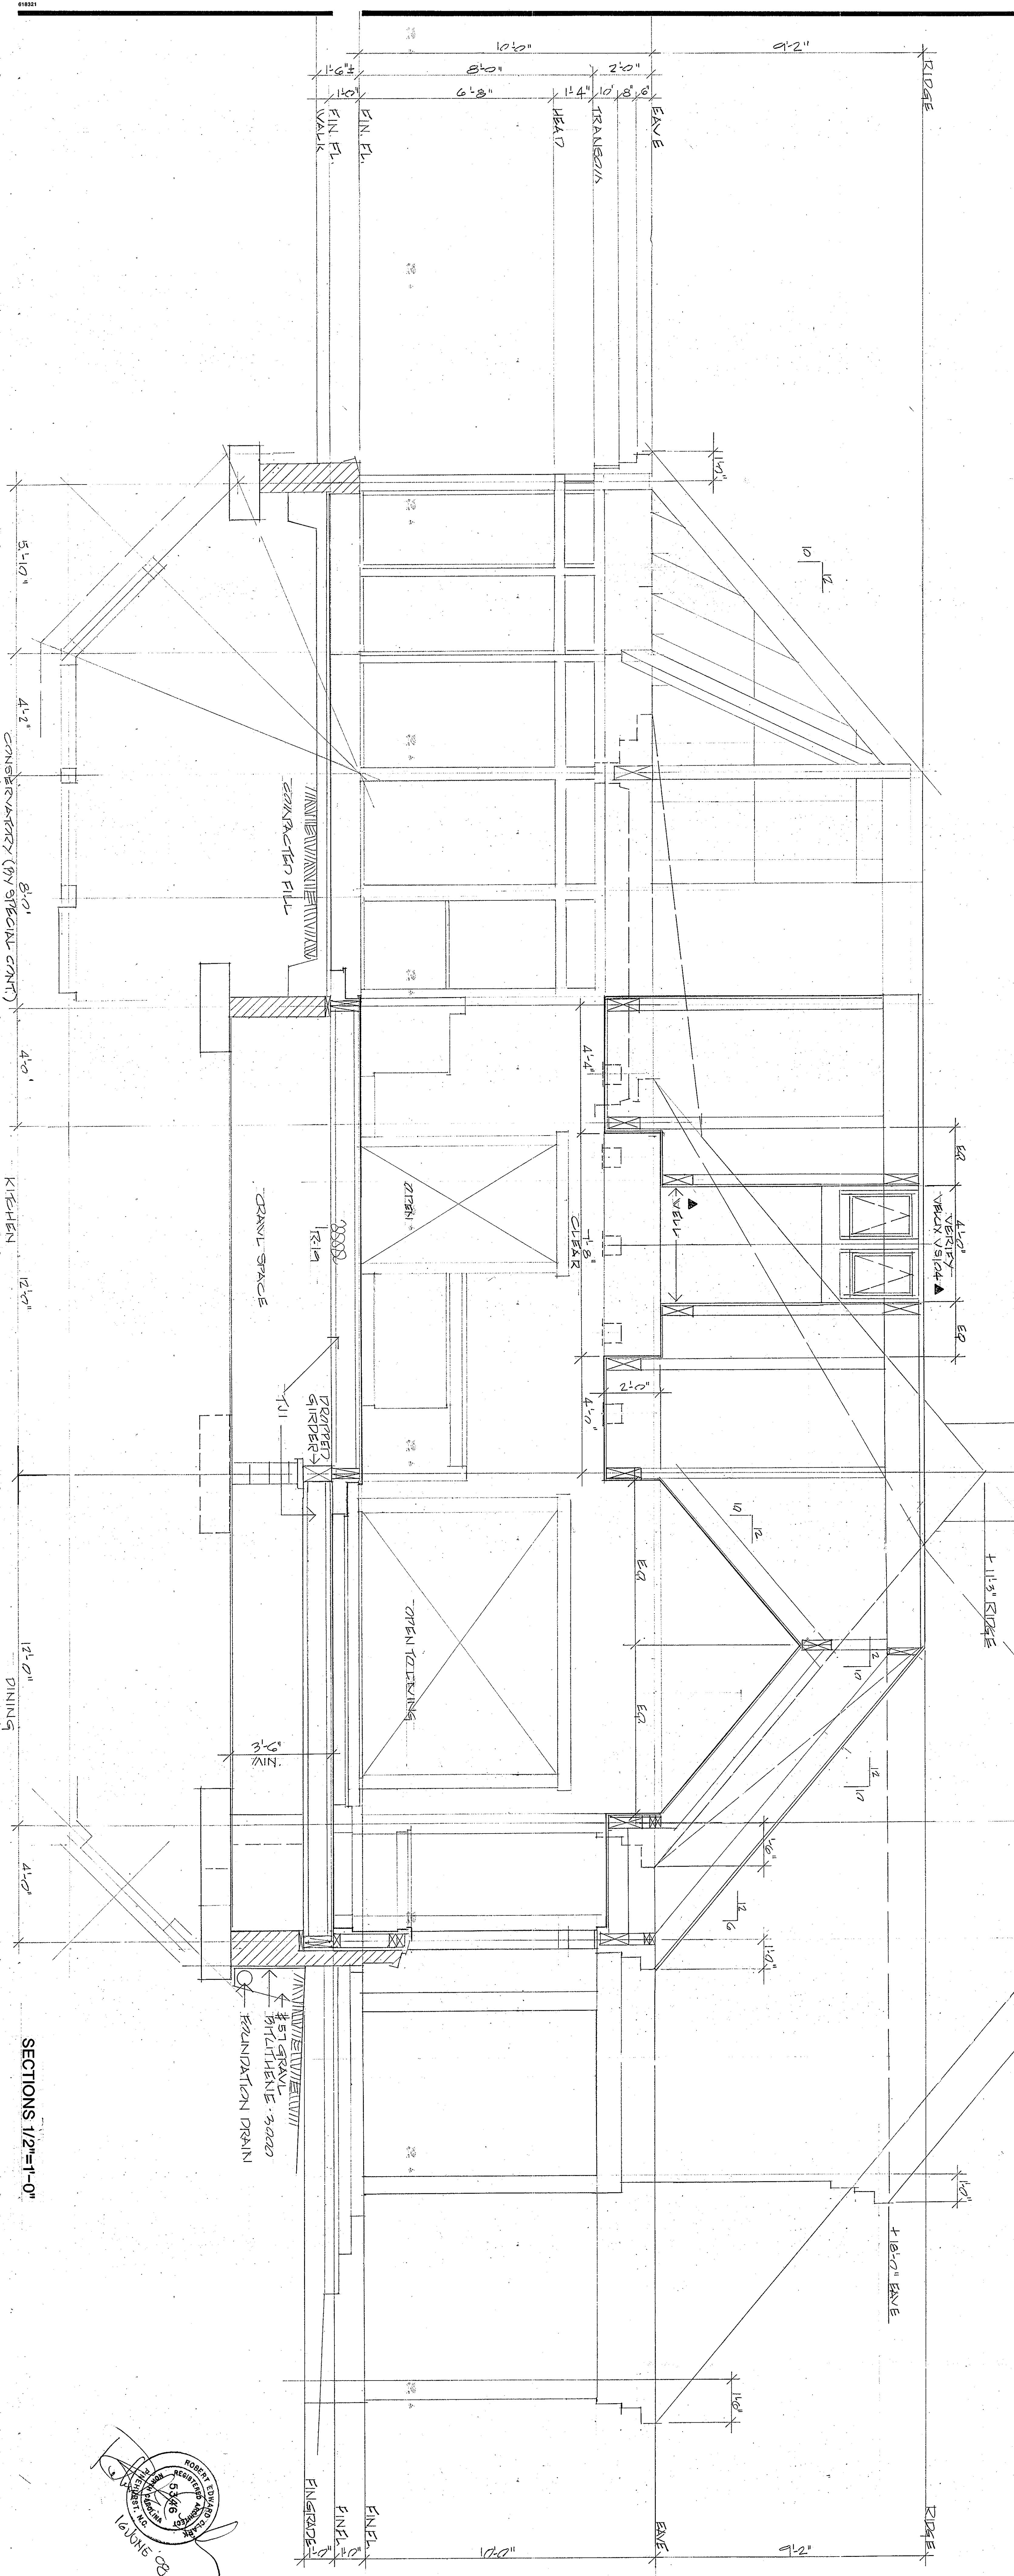

SECTIONS 1/2"=1'-0"

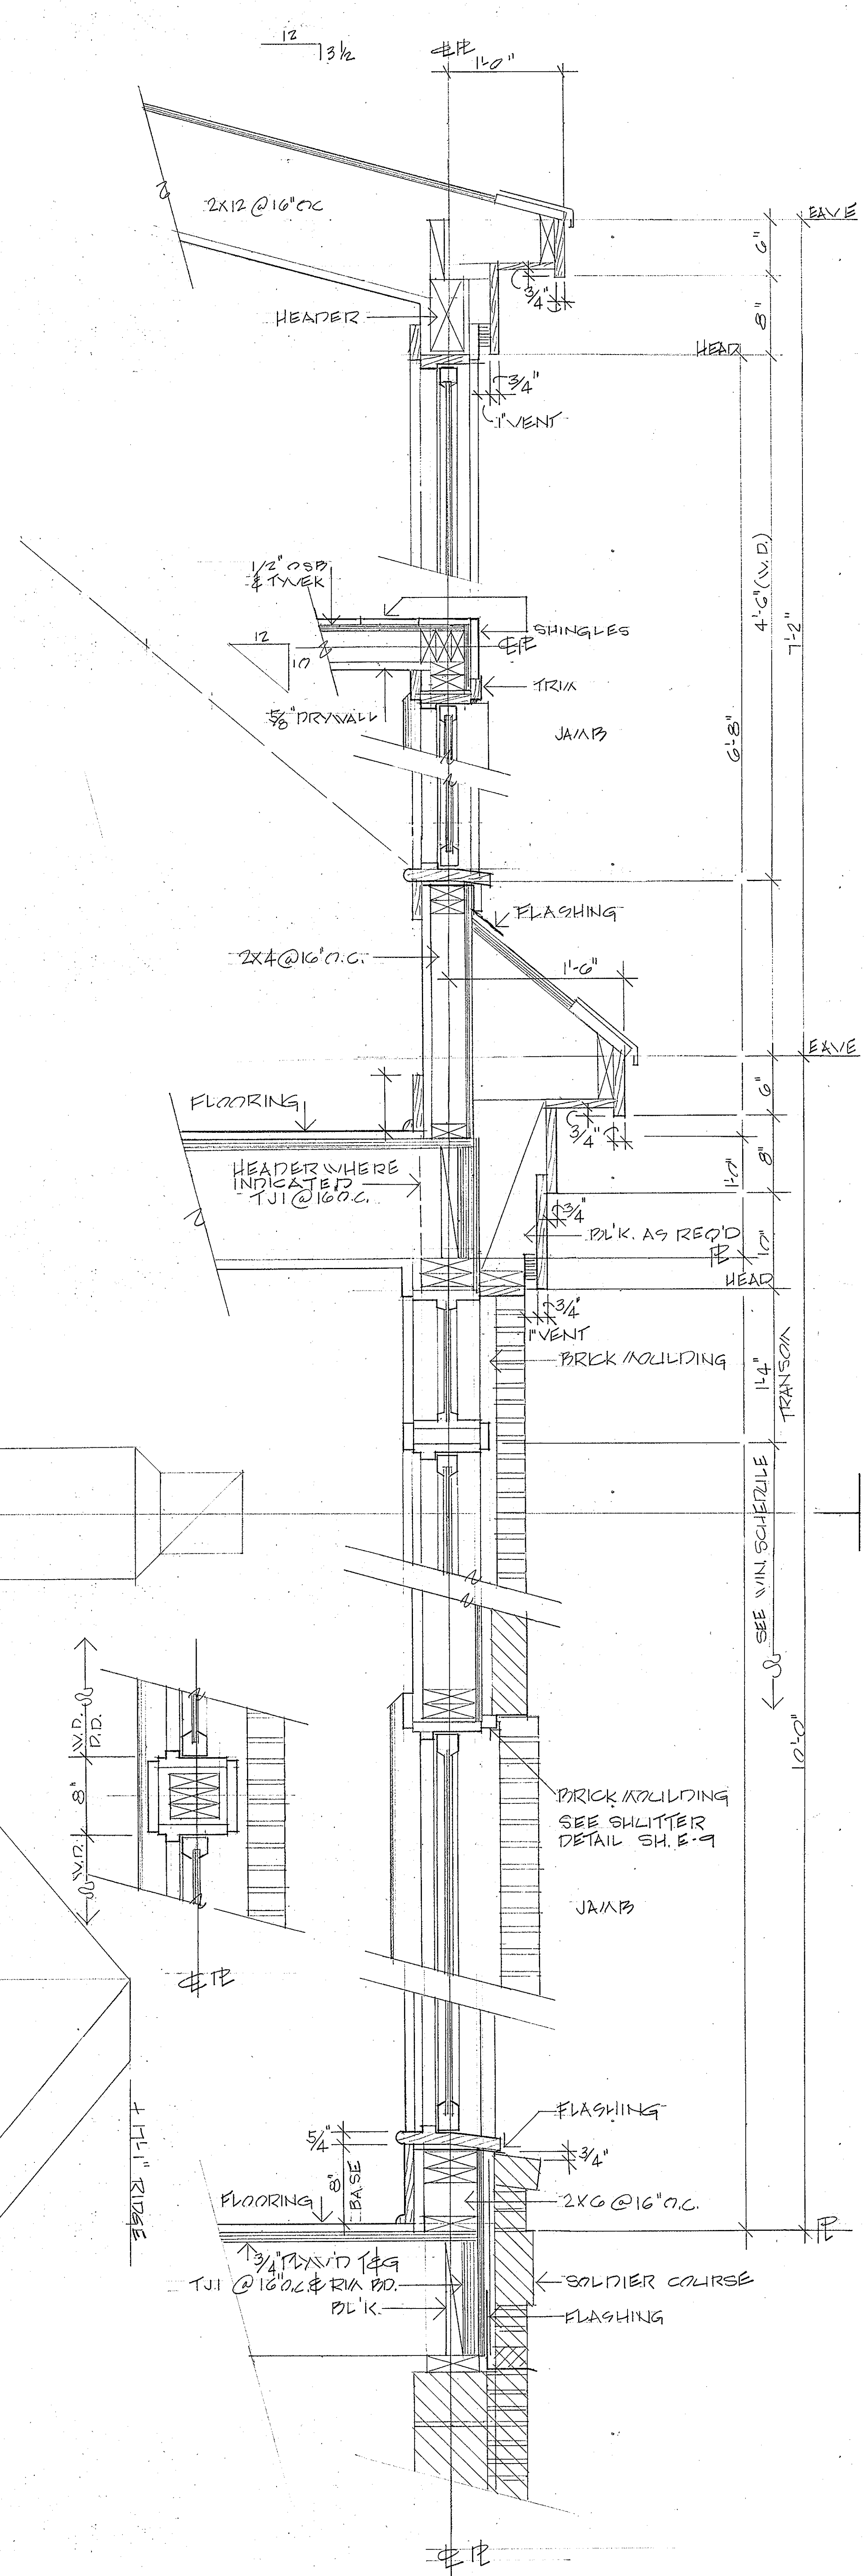


DETAIL SECTION 11/2"=1'-0"


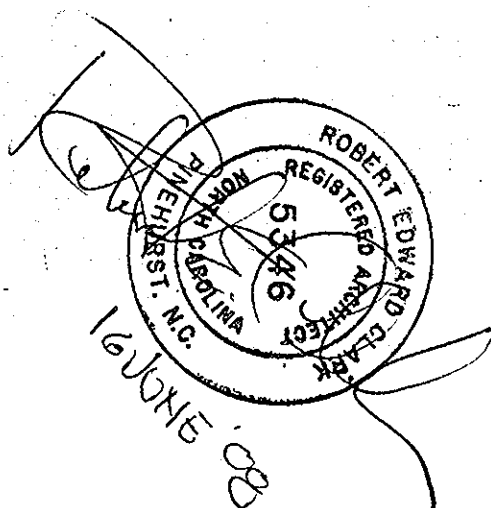


THE ARCHITECT RETAINS THE RIGHT OF AUTHORSHIP FOR IDEAS EXPRESSED AS HIS WORK AND AS SUCH ALL DRAWINGS AND SPECIFICATIONS REMAIN THE PROPERTY OF THE ARCHITECT WHETHER THE PROJECT FOR WHICH THEY ARE INTENDED IS EXECUTED OR NOT AND MAY NOT BE USED ON OTHER PROJECTS OR EXTENSIONS OF THIS PROJECT EXCEPT BY AGREEMENT WITH THE ARCHITECT.



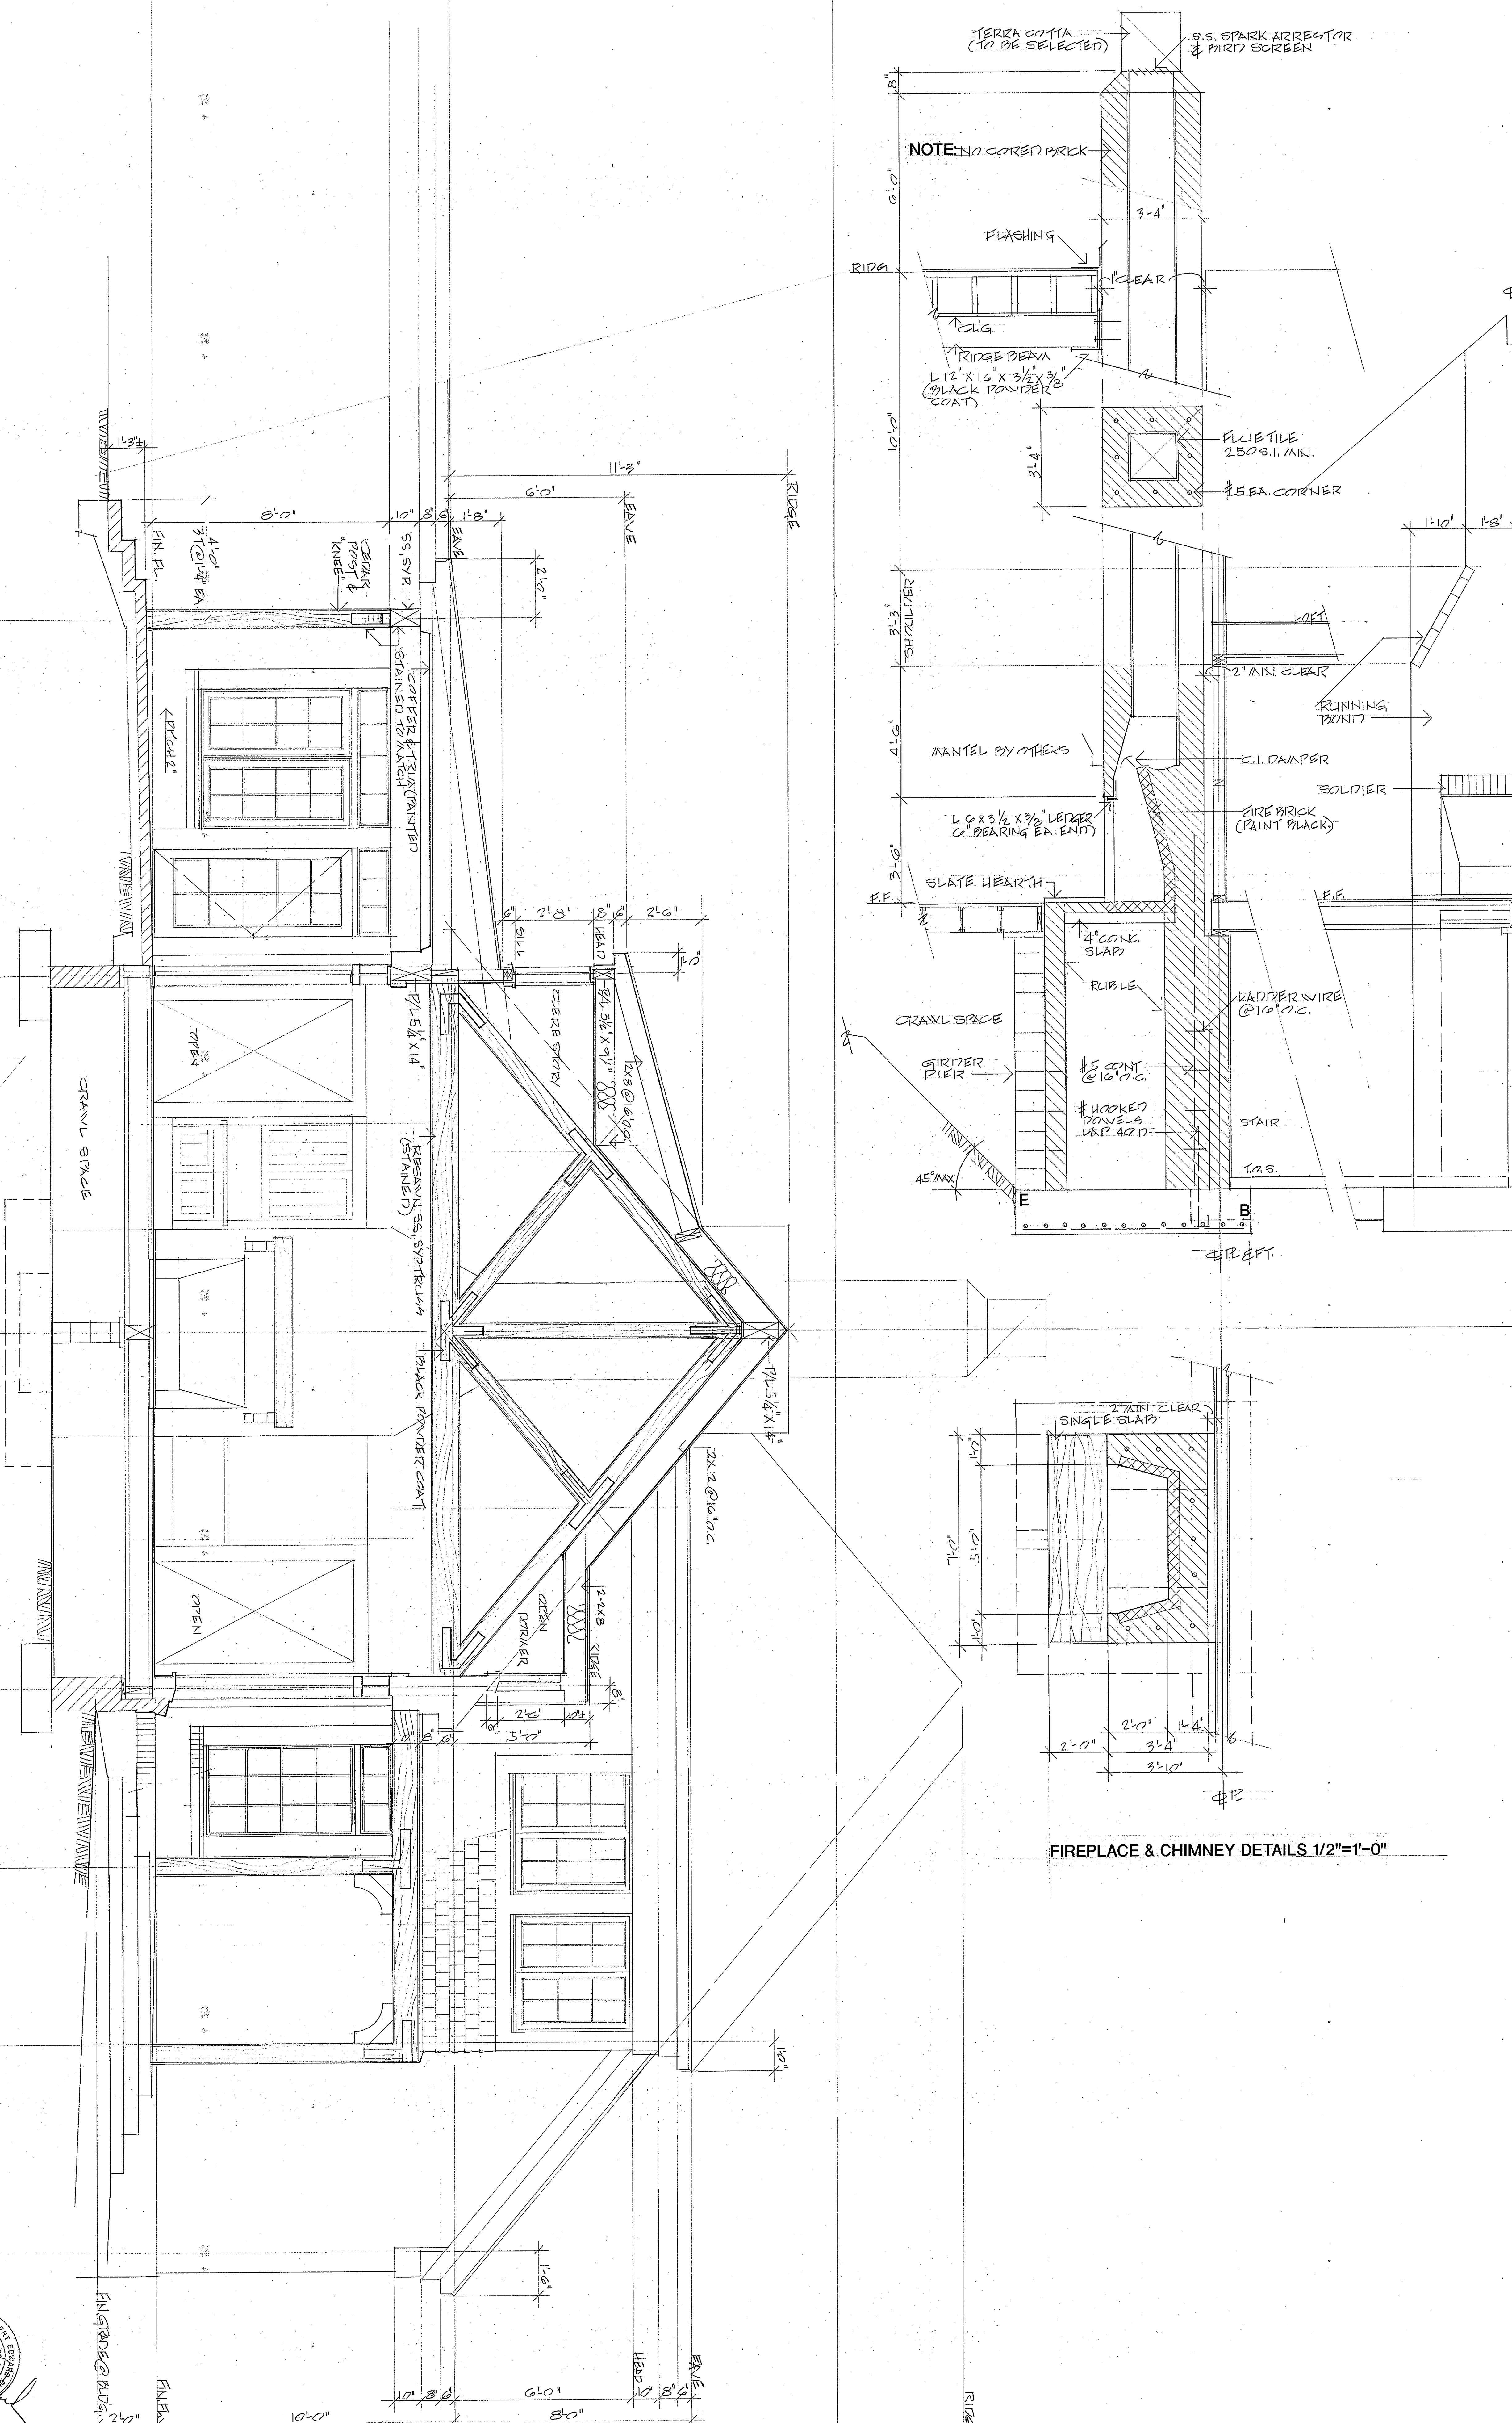



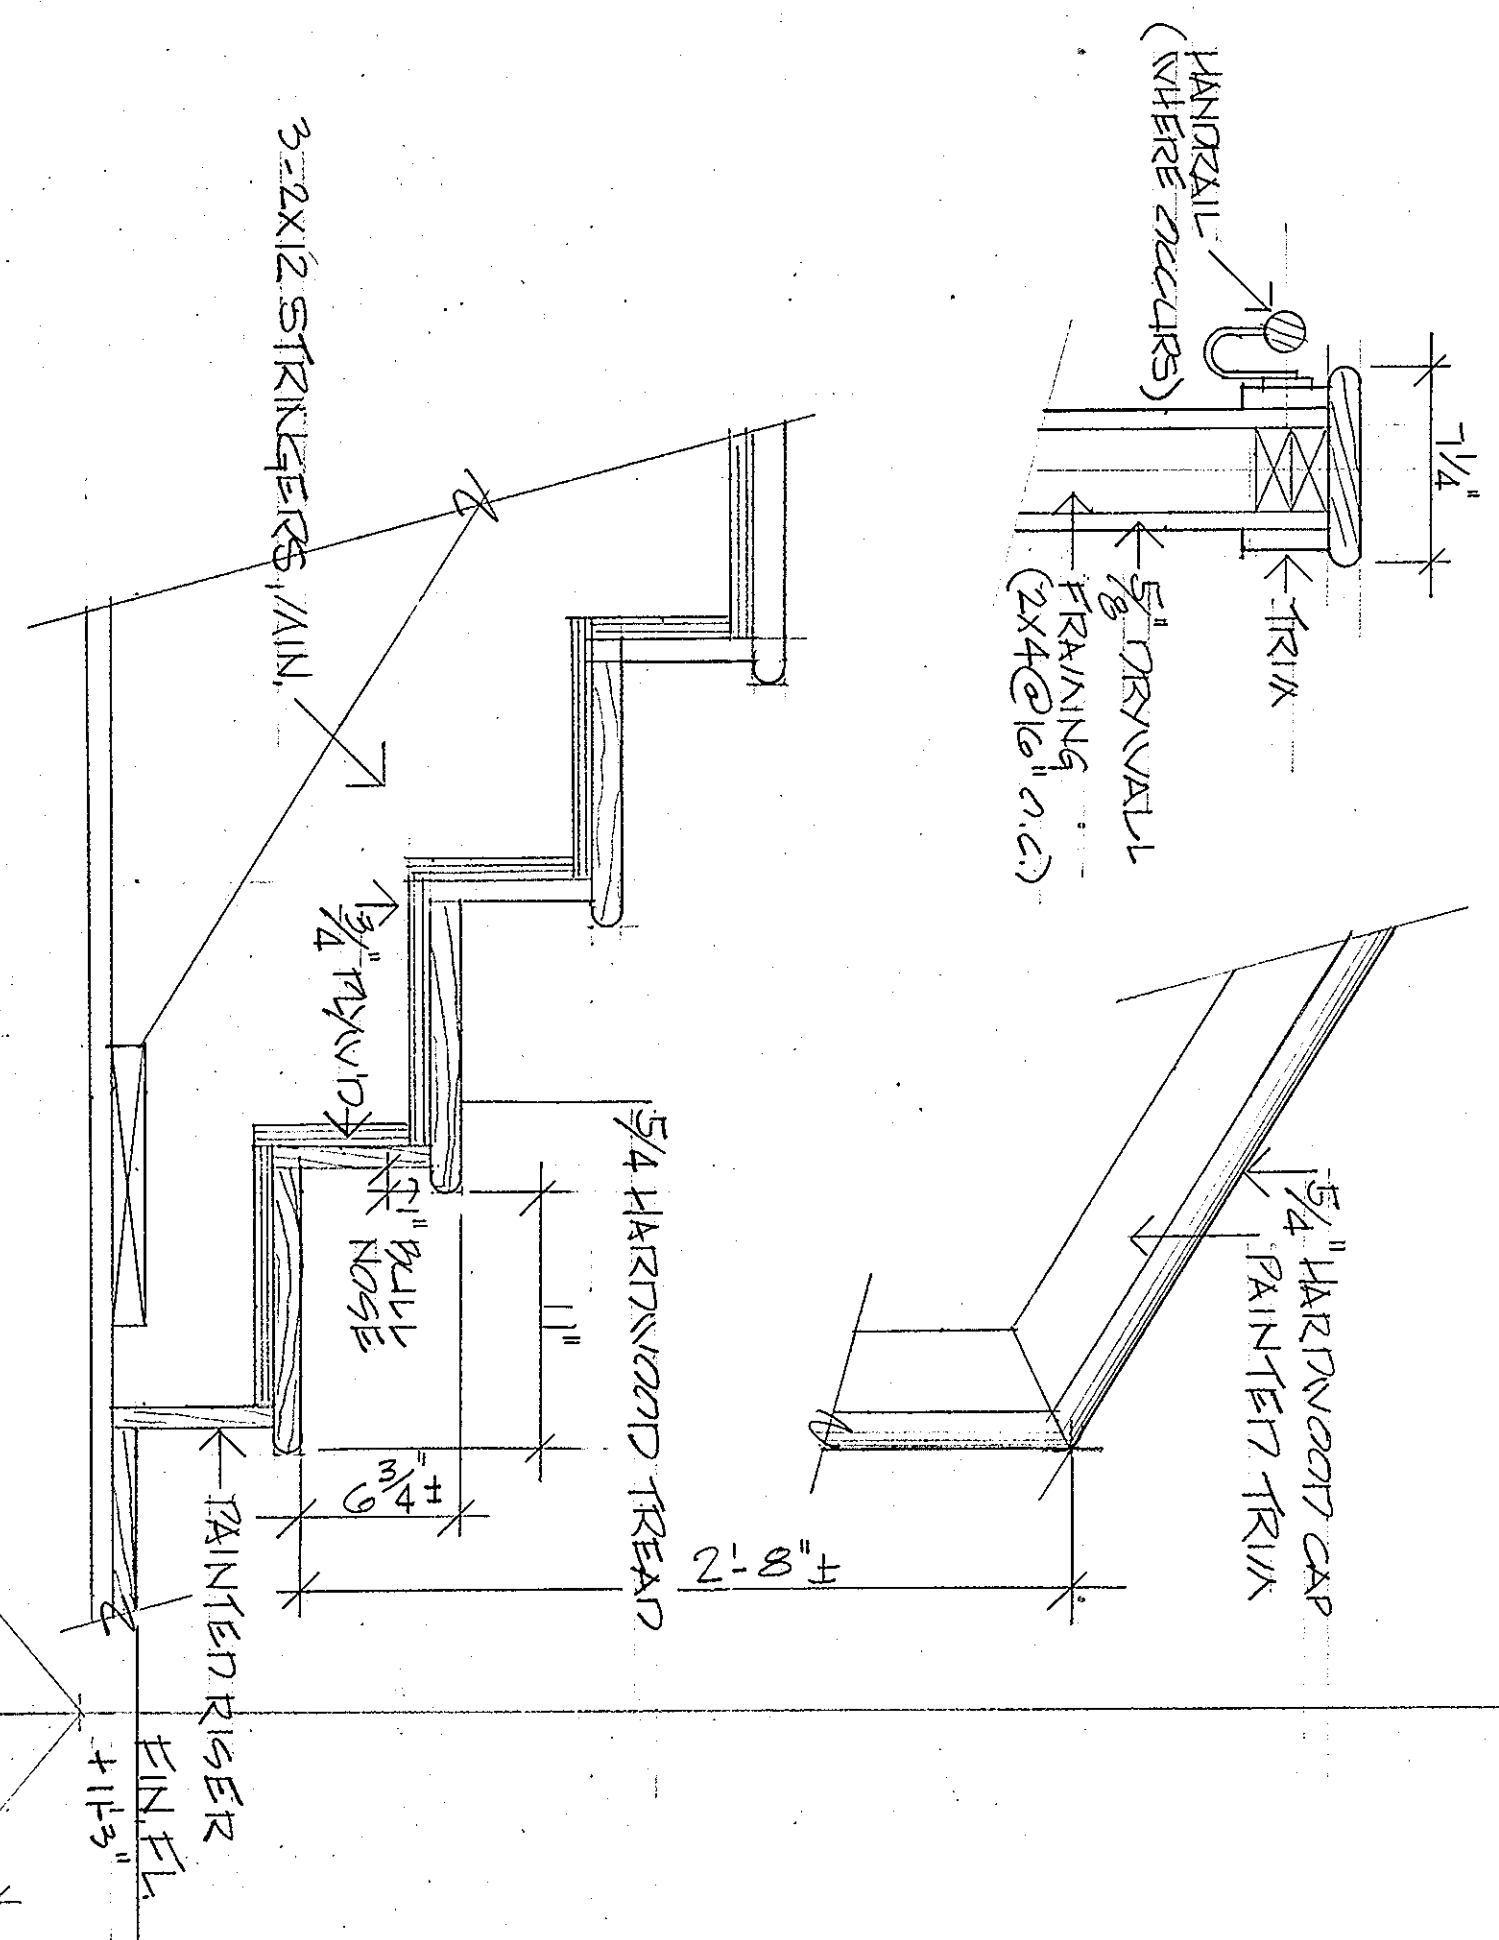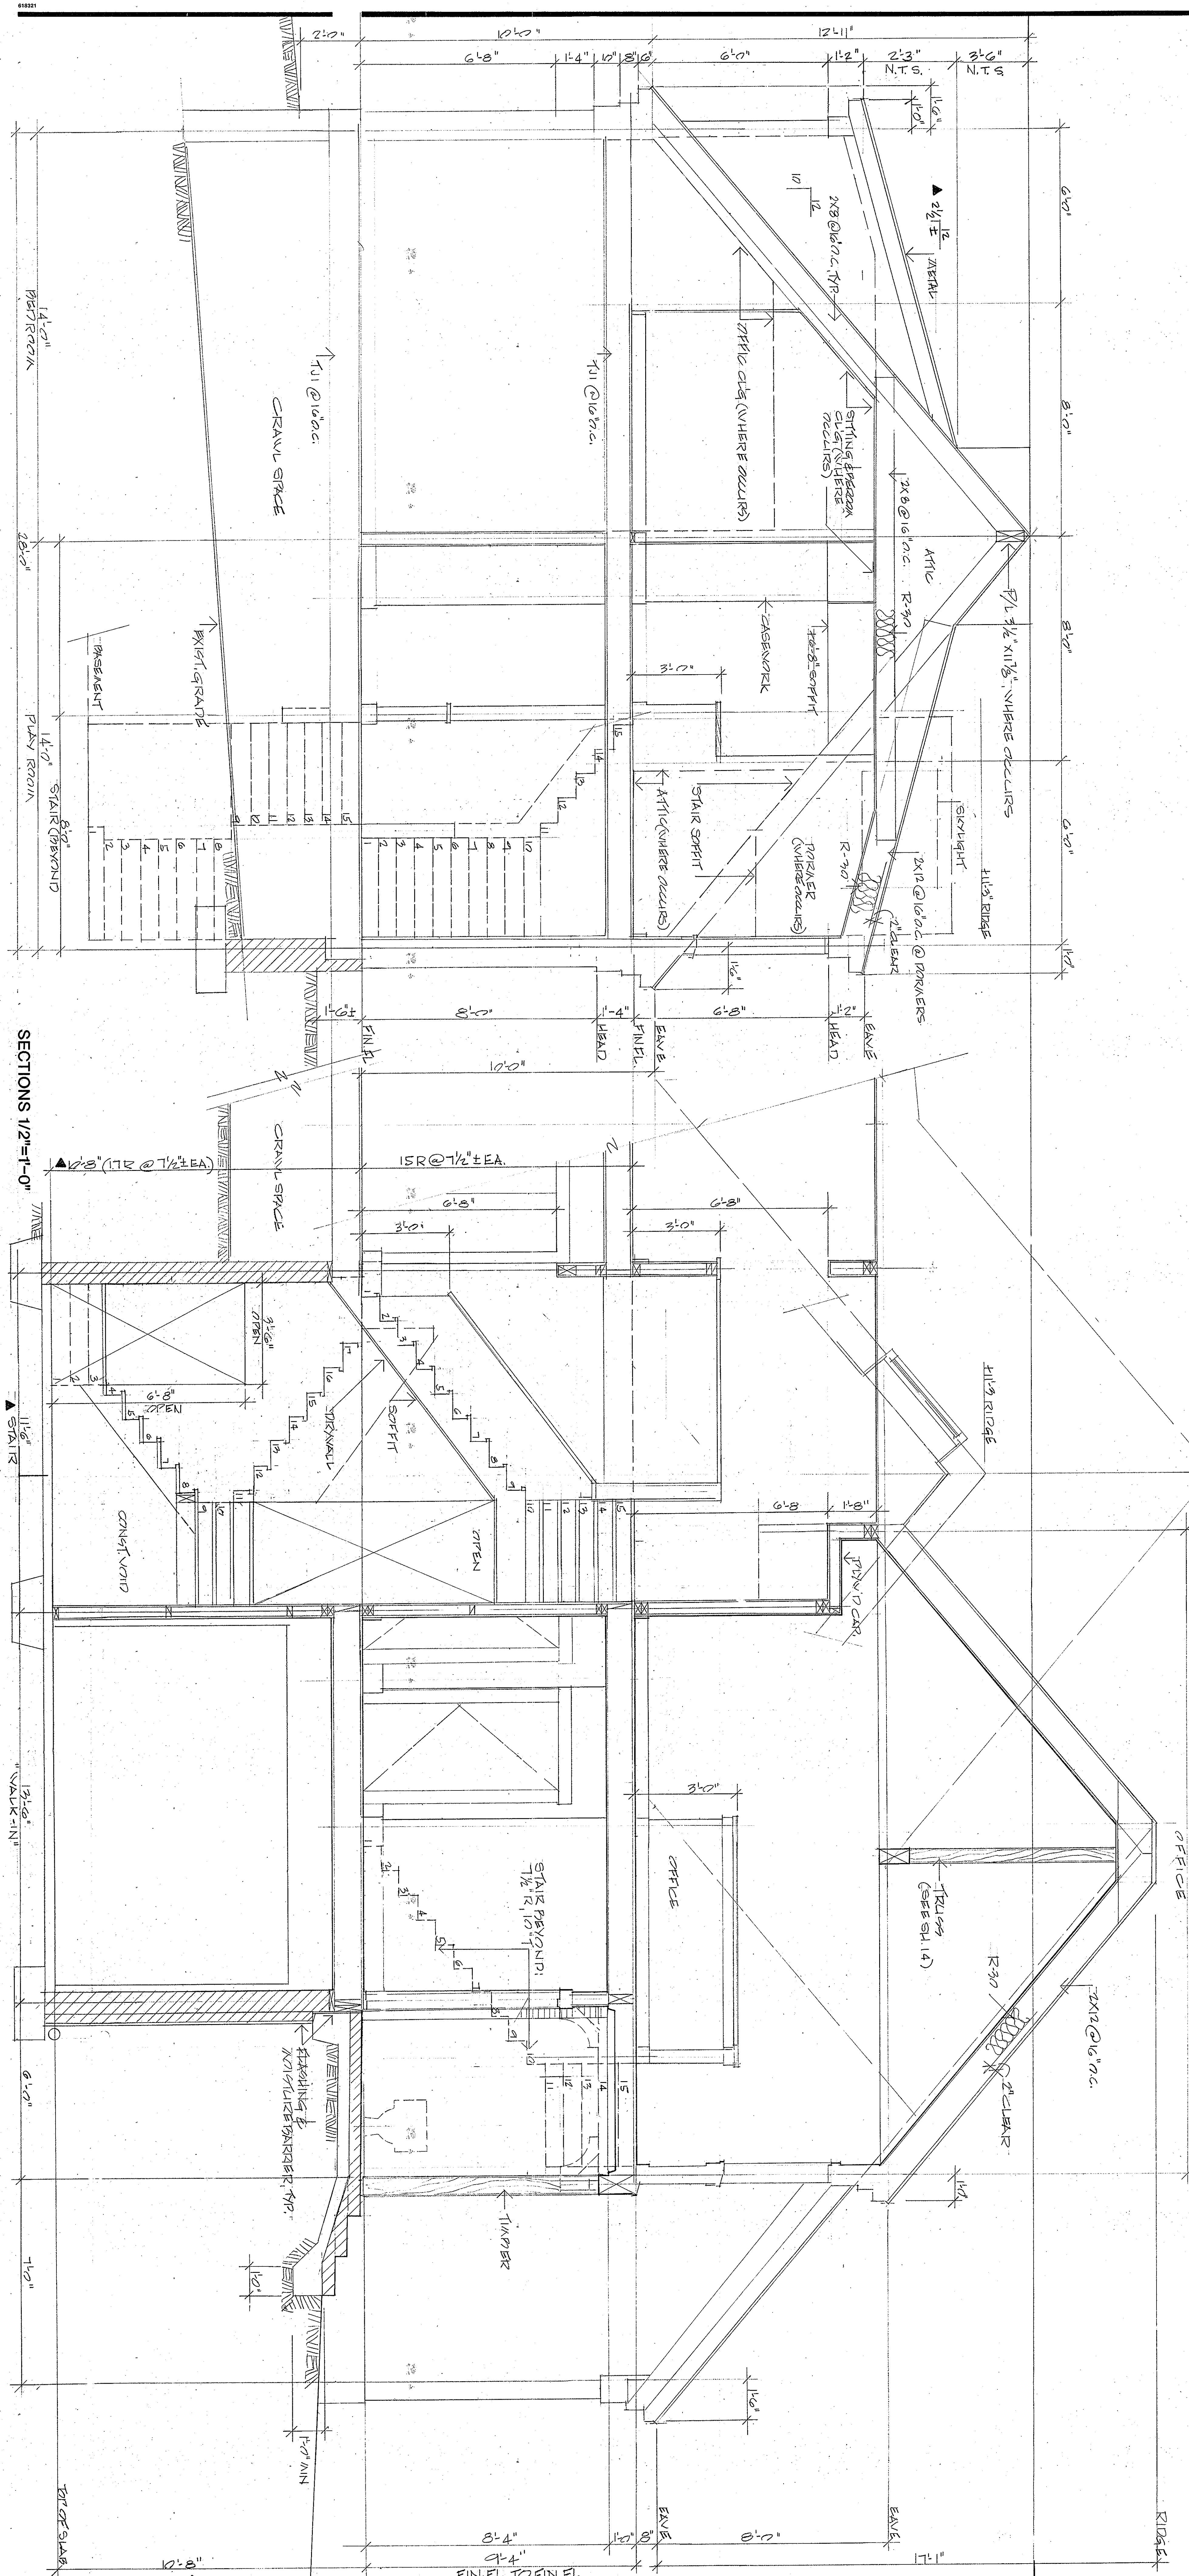



13

EPSTEIN/LATHAM RESIDENCE LOT 4 LINDEN TRAIL, PINEHURST, NC

THE ARCHITECT RETAINS THE RIGHT OF AUTHORSHIP FOR IDEAS EXPRESSED AS HIS WORK AND AS SUCH ALL DRAWINGS AND SPECIFICATIONS REMAIN THE PROPERTY OF THE ARCHITECT WHETHER THE PROJECT FOR WHICH THEY ARE INTENDED IS EXECUTED OR NOT AND MAY NOT BE USED ON OTHER PROJECTS OR EXTENSIONS OF THIS PROJECT EXCEPT BY AGREEMENT WITH THE ARCHITECT.

ROBERT E. CLARK AIA ARCHITECT  
910 295 4683 FAX 910 295 5684  
65 COMMUNITY ROAD  
PINEHURST NORTH CAROLINA 28370



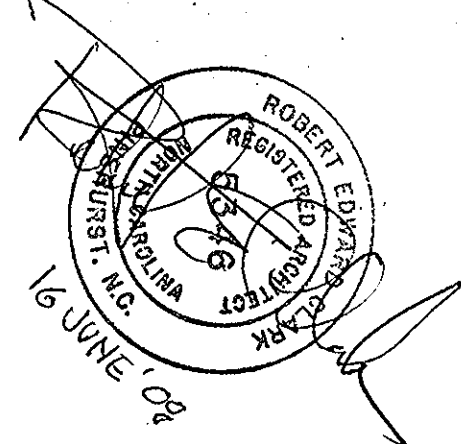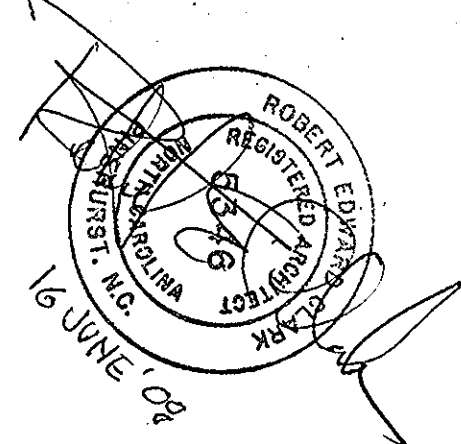

Julia B. Latham 7-11-08

APPROVED & ACCEPTED      DATE

## REVISIONS


**910 295 4683** FAX **910 295 5684**

65 COMMUNITY ROAD  
PINEHURST NORTH CAROLINA 28370

**FAX: 910 295 5684**

P O BOX 205



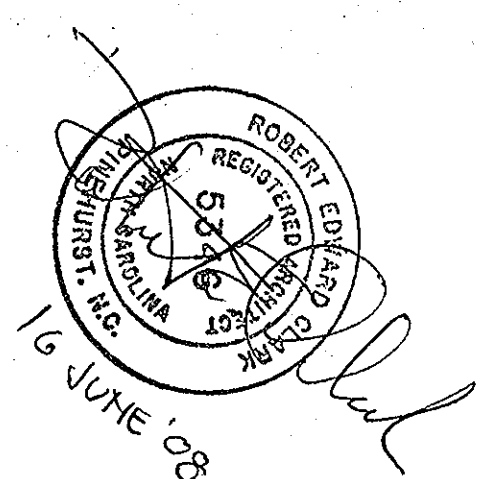


REFLECTED PLAN 1/4"=1'-0"



BASEMENT ▲ REFER TO SH, R-1

LOFTS

REFLECTED PLANS 1/4"=1'-0"

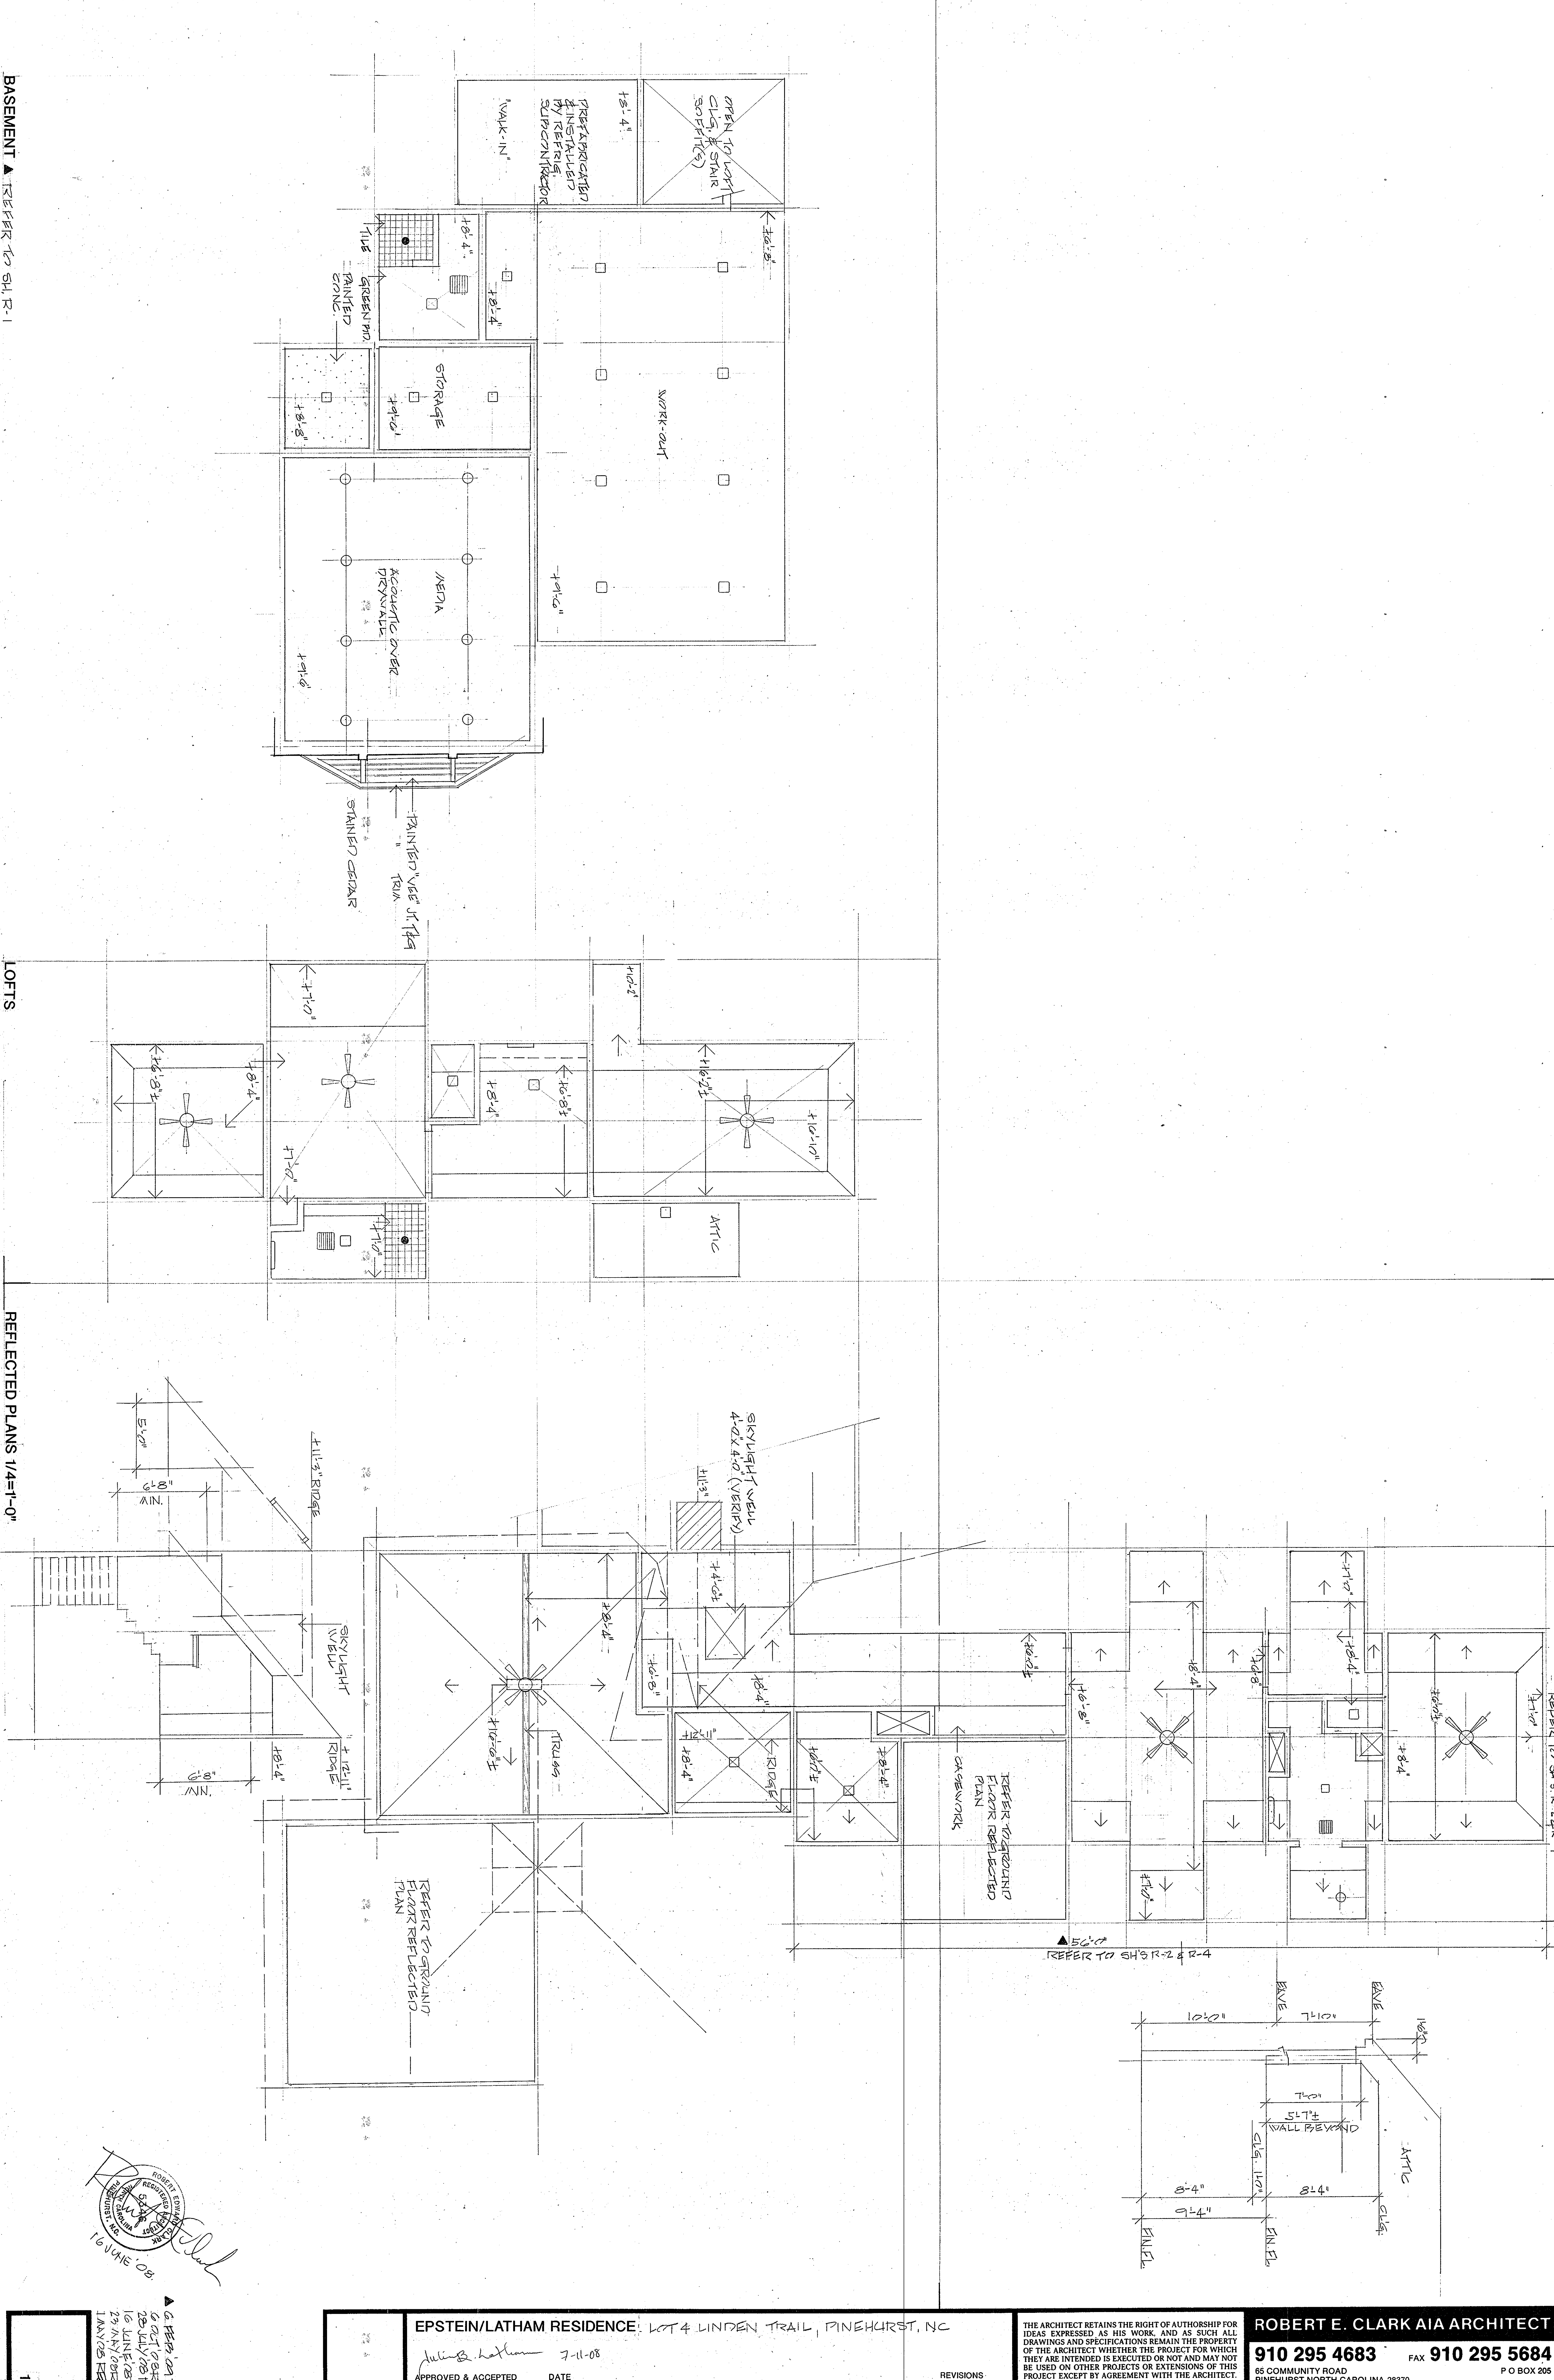

16

EPSTEIN/LATHAM RESIDENCE: LOT 4 LINDEN TRAIL, PINEHURST, NC

7-11-08

APPROVED & ACCEPTED DATE


THE ARCHITECT RETAINS THE RIGHT OF AUTHORSHIP FOR IDEAS EXPRESSED AS HIS WORK AND AS SUCH ALL DRAWINGS AND SPECIFICATIONS REMAIN THE PROPERTY OF THE ARCHITECT WHETHER THE PROJECT FOR WHICH THEY ARE INTENDED IS EXECUTED OR NOT AND MAY NOT BE USED ON OTHER PROJECTS OR EXTENSIONS OF THIS PROJECT EXCEPT BY AGREEMENT WITH THE ARCHITECT.

ROBERT E. CLARK AIA ARCHITECT

910 295 4683 FAX 910 295 5684


85 COMMUNITY ROAD PINEHURST NORTH CAROLINA 28370



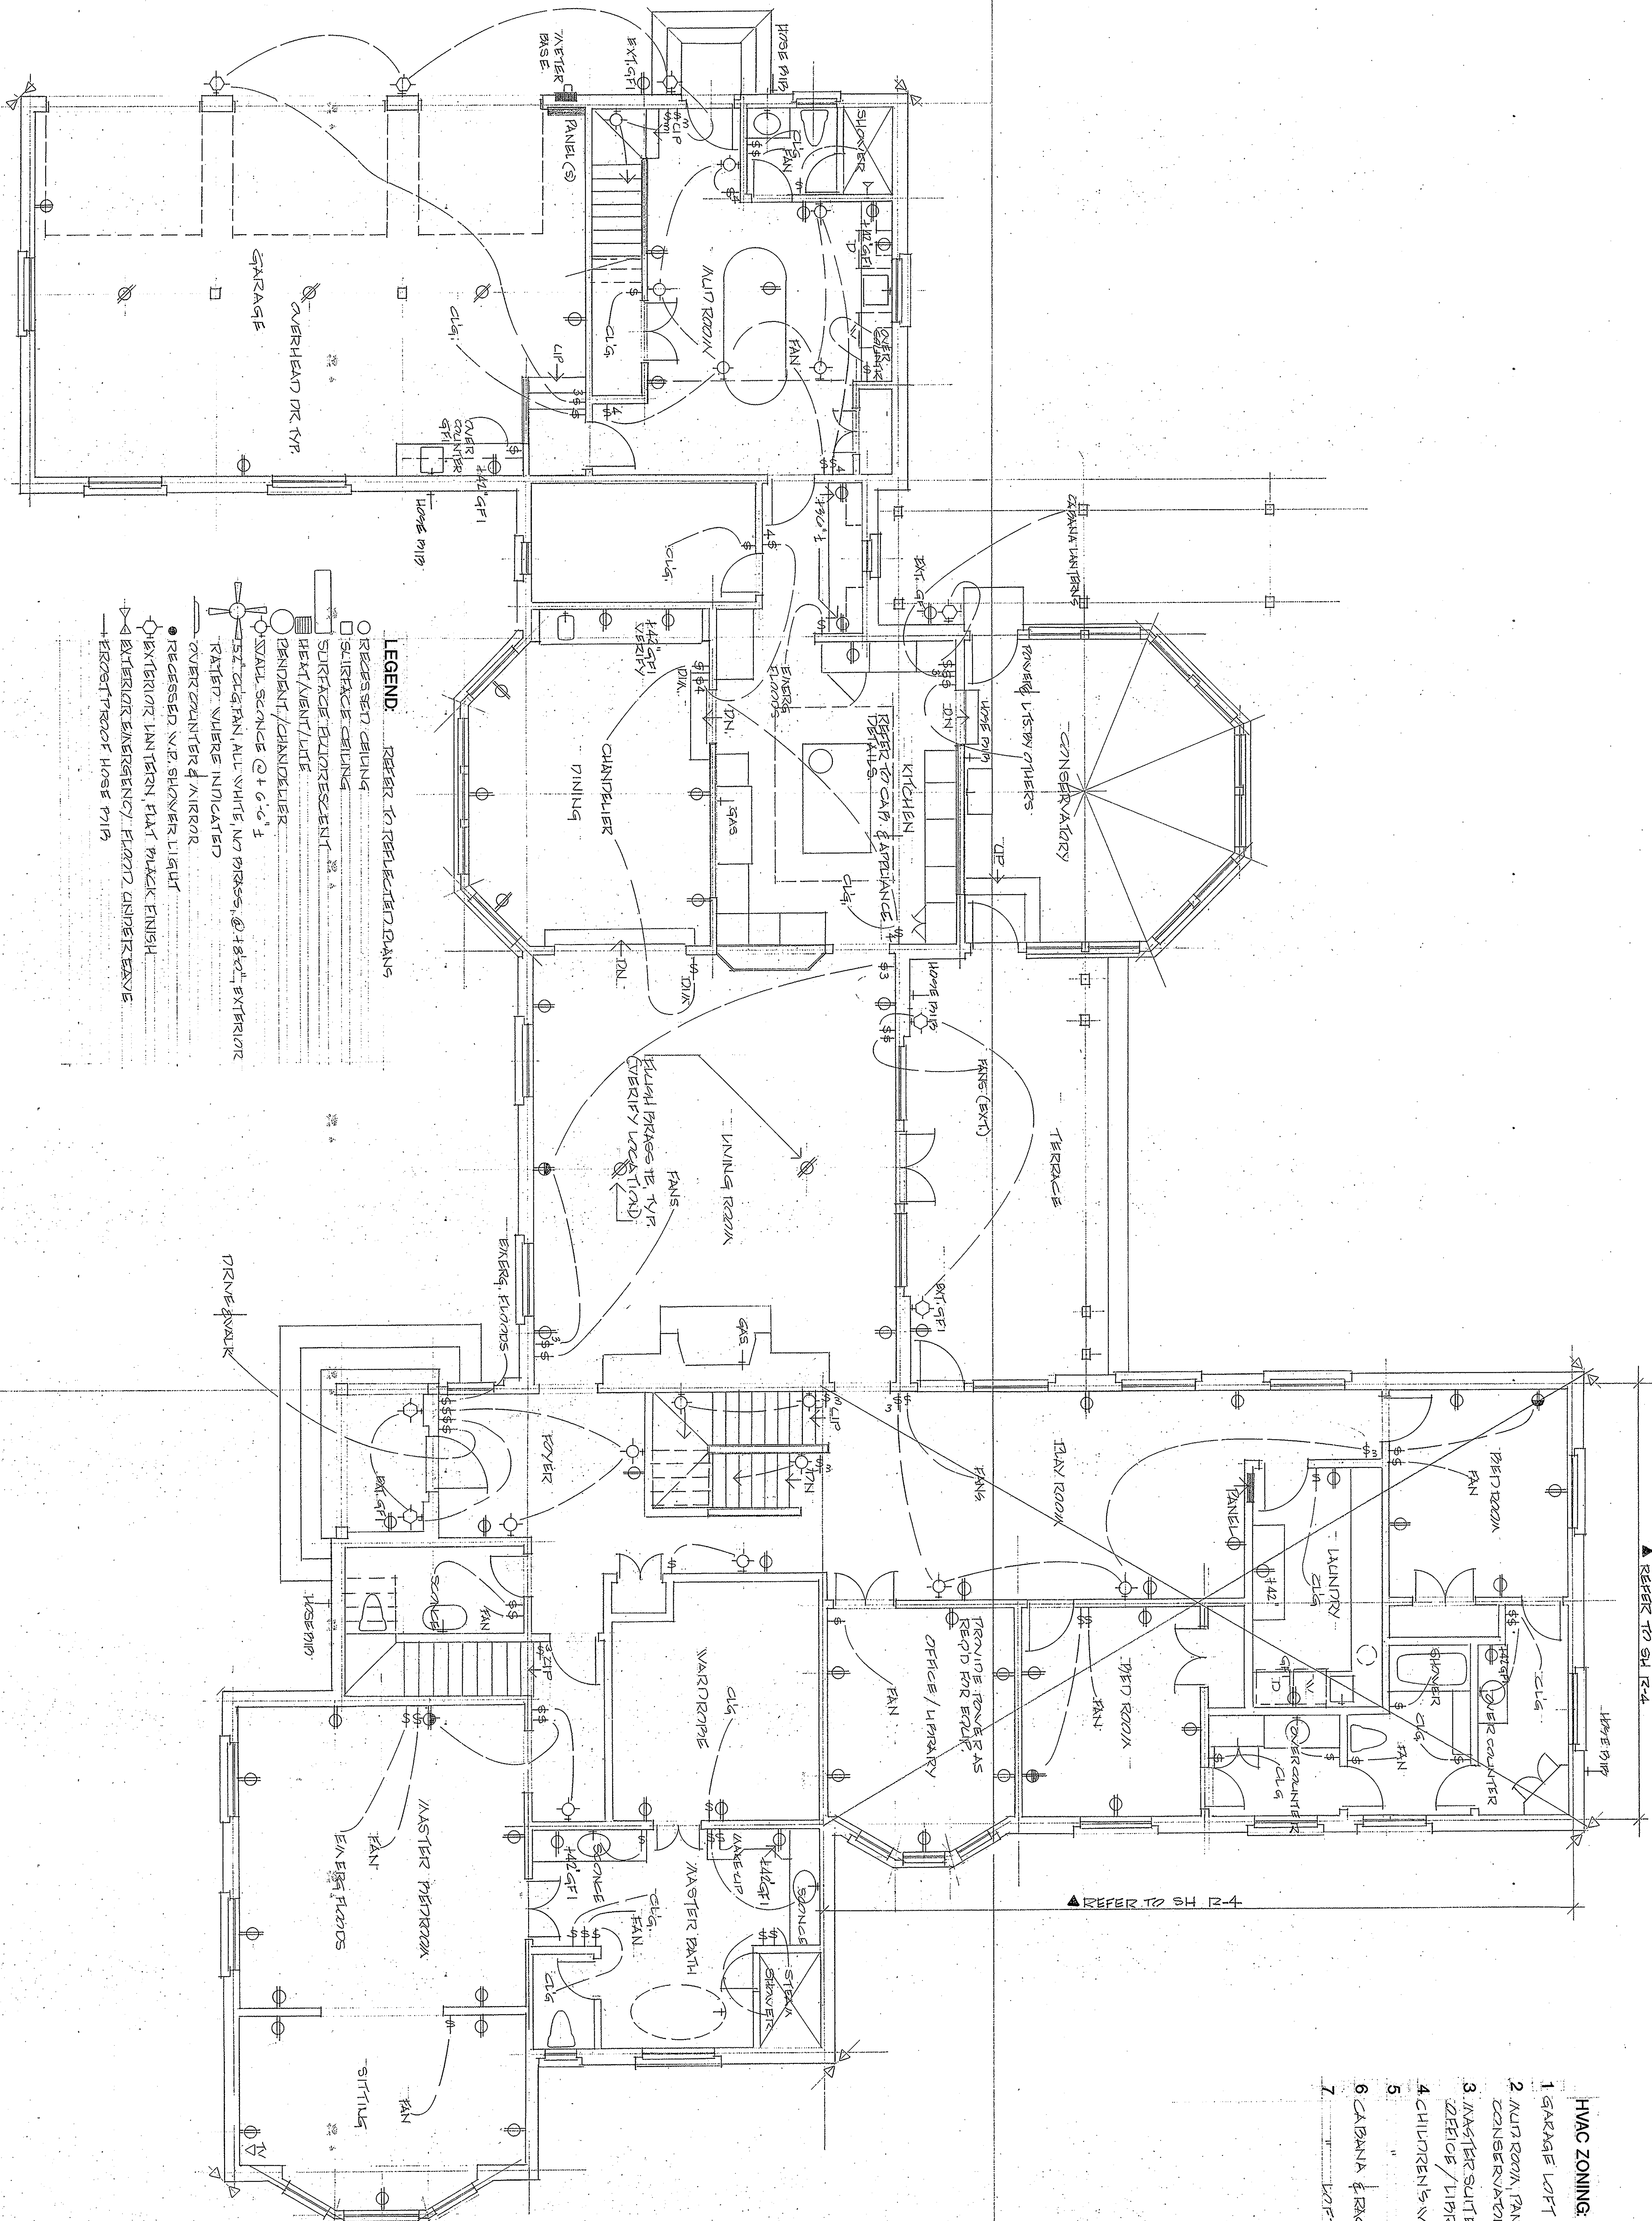

GROUND FLOOR POWER PLAN 1/4"=1'-0"

- HVAC ZONING:**
- 1 GARAGE LOFT
  - 2 MAIN ROOM, PANTRY, KITCHEN, DINING, CONSERVATORY, LIVING & FOYER
  - 3 MASTER SUITE, MASTER'S OFFICE & ZEEBOS / LIBRARY
  - 4 CHILDREN'S WING & BASEMENT
  - 5 " LOFT
  - 6 CABBAN & RECQUITBALL COURT
  - 7 " LOFT

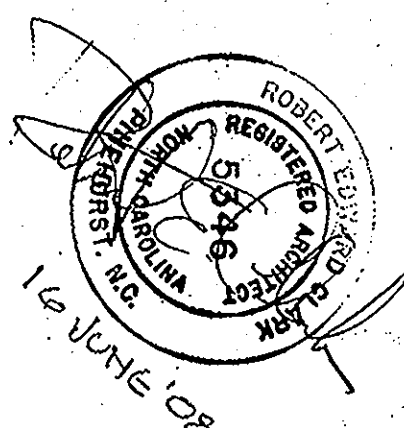

EPSTEIN/LATHAM RESIDENCE 1274 LINDEN TRAIL, PINEHURST, NC

APPROVED & ACCEPTED DATE 7-1-08

REVISIONS



THE ARCHITECT RETAINS THE RIGHT OF AUTHORSHIP FOR IDEAS EXPRESSED AS HIS WORK AND AS SUCH ALL DRAWINGS AND SPECIFICATIONS REMAIN THE PROPERTY OF THE ARCHITECT WHETHER THE PROJECT FOR WHICH THEY ARE INTENDED IS EXECUTED OR NOT AND MAY NOT BE USED ON OTHER PROJECTS OR EXTENSIONS OF THIS PROJECT EXCEPT BY AGREEMENT WITH THE ARCHITECT.

ROBERT E. CLARK AIA ARCHITECT

910 295 4683 FAX 910 295 5684  
65 COMMUNITY ROAD  
PINEHURST NORTH CAROLINA 28370  
P O BOX 205

6-18-07 07:15:00  
6-18-07 07:15:00  
28 JULY 08 08:00  
16 JULY 08 08:00



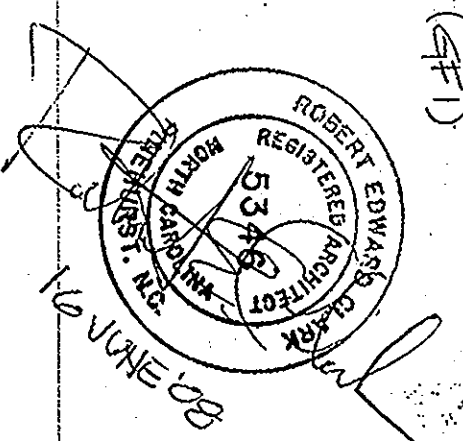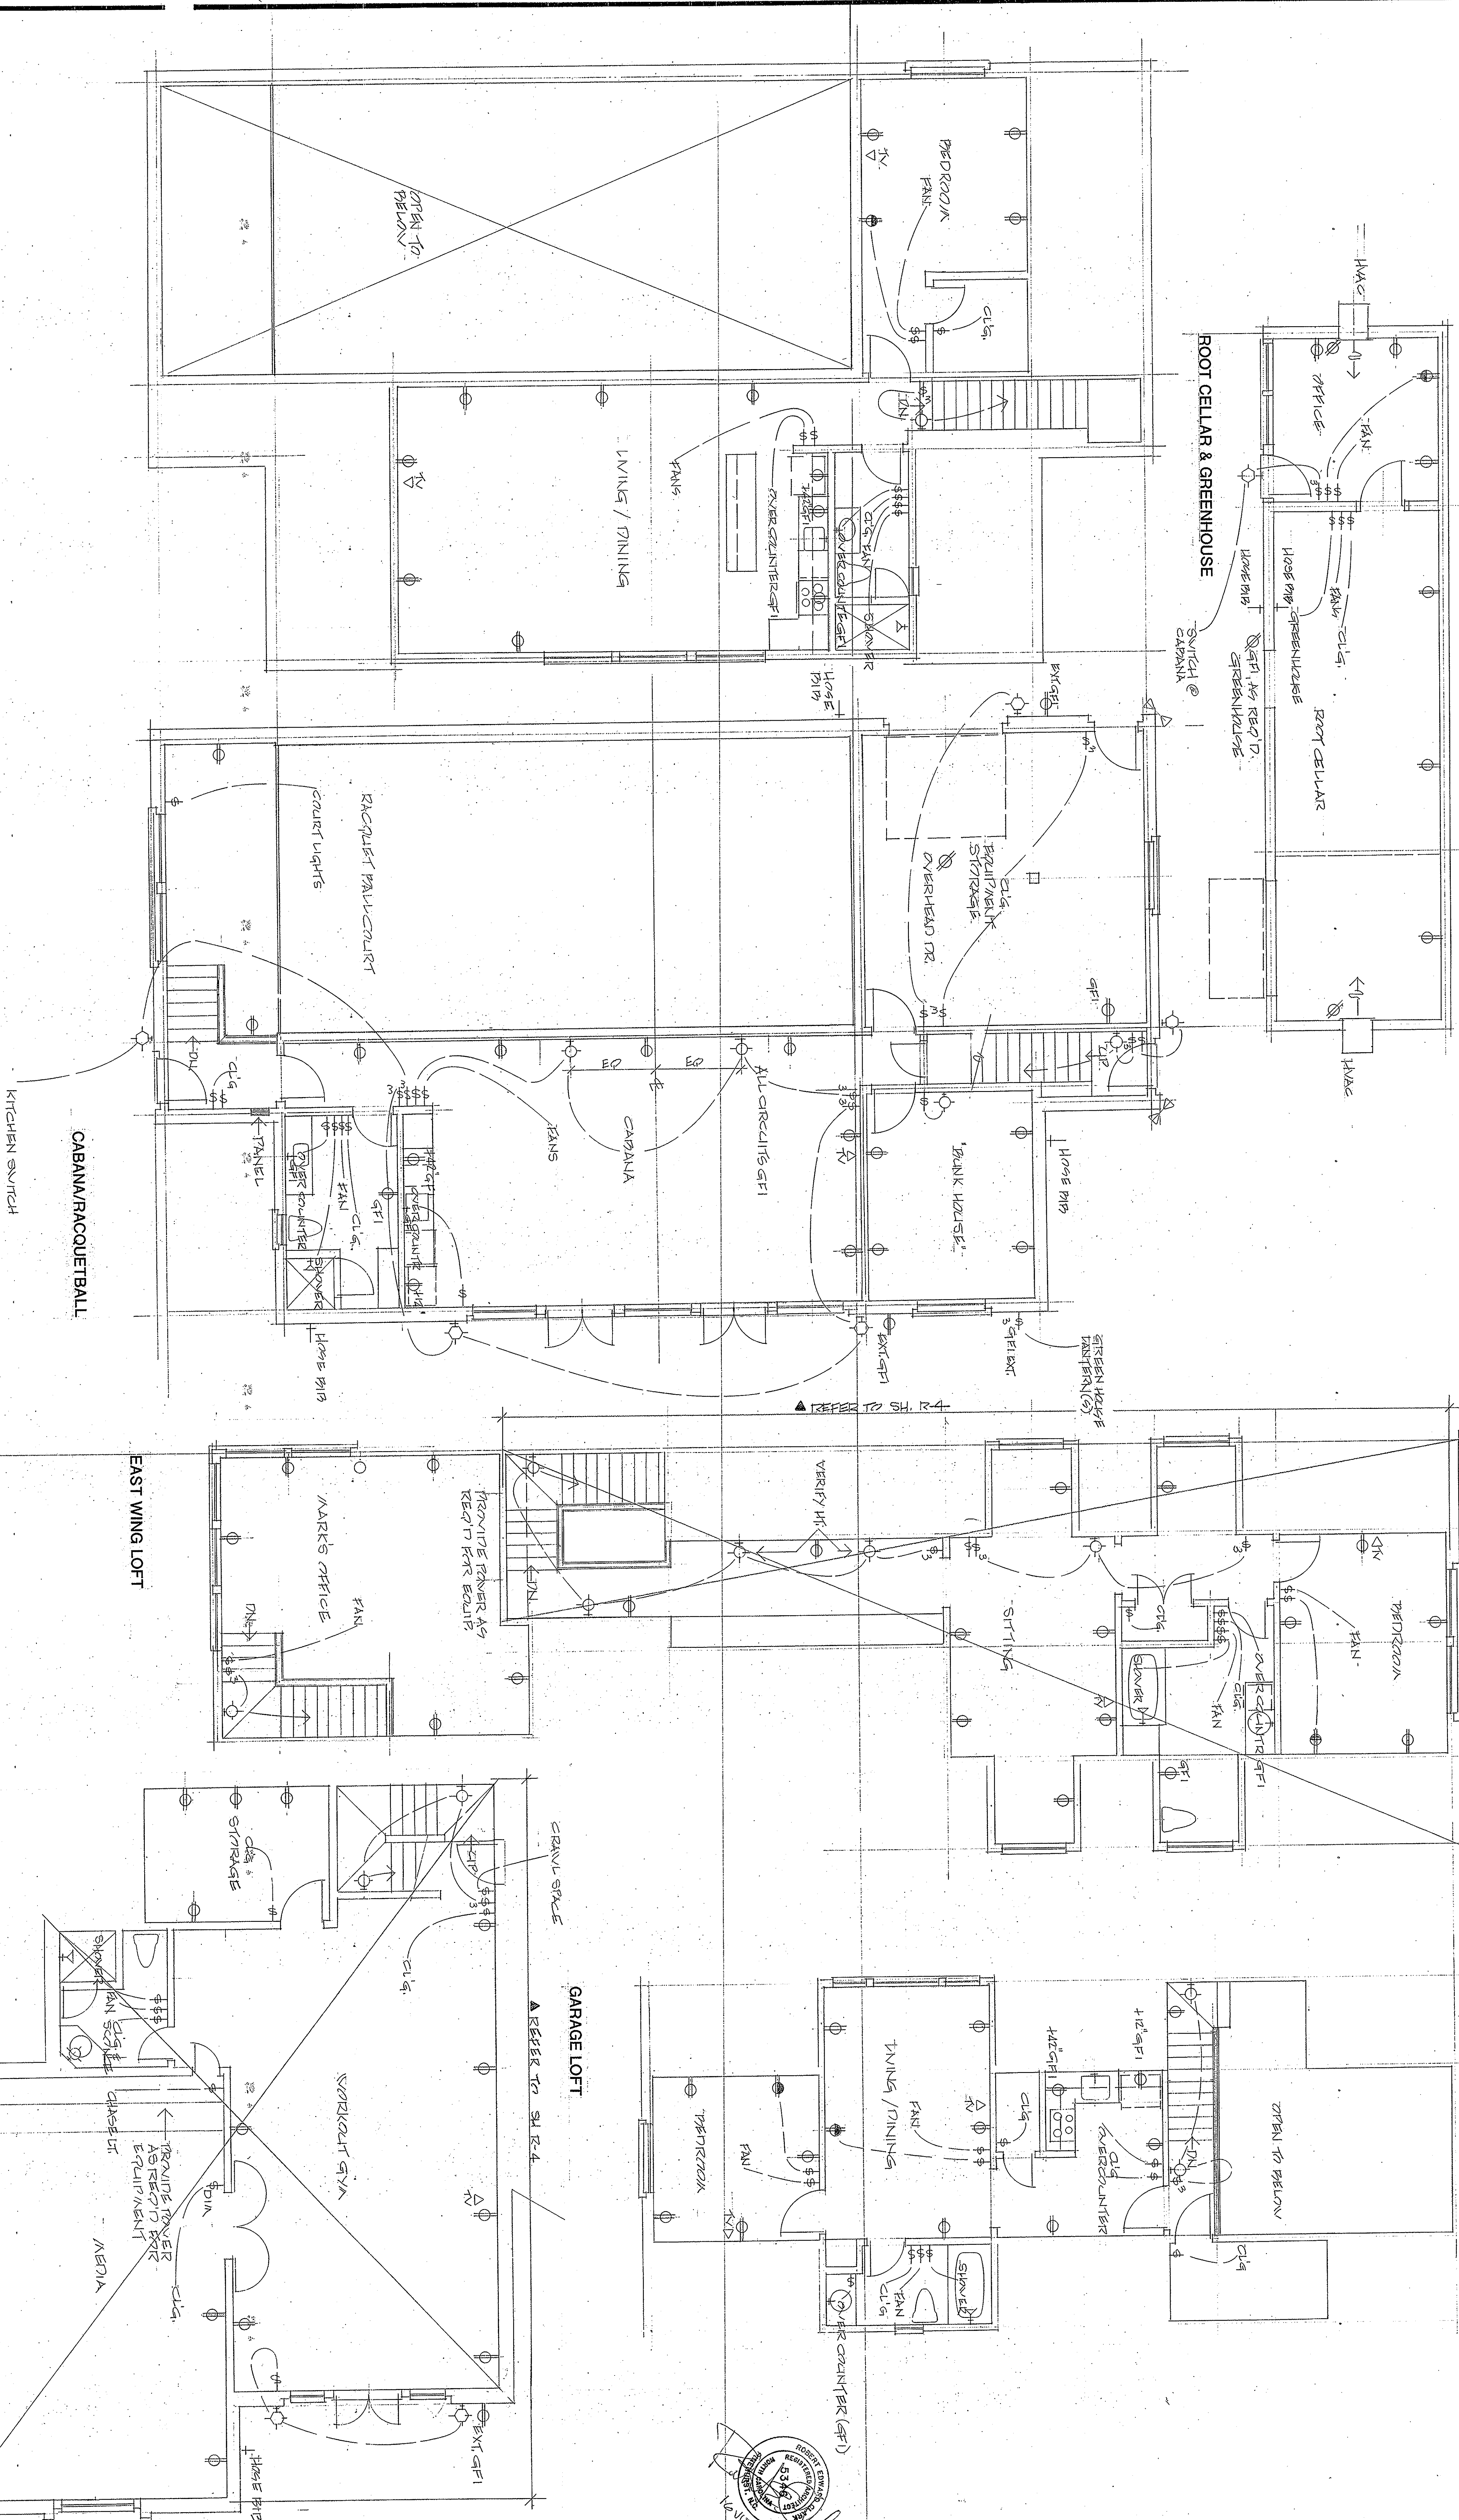

EPSTEIN/LATHAM RESIDENCE 1214 LINDEN TRAIL, PINEHURST, NC

7-11-08  
APPROVED & ACCEPTED DATE

REVISIONS

THE ARCHITECT RETAINS THE RIGHT OF AUTHORSHIP FOR IDEAS EXPRESSED AS HIS WORK, AND AS SUCH ALL DRAWINGS AND SPECIFICATIONS REMAIN THE PROPERTY OF THE ARCHITECT WHETHER THE PROJECT FOR WHICH THEY ARE INTENDED IS EXECUTED OR NOT AND MAY NOT BE USED ON OTHER PROJECTS OR EXTENSIONS OF THIS PROJECT EXCEPT BY AGREEMENT WITH THE ARCHITECT.

ROBERT E. CLARK AIA ARCHITECT


910 295 4683 FAX 910 295 5684  
65 COMMUNITY ROAD  
PINEHURST NORTH CAROLINA 28370




ROOF FRAMING

FLOOR FRAMING

FOUNDATION

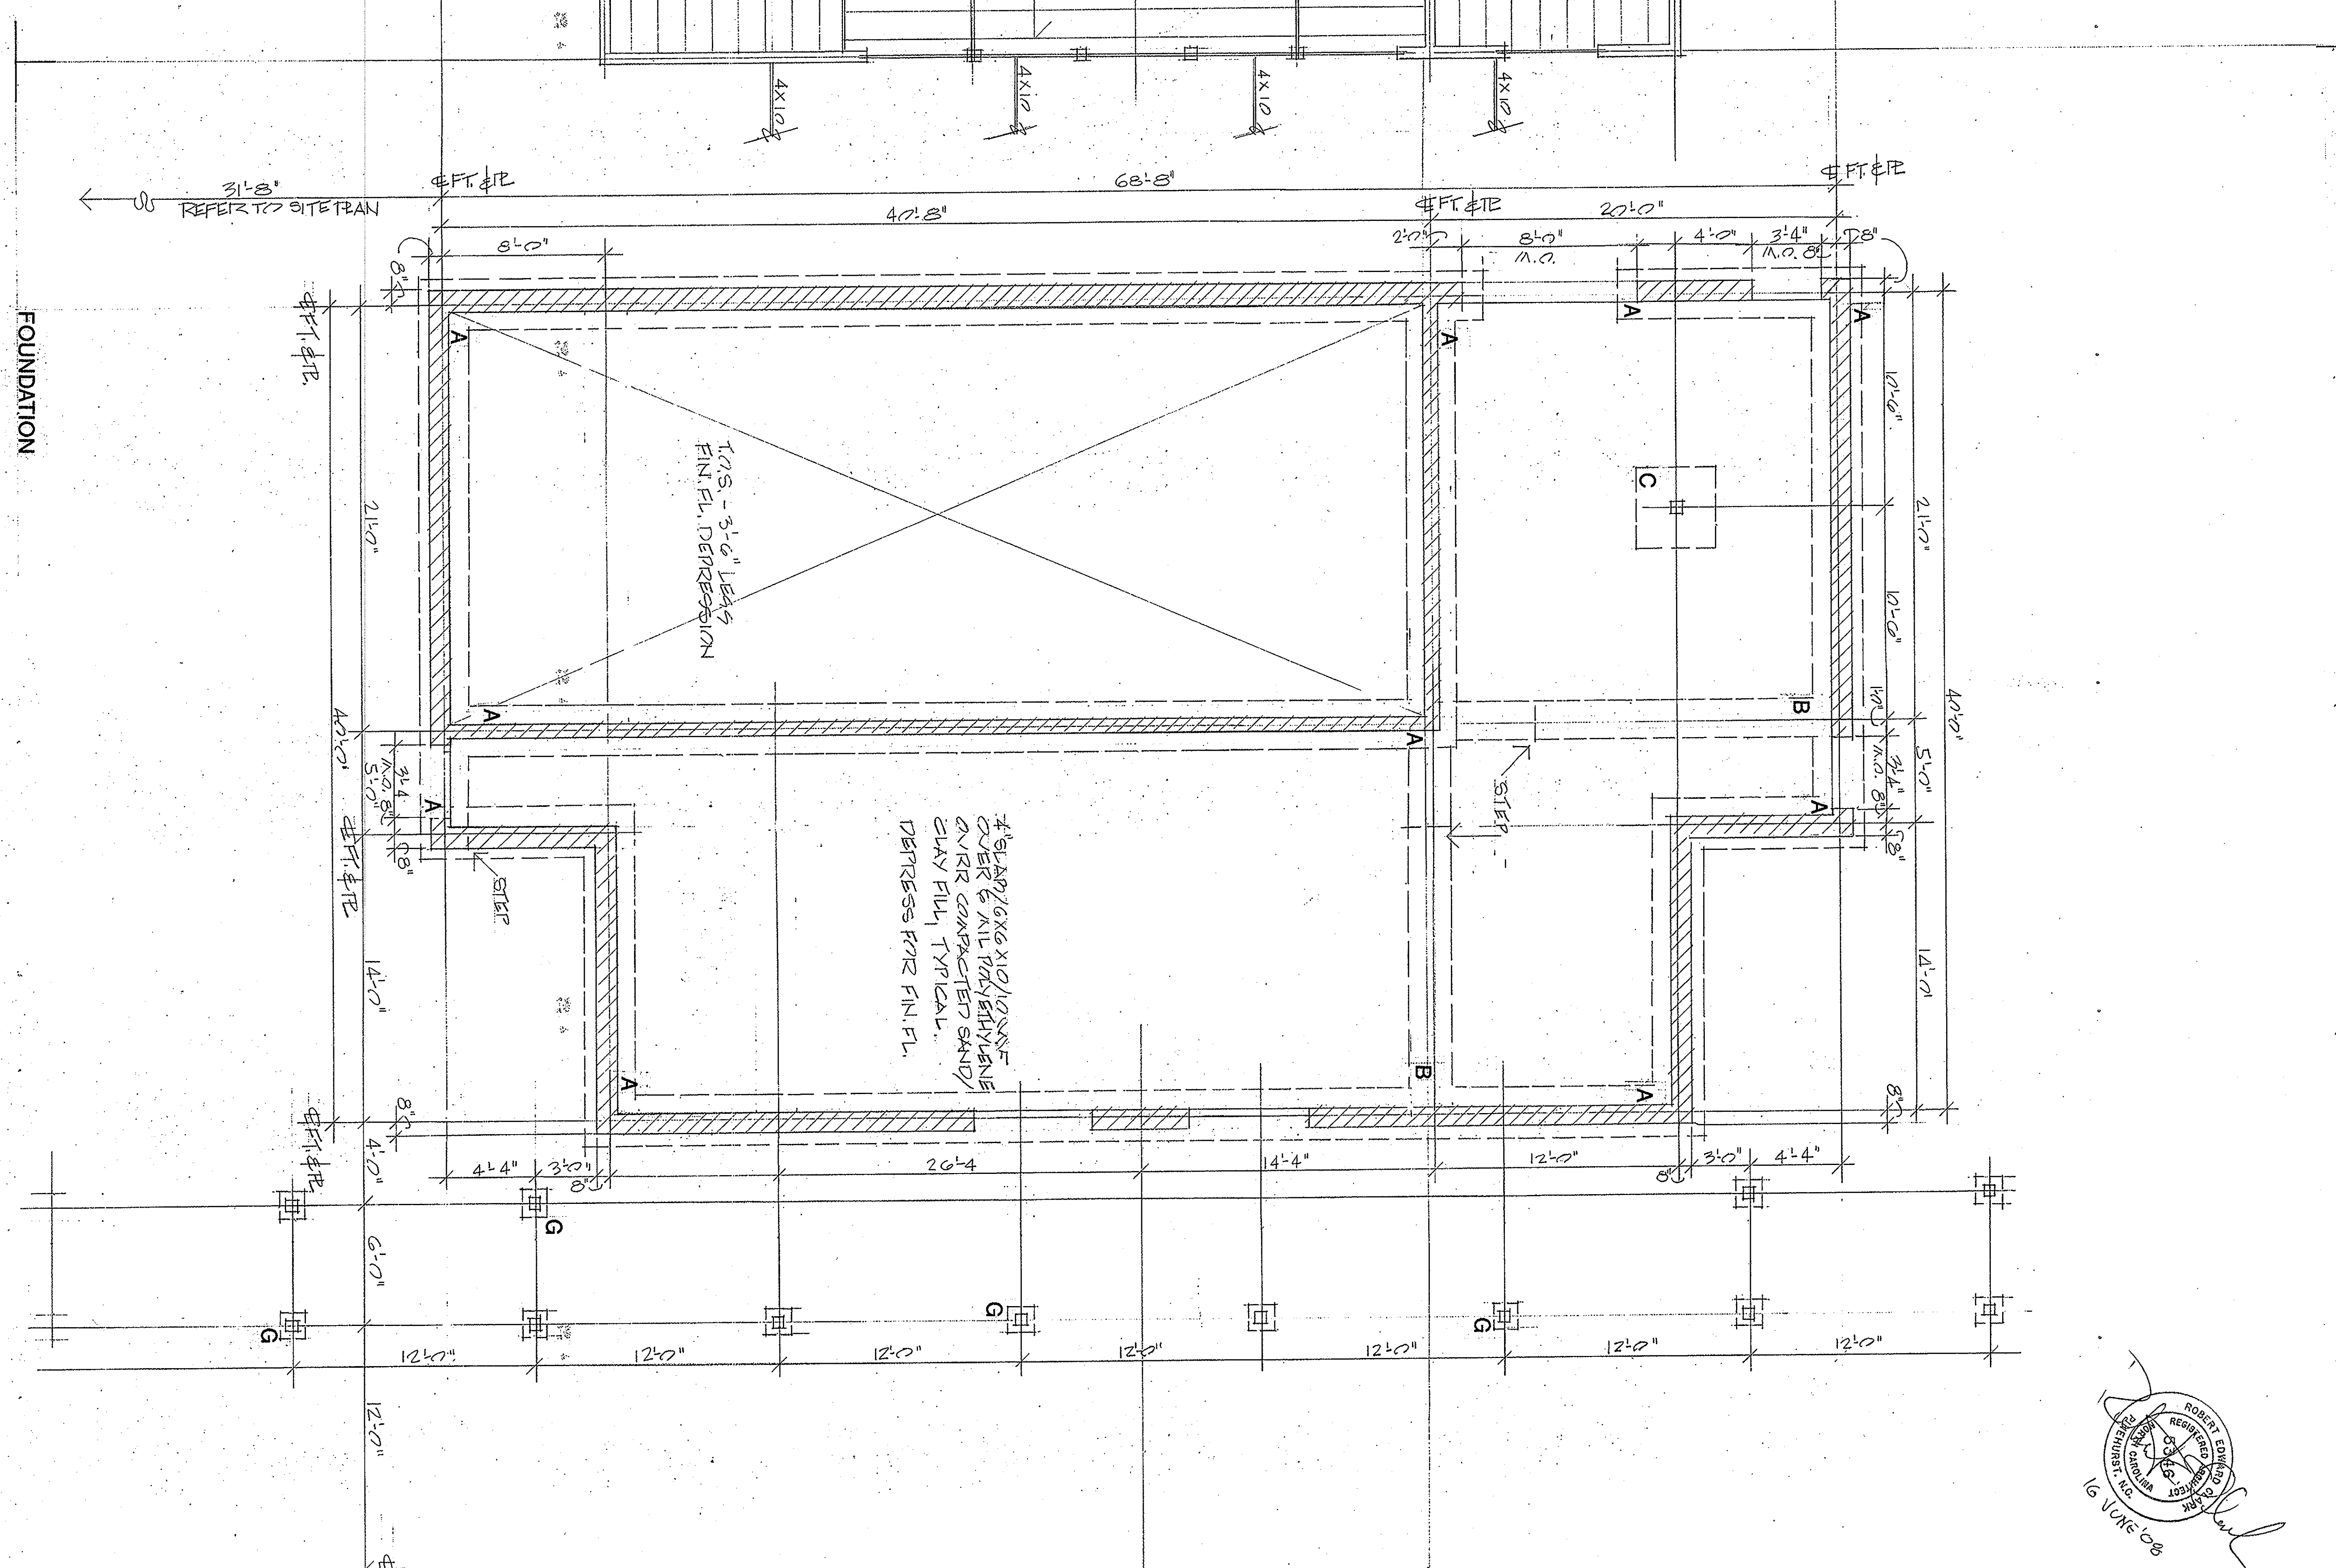

PLANS 1/4"=1'-0"

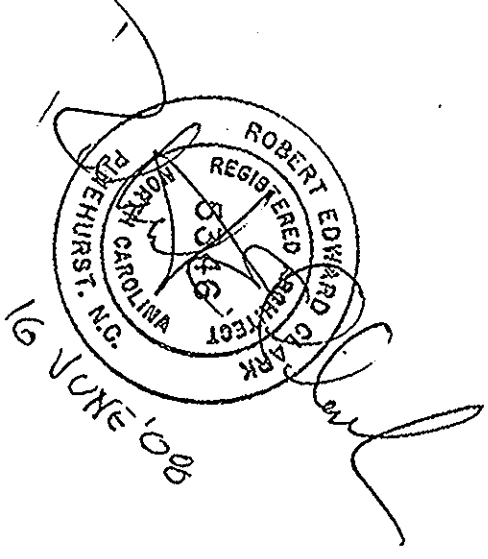

604106 FEB  
08 JULY 2008  
16 JUNE 2008

|                                                            |         |
|------------------------------------------------------------|---------|
| EPSTEIN/LATHAM RESIDENCE LOT 4 LINDEN TRAIL, PINEHURST, NC |         |
| APPROVED & ACCEPTED                                        | DATE    |
| <i>Julie Blanton</i>                                       | 7-11-08 |

THE ARCHITECT RETAINS THE RIGHT OF AUTHORSHIP FOR IDEAS EXPRESSED AS HIS WORK, AND AS SUCH ALL DRAWINGS AND SPECIFICATIONS REMAIN THE PROPERTY OF THE ARCHITECT WHETHER THE PROJECT FOR WHICH THEY ARE INTENDED IS EXECUTED OR NOT AND MAY NOT BE USED ON OTHER PROJECTS OR EXTENSIONS OF THIS PROJECT EXCEPT BY AGREEMENT WITH THE ARCHITECT.


ROBERT E. CLARK AIA ARCHITECT  
910 295 4683 FAX 910 295 5684  
65 COMMUNITY ROAD  
PINEHURST NORTH CAROLINA 28370  
P O BOX 205




LOFT

CABANA/RACQUETBALL COURT PLANS 1/4"=1'-0"

GROUND FLOOR

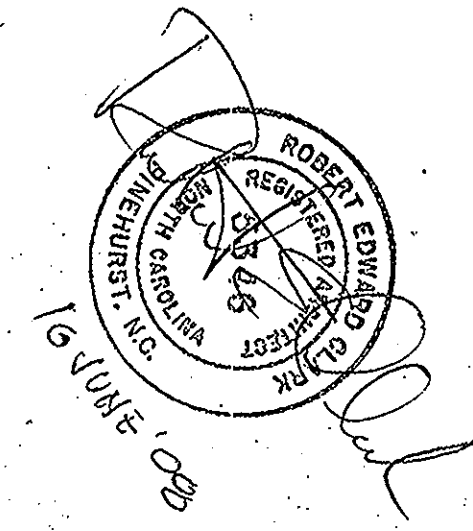


REVISIONS  
1 MAY 08 DEC  
28 MAR 08 DEC  
12 MAR 08 DEC

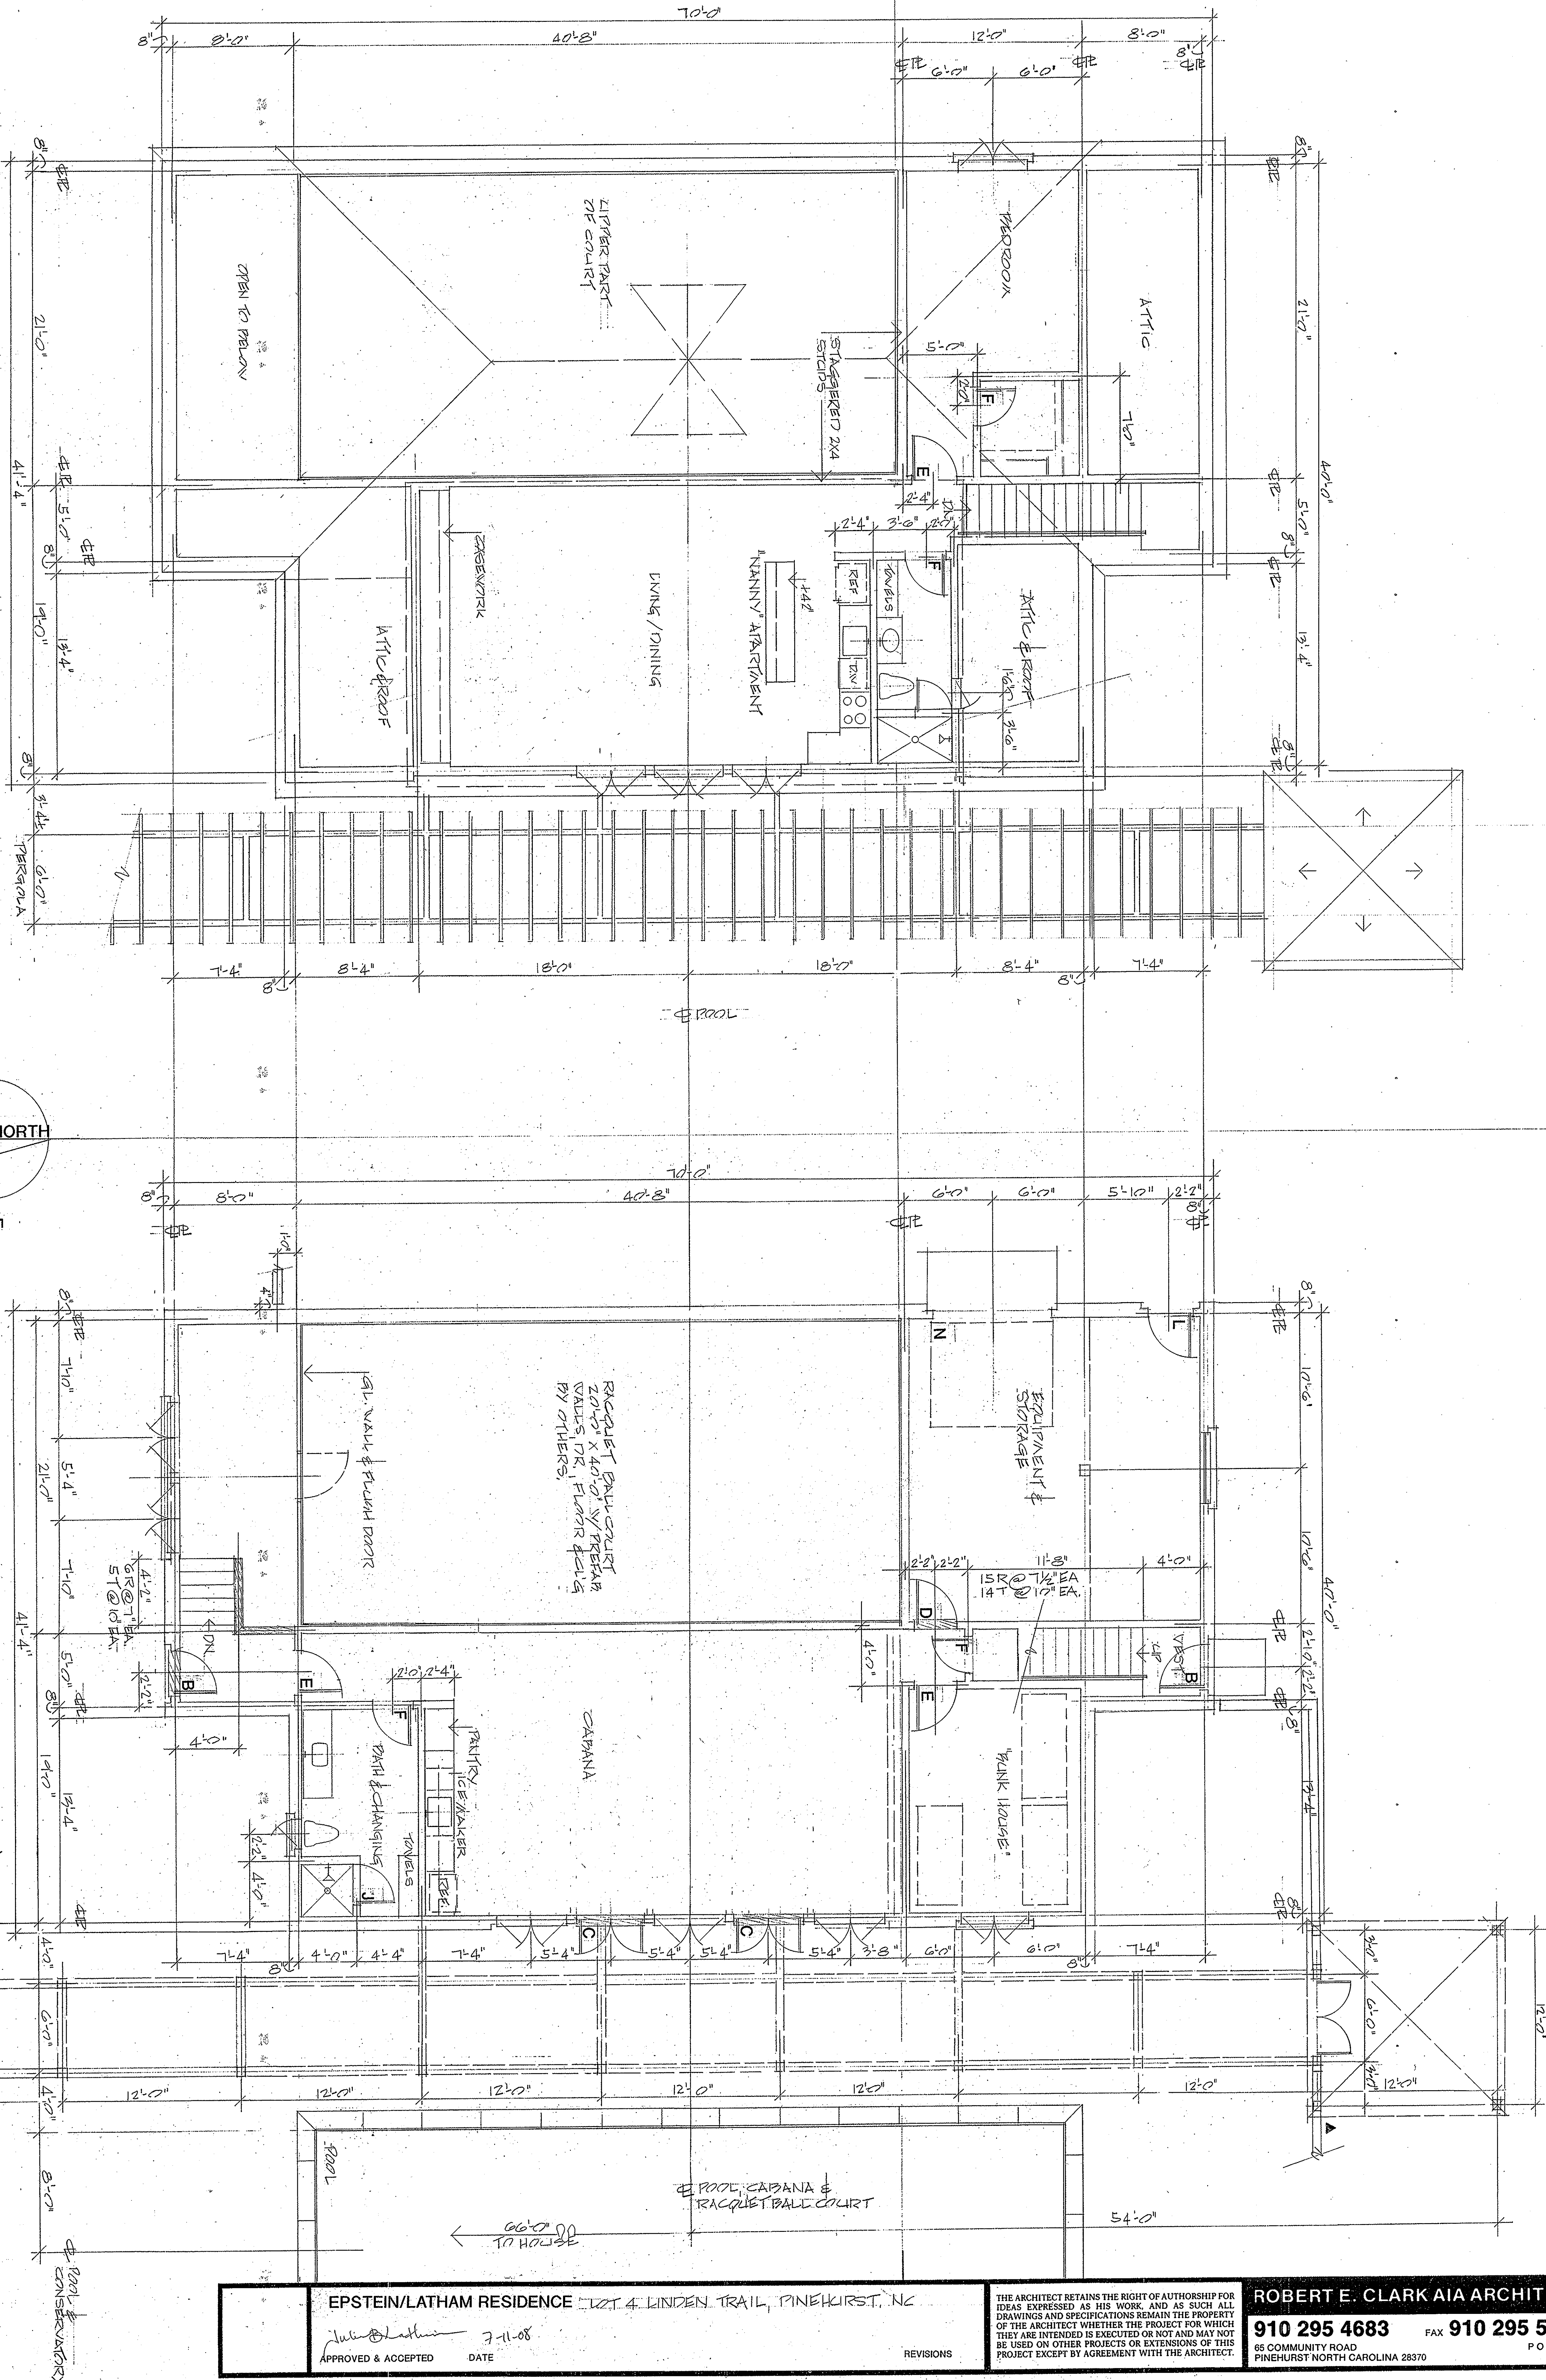
















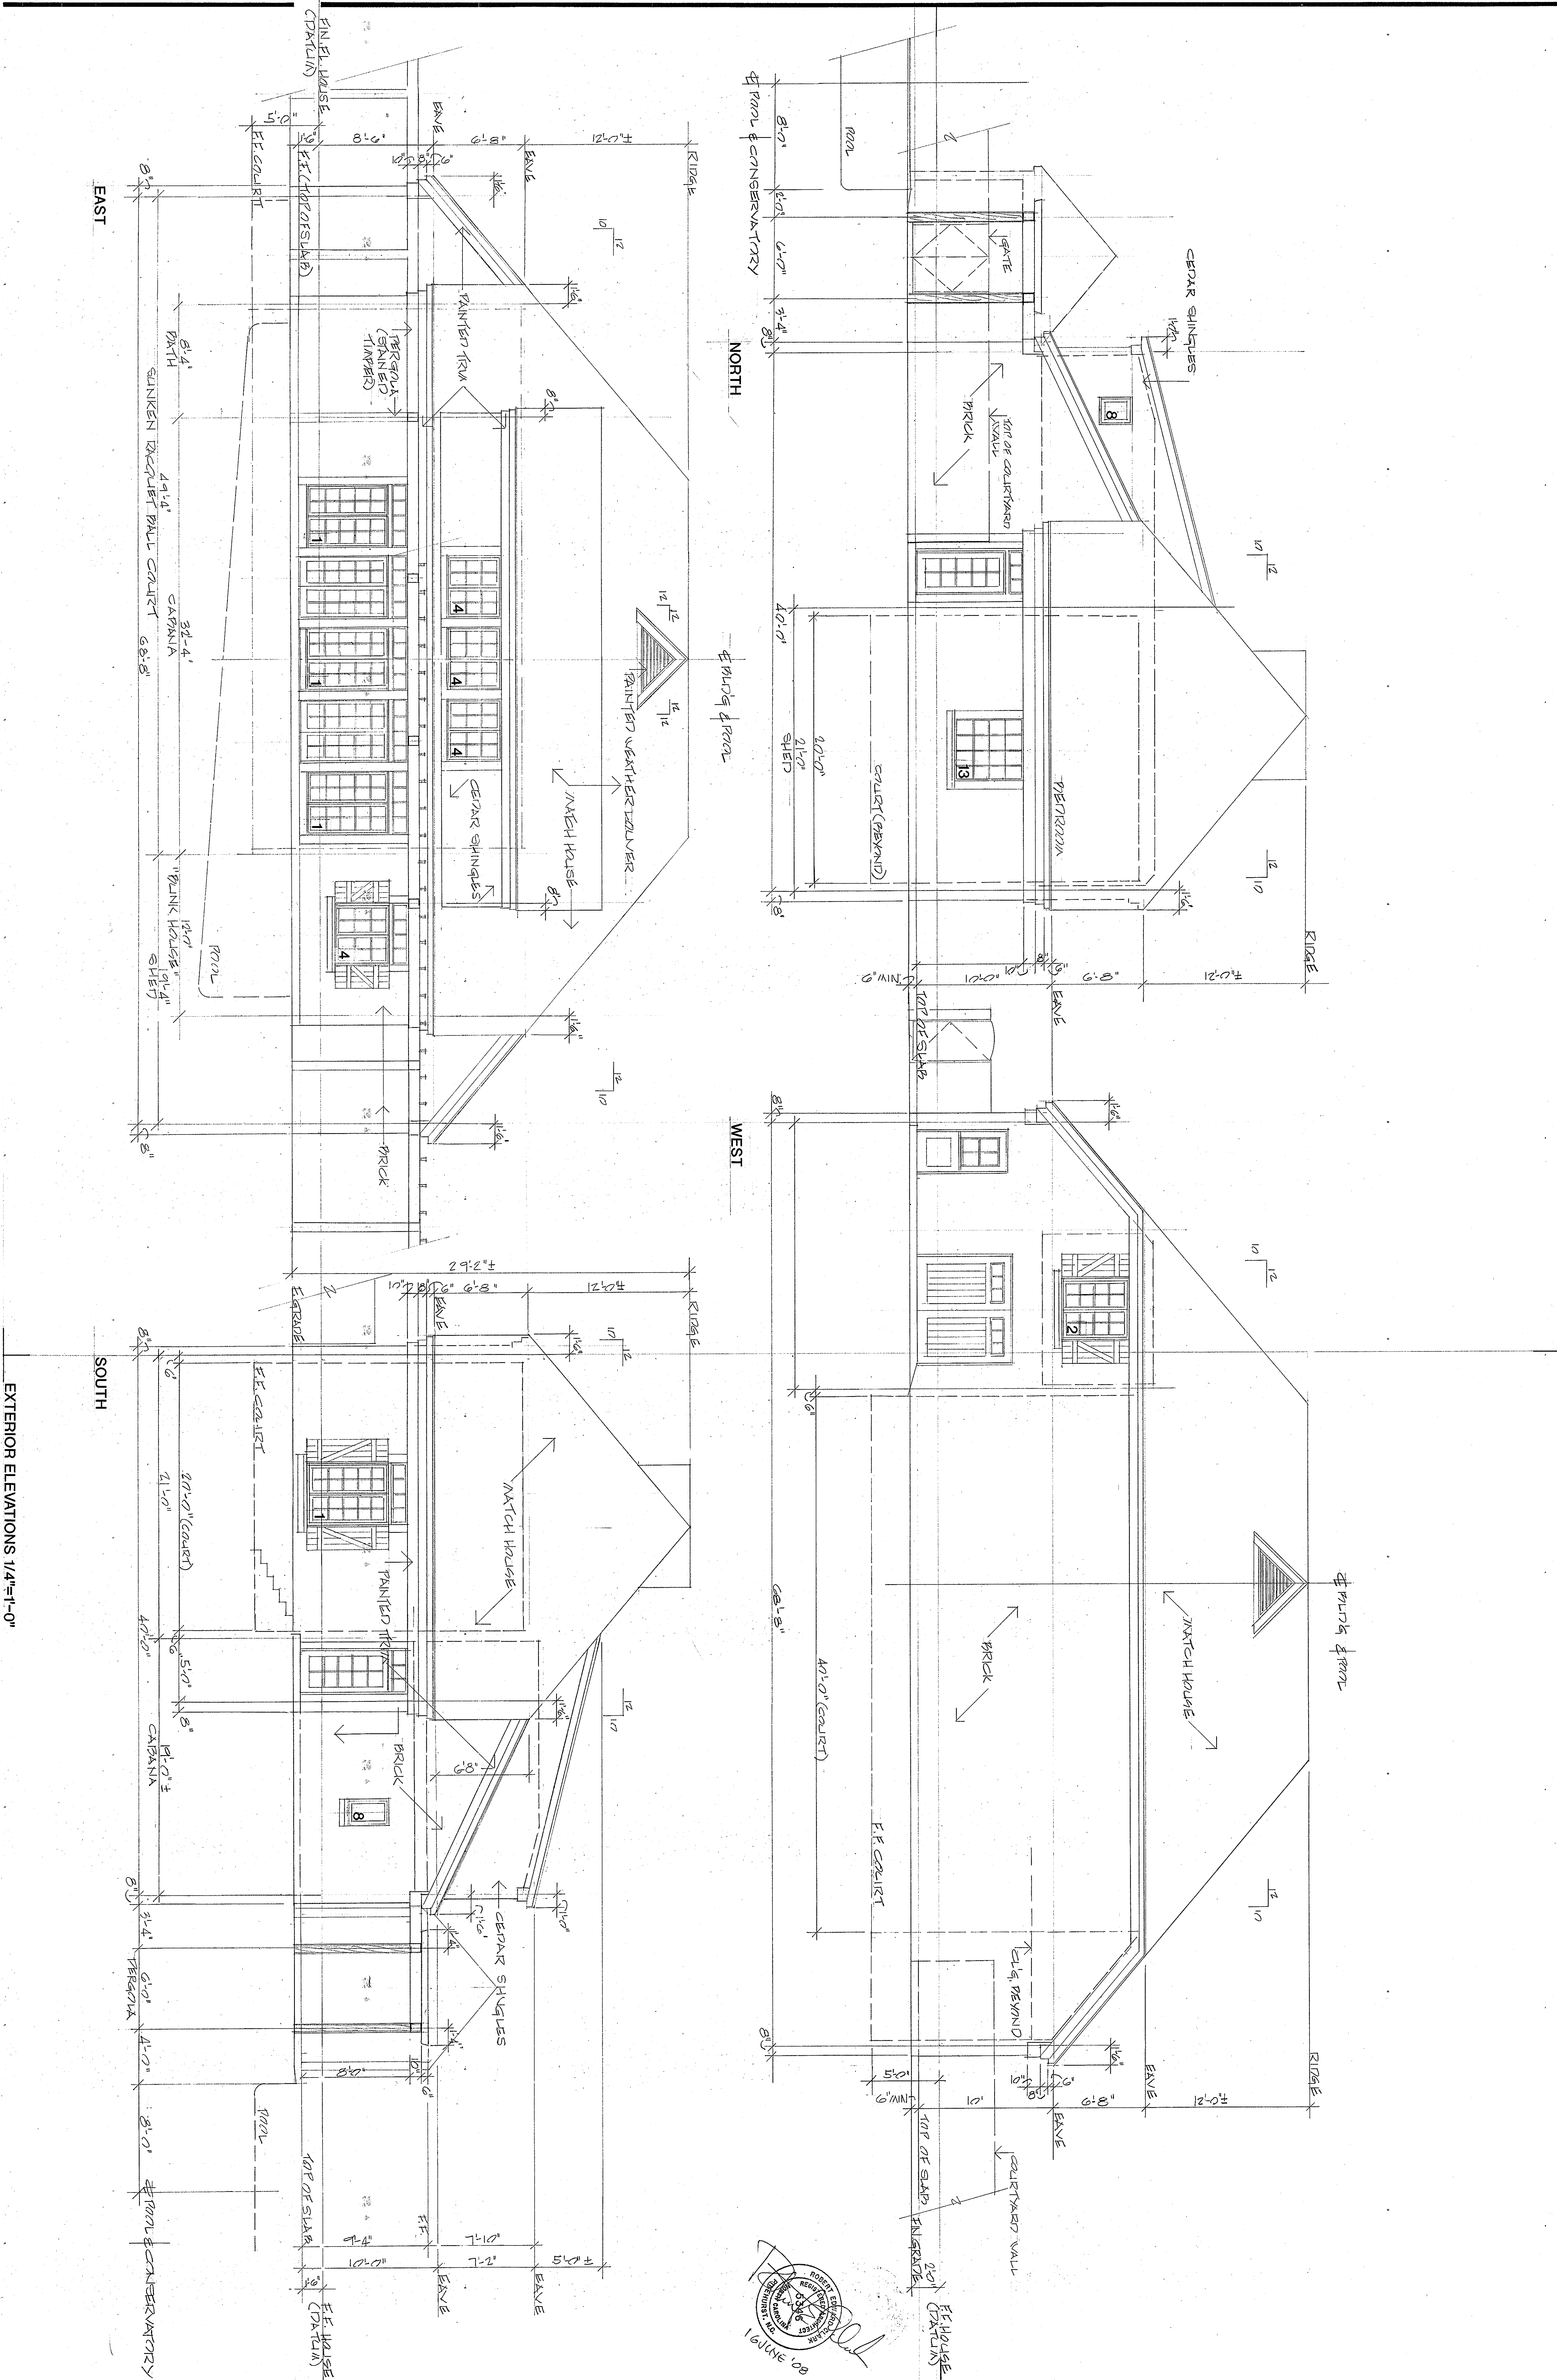



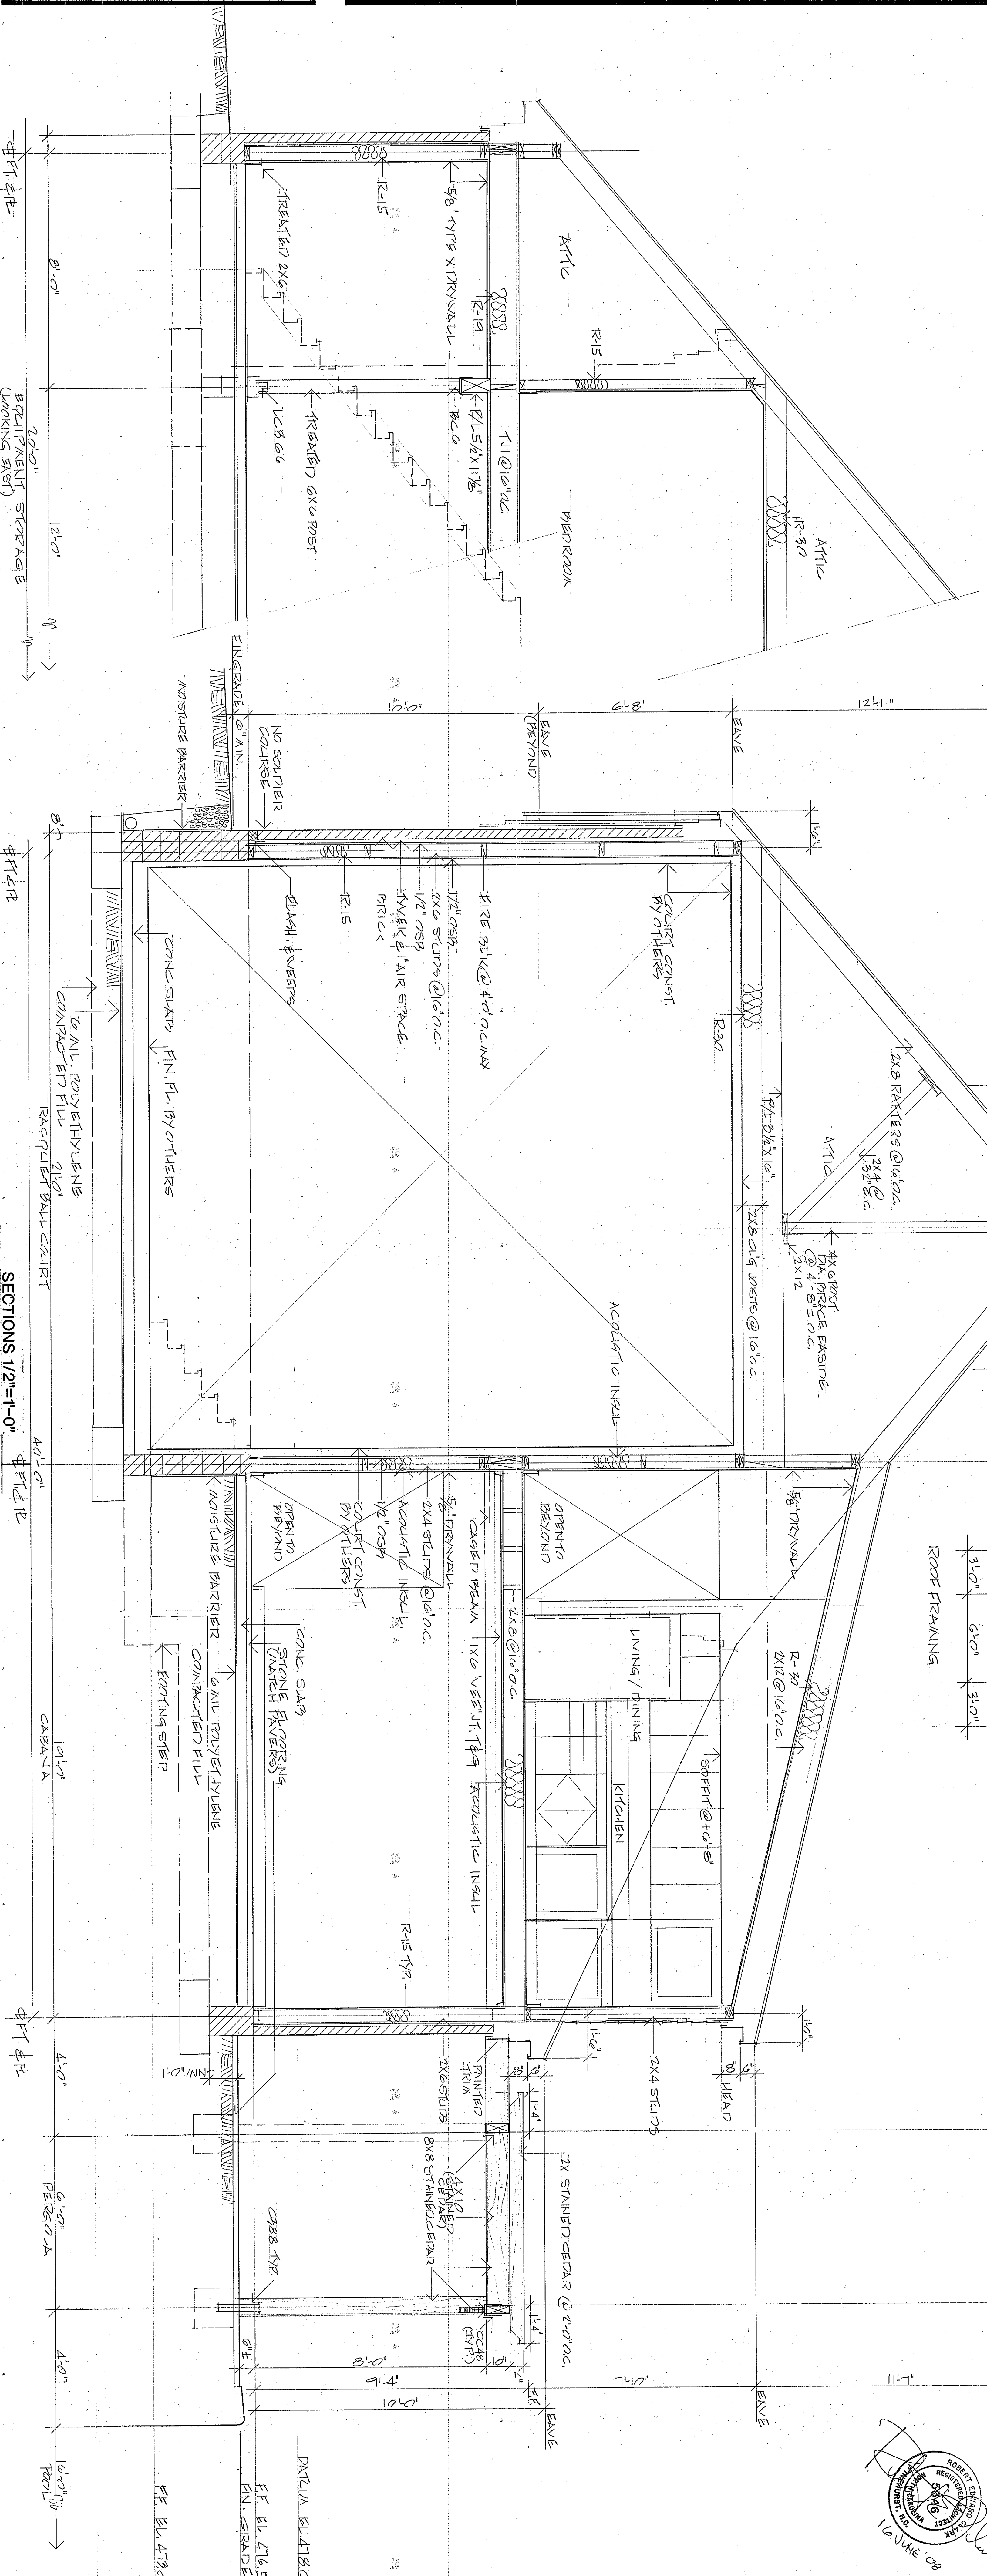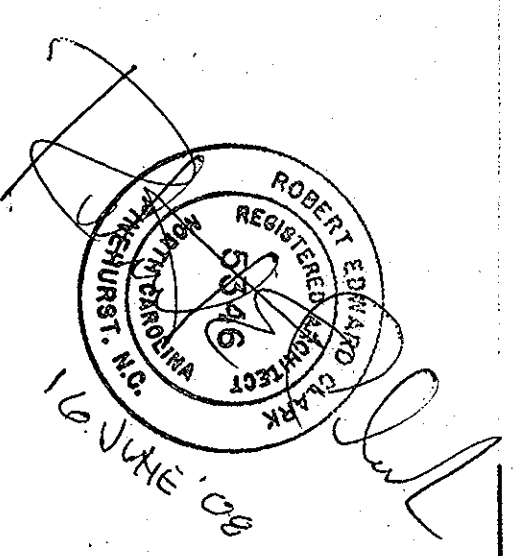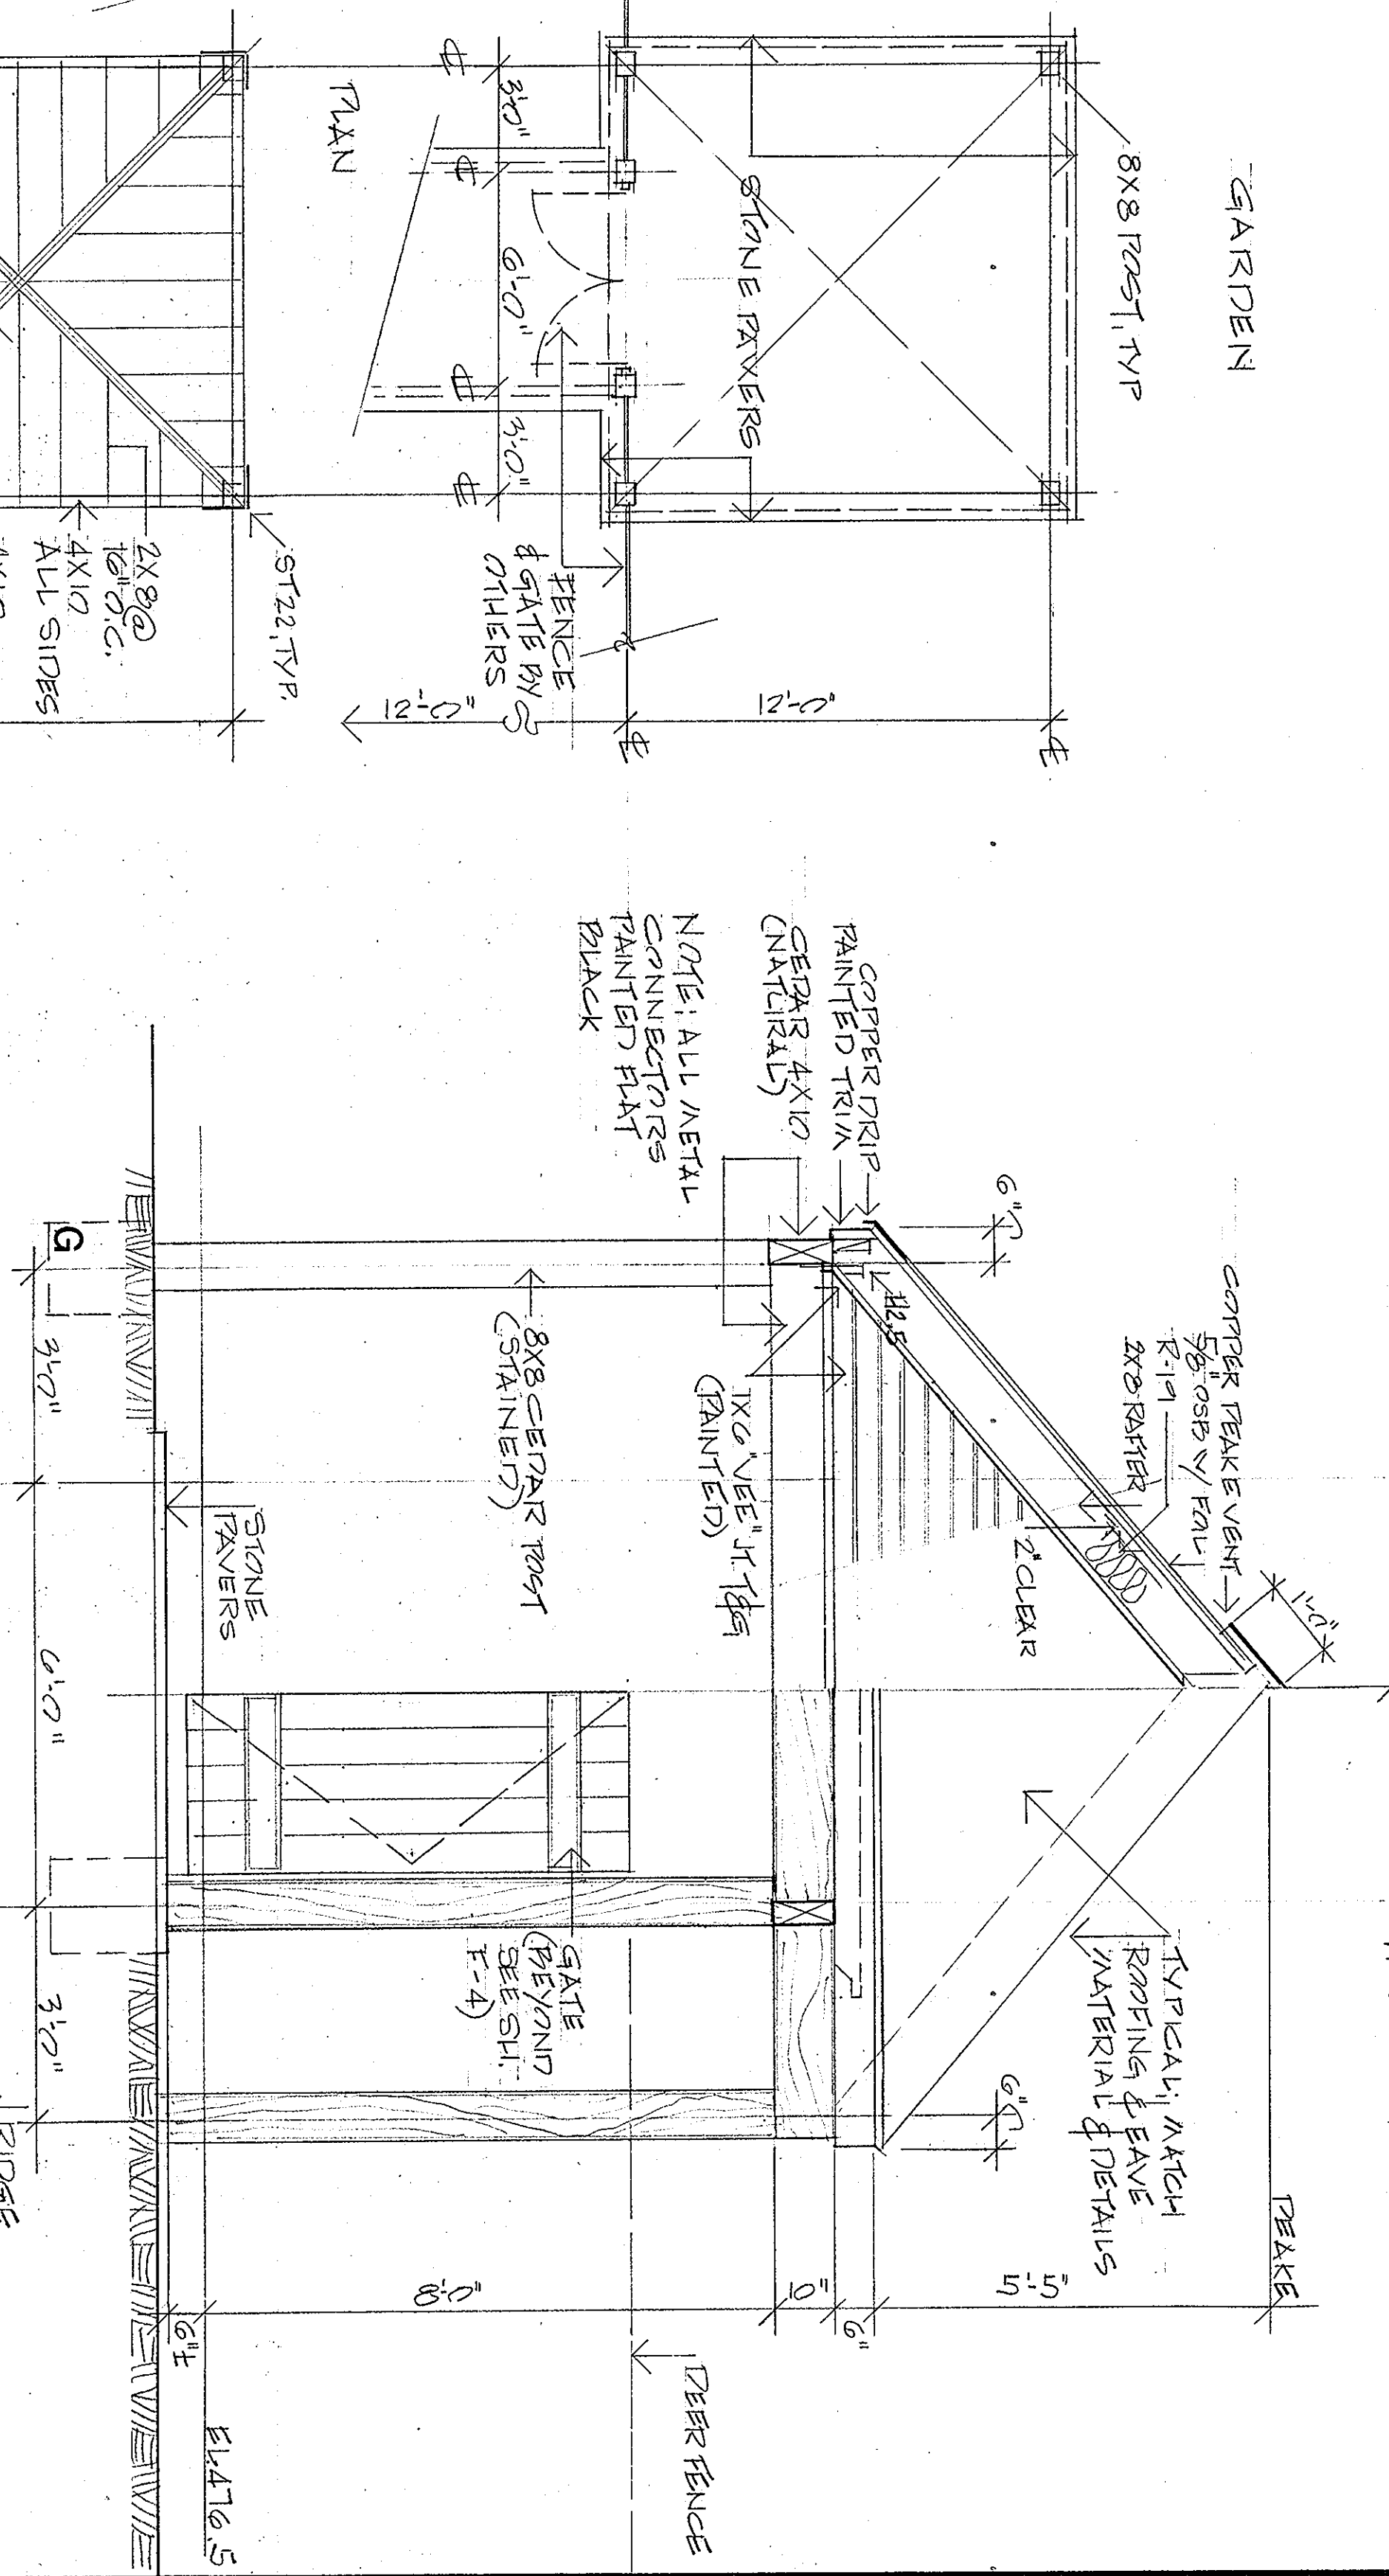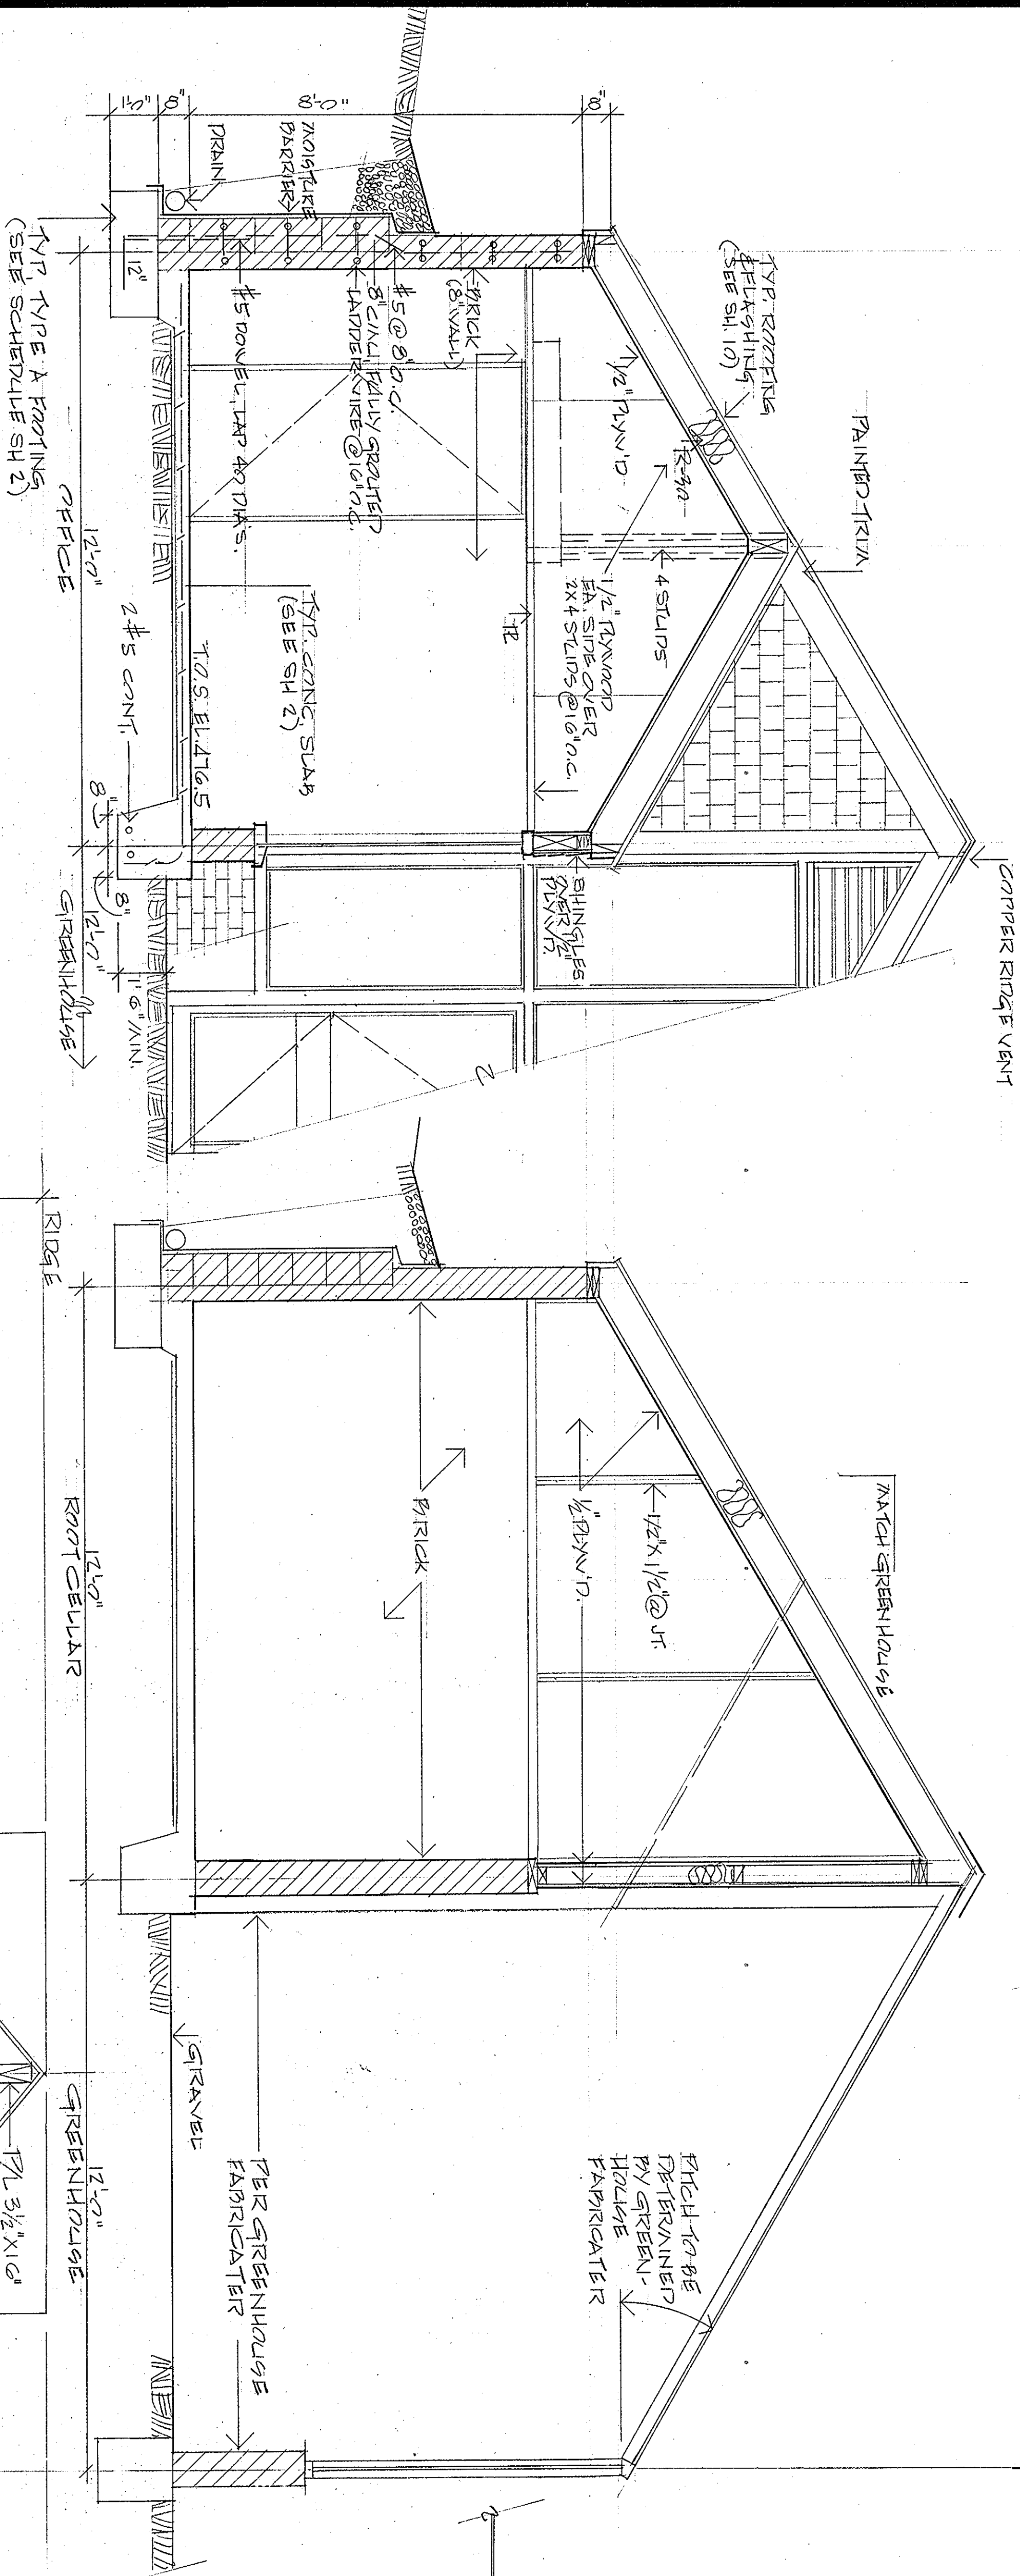



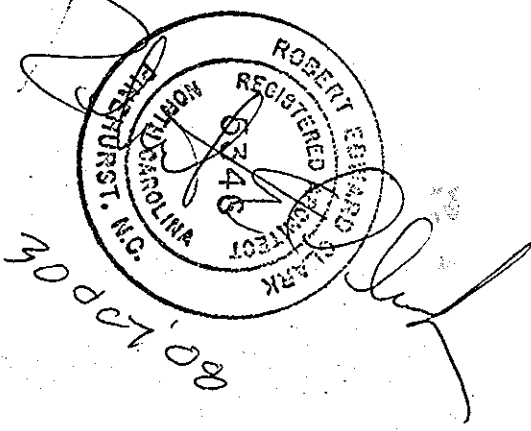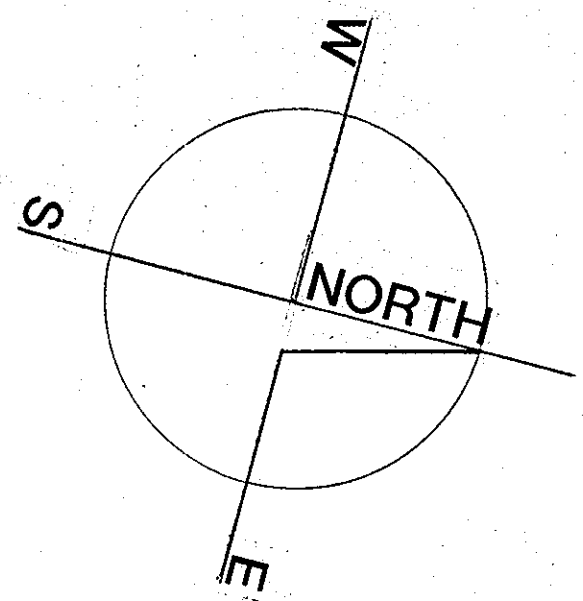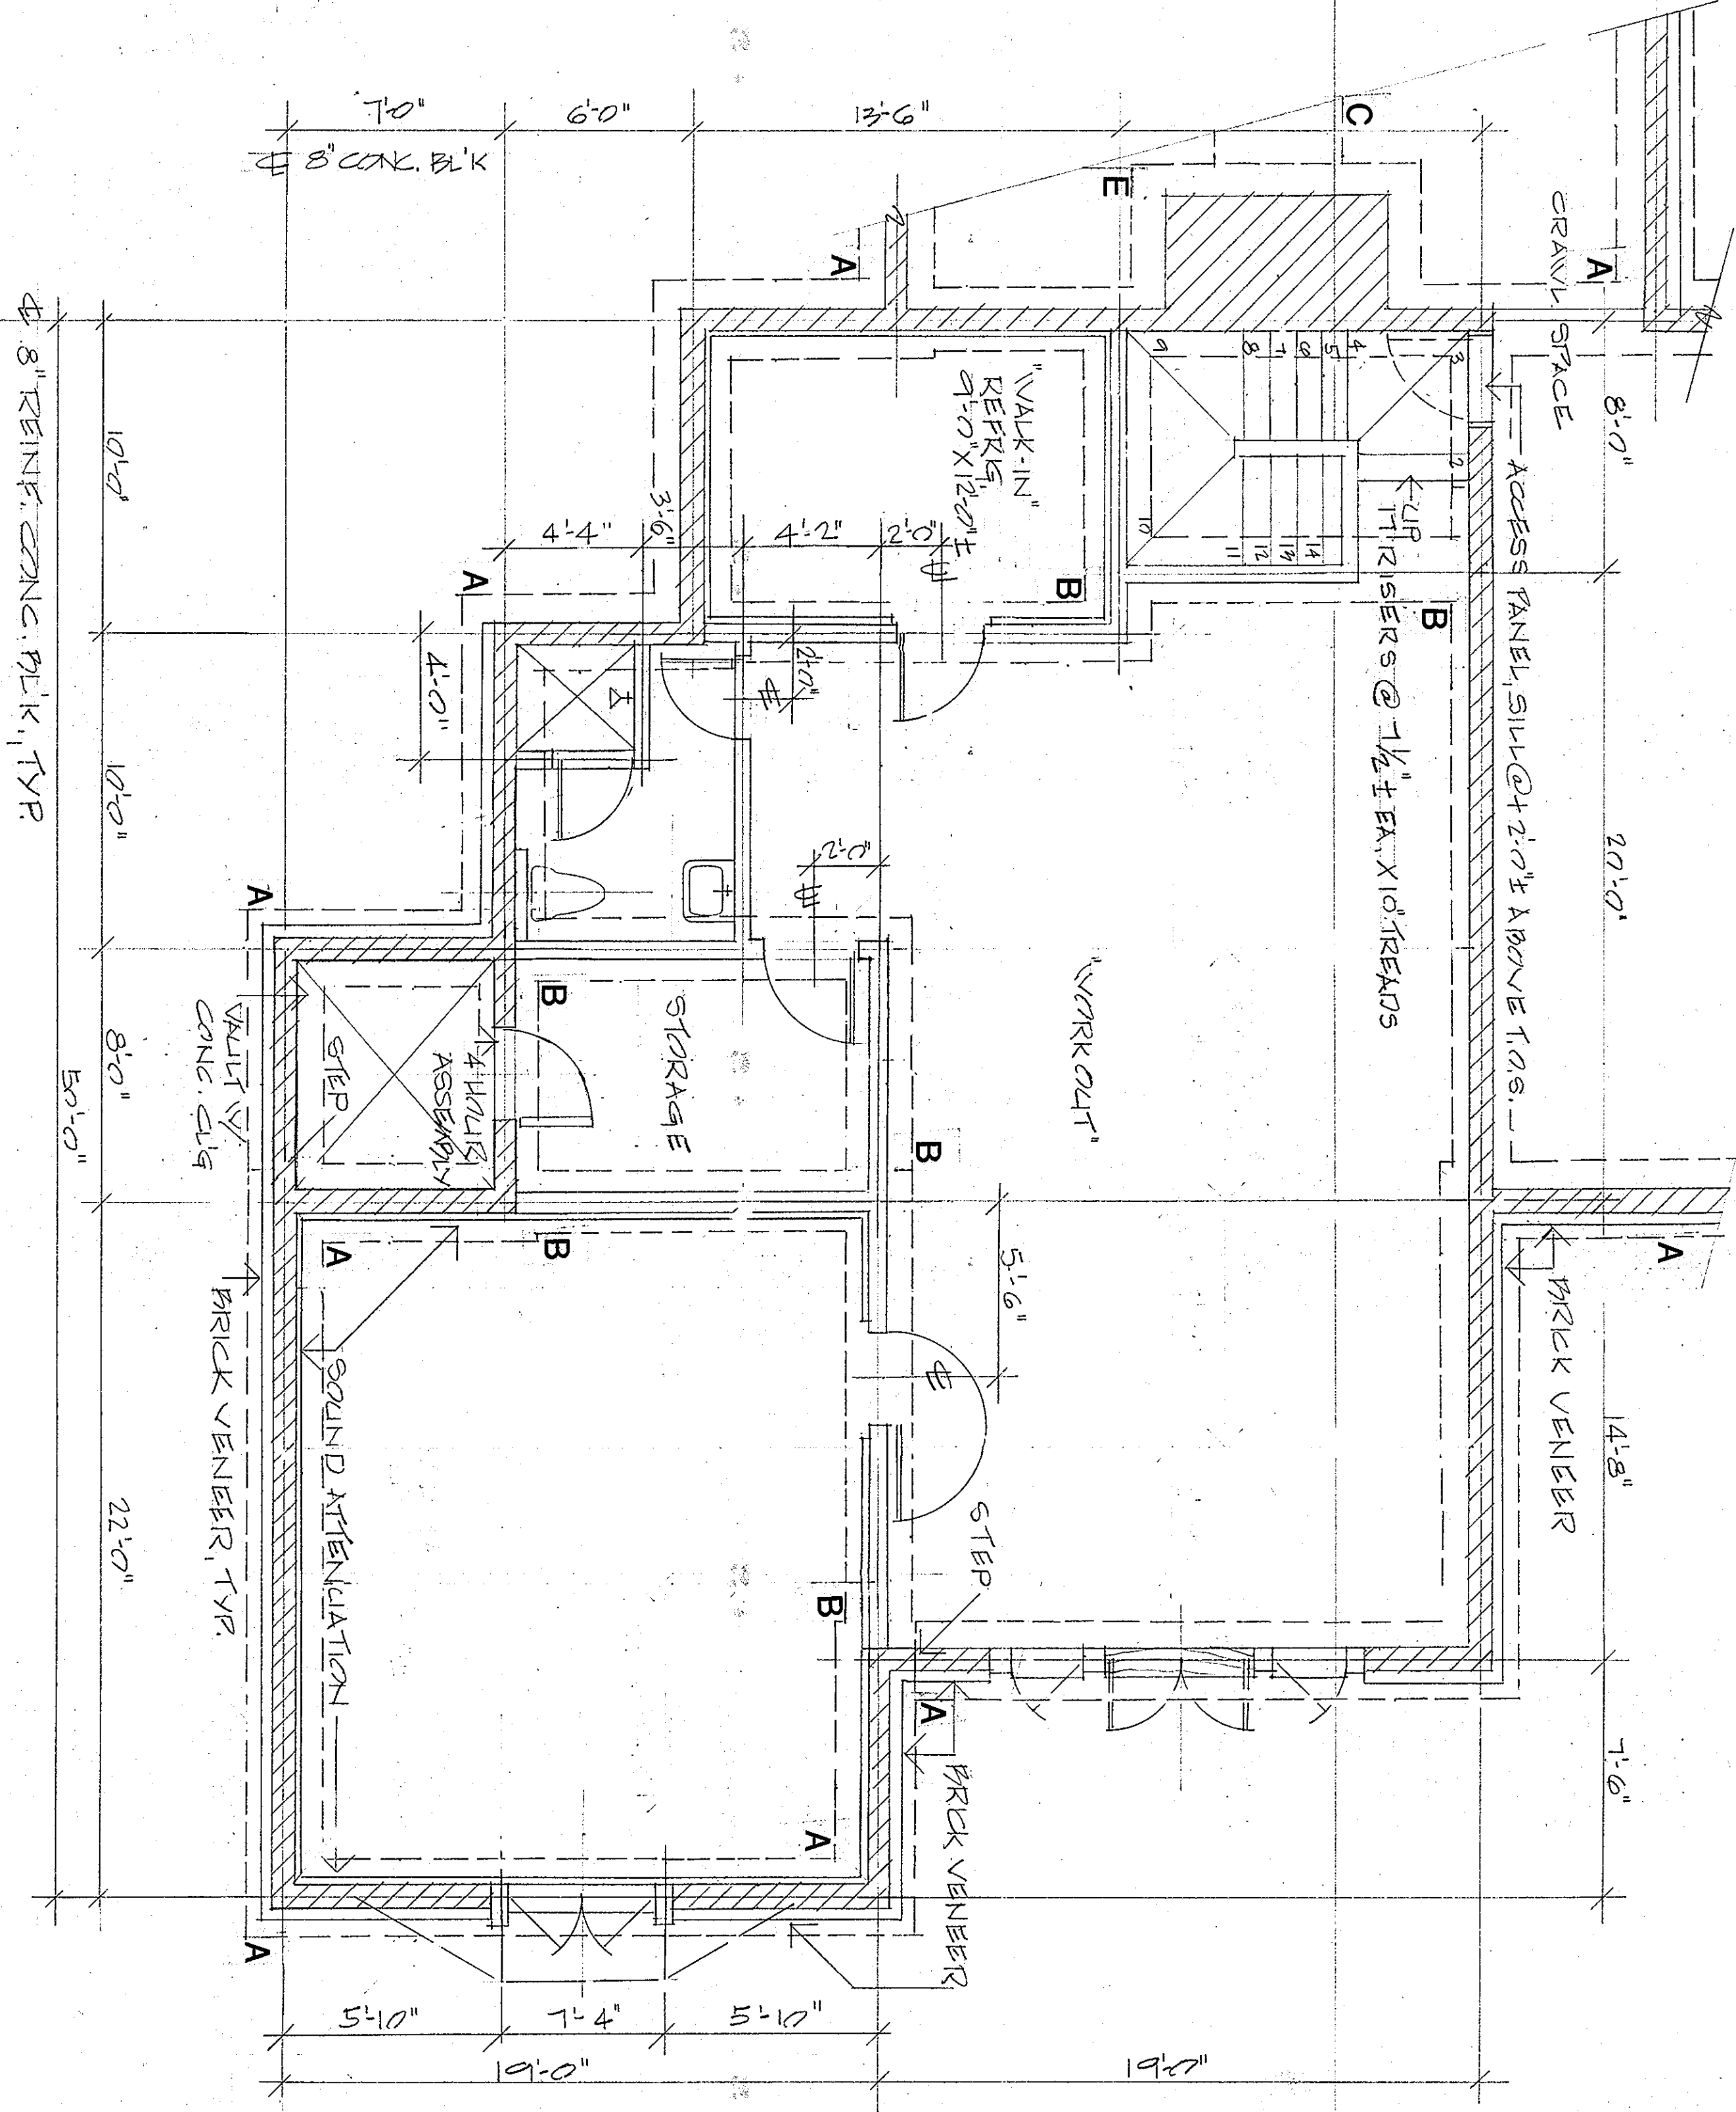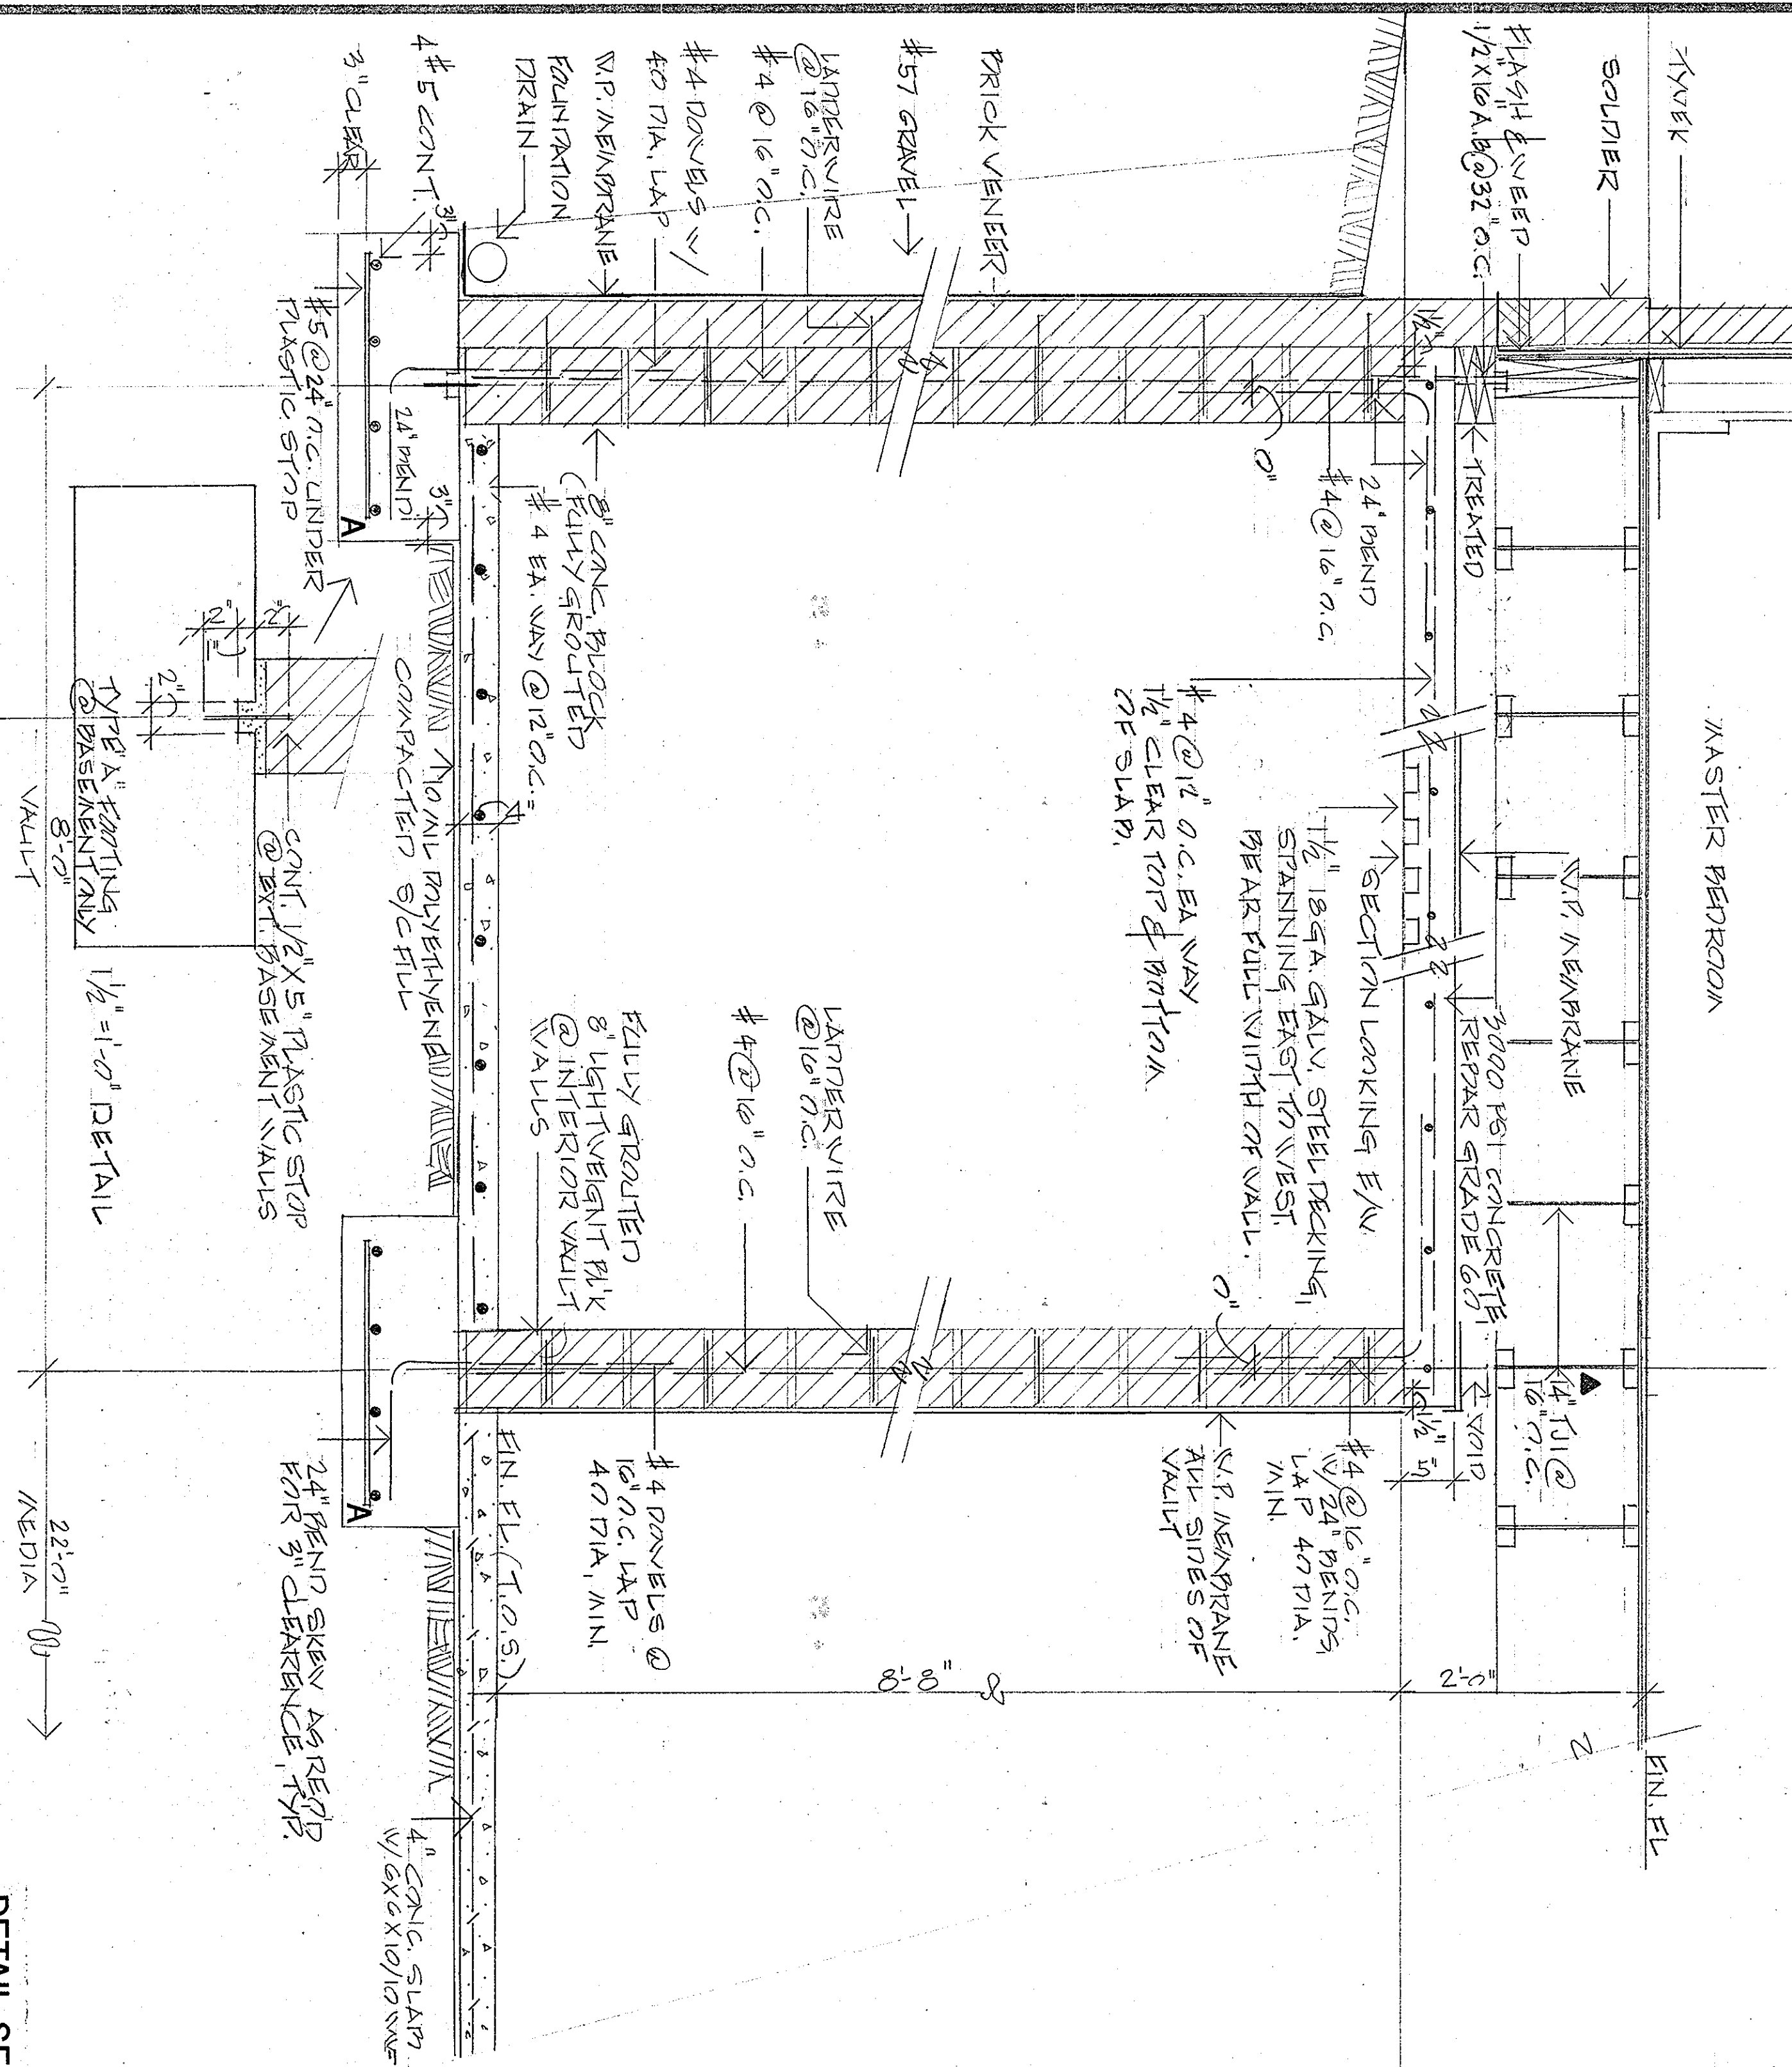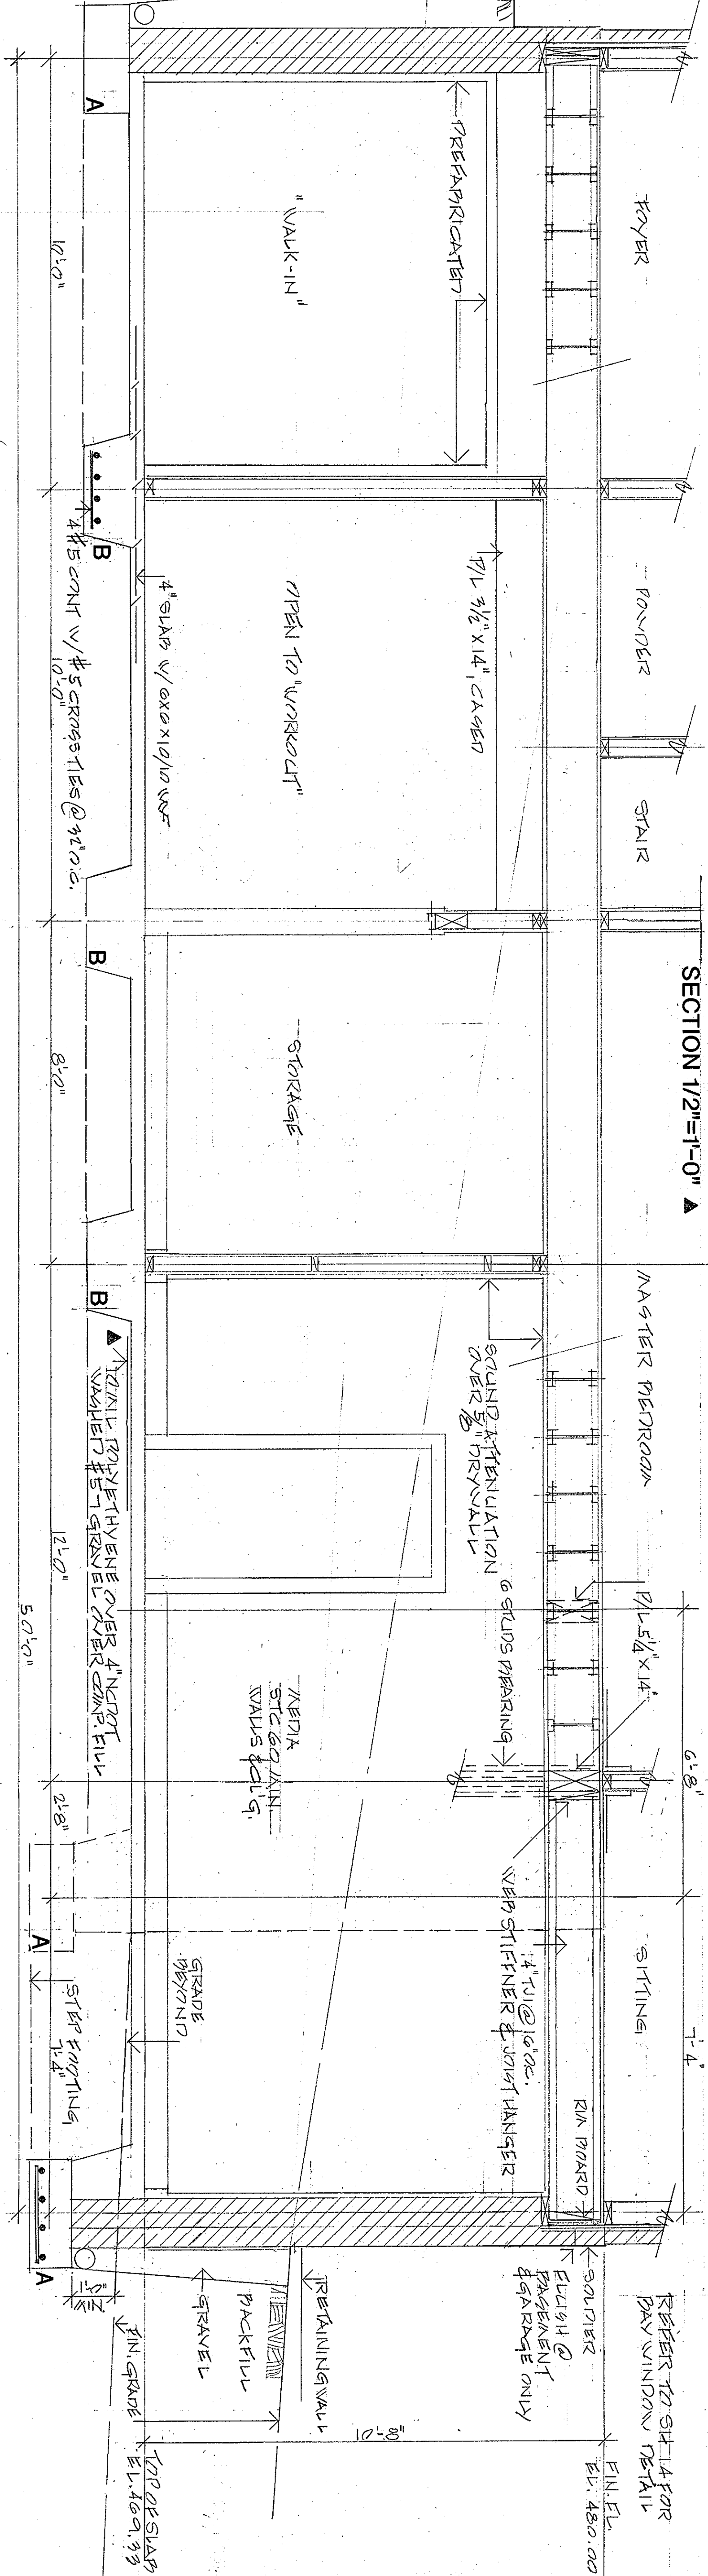

▲ 6 FEB '09 REC  
28 JAN '09 REC  
30 OCT '08 REC  
24 OCT '08 REC




FOUNDATION & FLOOR FRAMING  
REFER TO SHEET S2

NOT  
REFER TO SHEET FC

PLANS 1/4"=1'-0"

GROUND FLOOR  
REFER TO SHEET F5

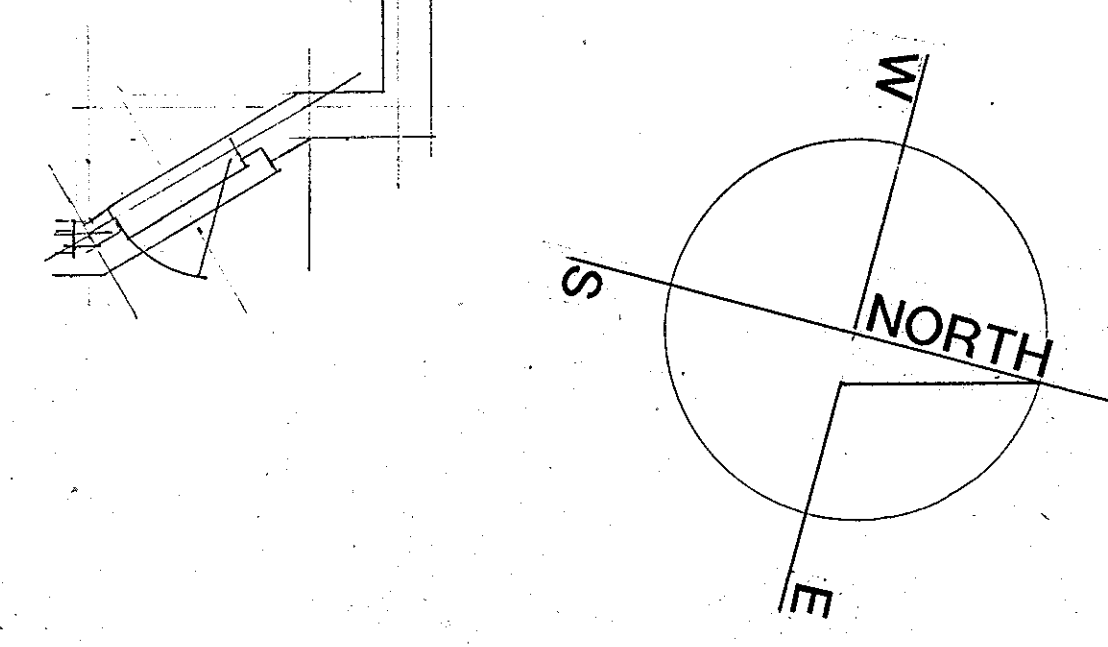

6 FEB '09 REC  
5 JAN '09 REC  
10 DEC '08 REC

1  
2

EPSTEIN/LATHAM RESIDENCE LOT 4 LINDEN TRAIL, PINEHURST, NC


APPROVED & ACCEPTED DATE REVISIONS

THE ARCHITECT RETAINS THE RIGHT OF AUTHORSHIP FOR IDEAS EXPRESSED AS HIS WORK, AND AS SUCH ALL DRAWINGS AND SPECIFICATIONS REMAIN THE PROPERTY OF THE ARCHITECT WHETHER THE PROJECT FOR WHICH THEY ARE INTENDED IS EXECUTED OR NOT AND MAY NOT BE USED ON OTHER PROJECTS OR EXTENSIONS OF THIS PROJECT EXCEPT BY AGREEMENT WITH THE ARCHITECT.

ROBERT E. CLARK AIA ARCHITECT  
910 295 4683 FAX 910 295 5684  
65 COMMUNITY ROAD  
PINEHURST NORTH CAROLINA 28374  
P O BOX 205


NOTE:  
REFER TO SHEETS 13 & 14  
FOR TRANSVERSE SECTIONS



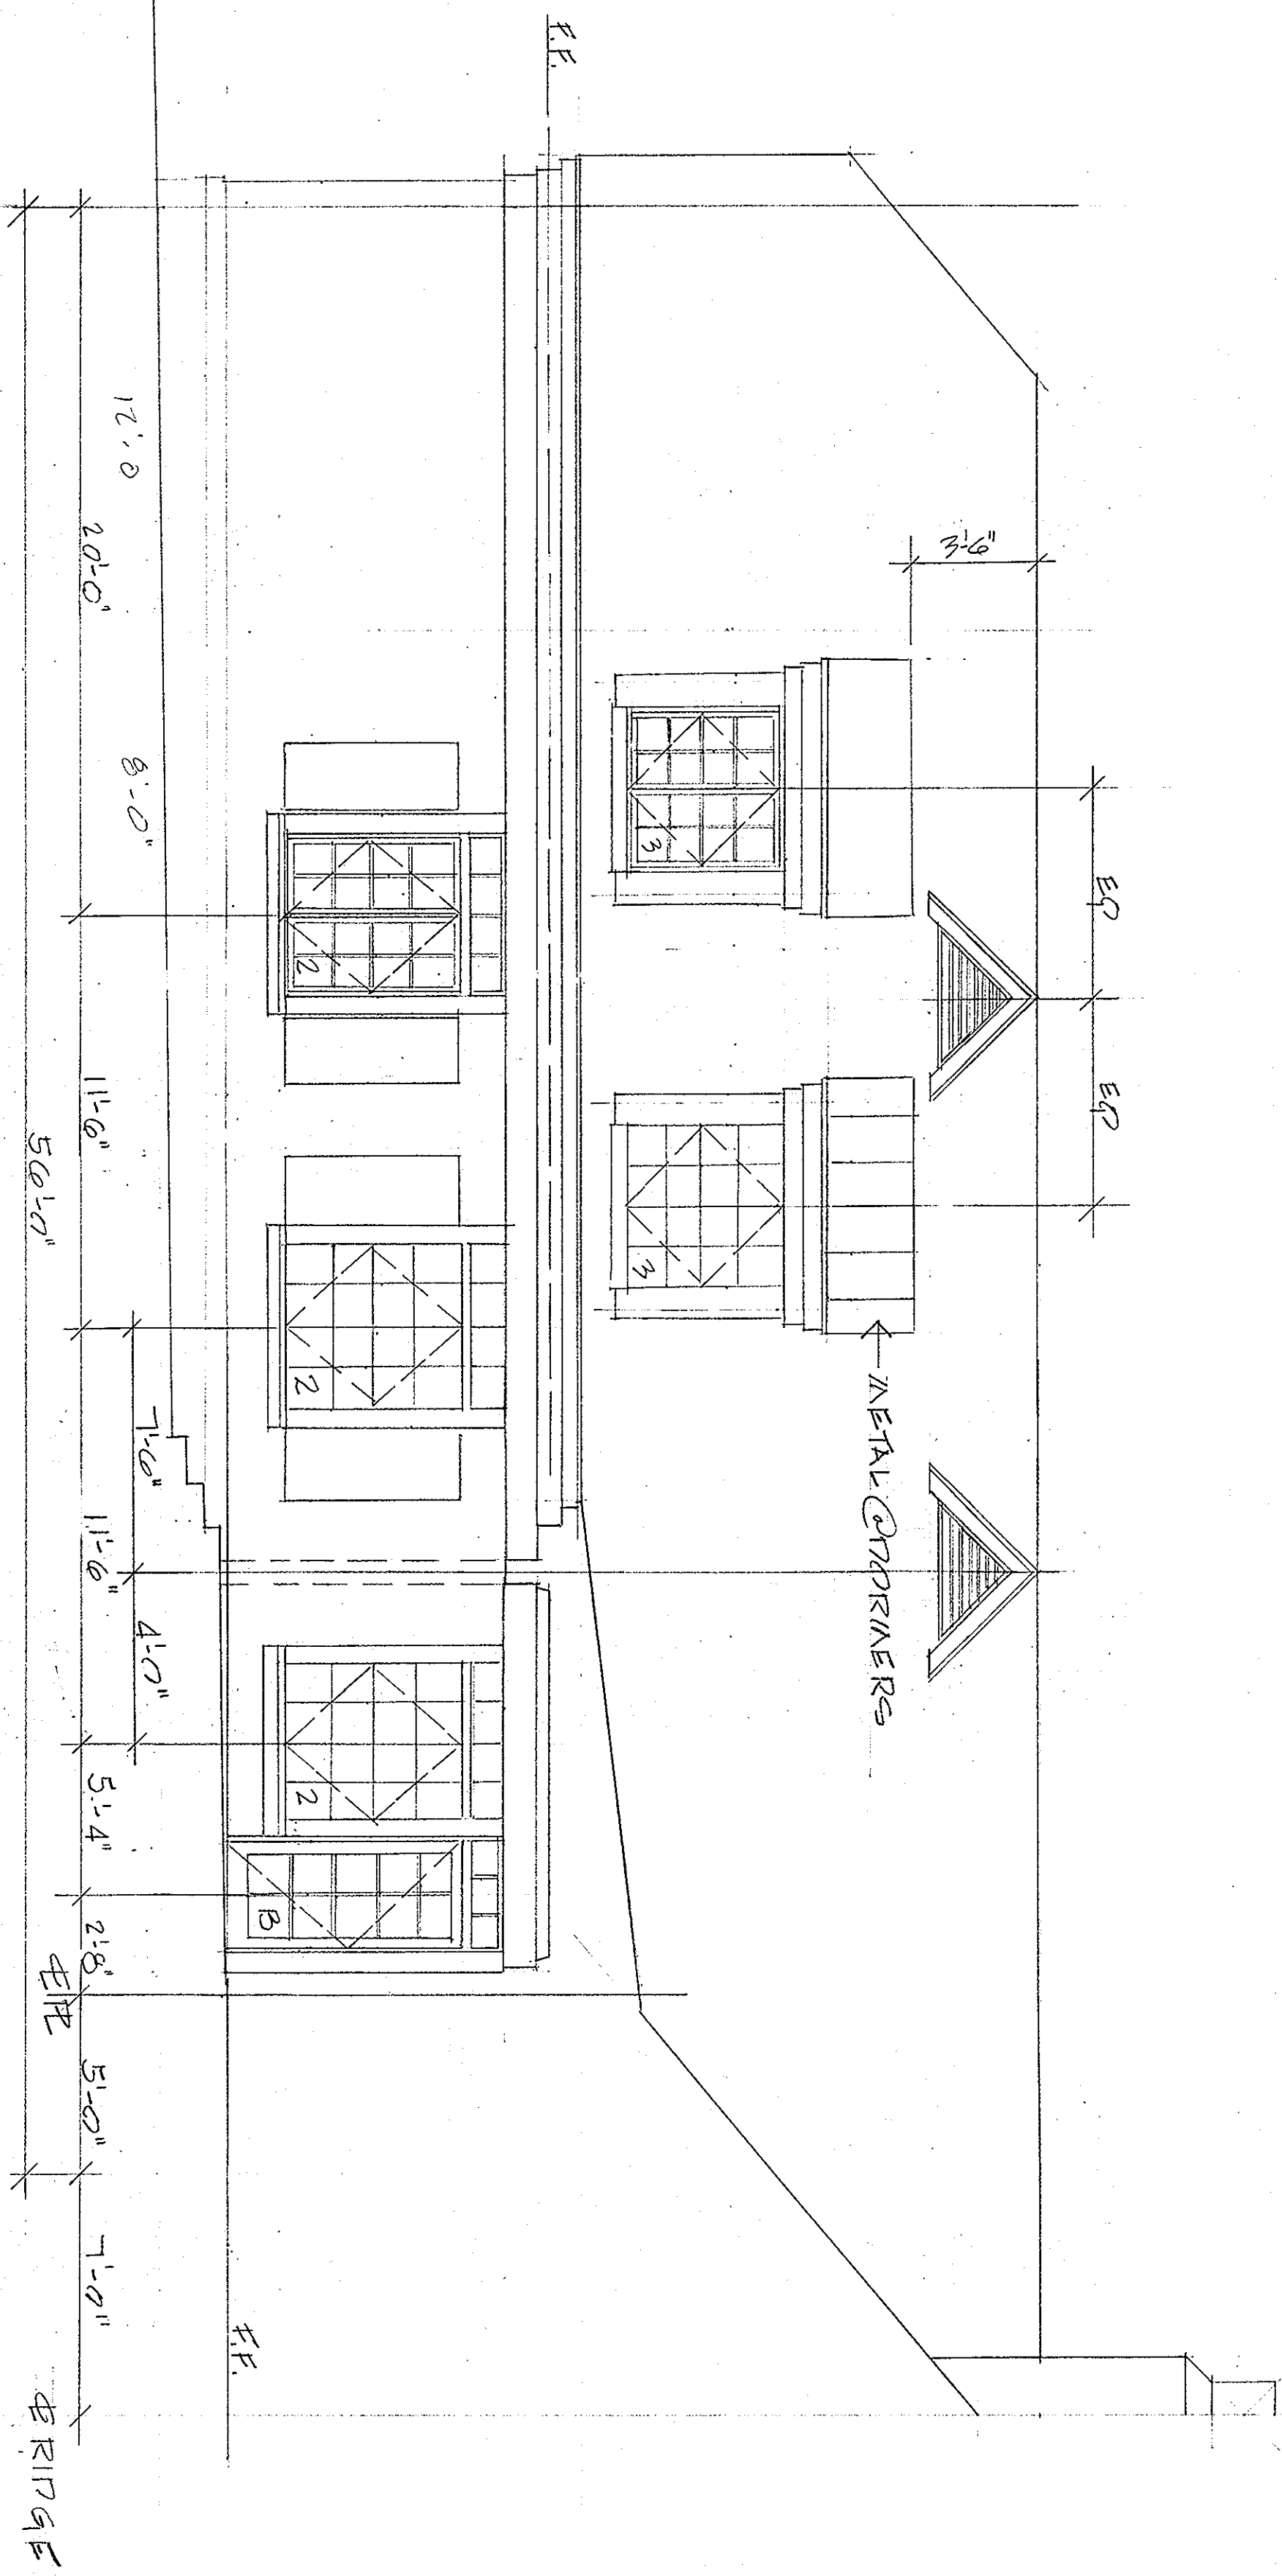


WEST ST. REFER SHEET E8

NOTE:  
NORTH ELEVATION  
IS UNCHANGED  
NUMBER PITCH HAS  
BEEN CHANGED TO  
ACCOMMODATE ATTIC  
VENT REFER SH. 13

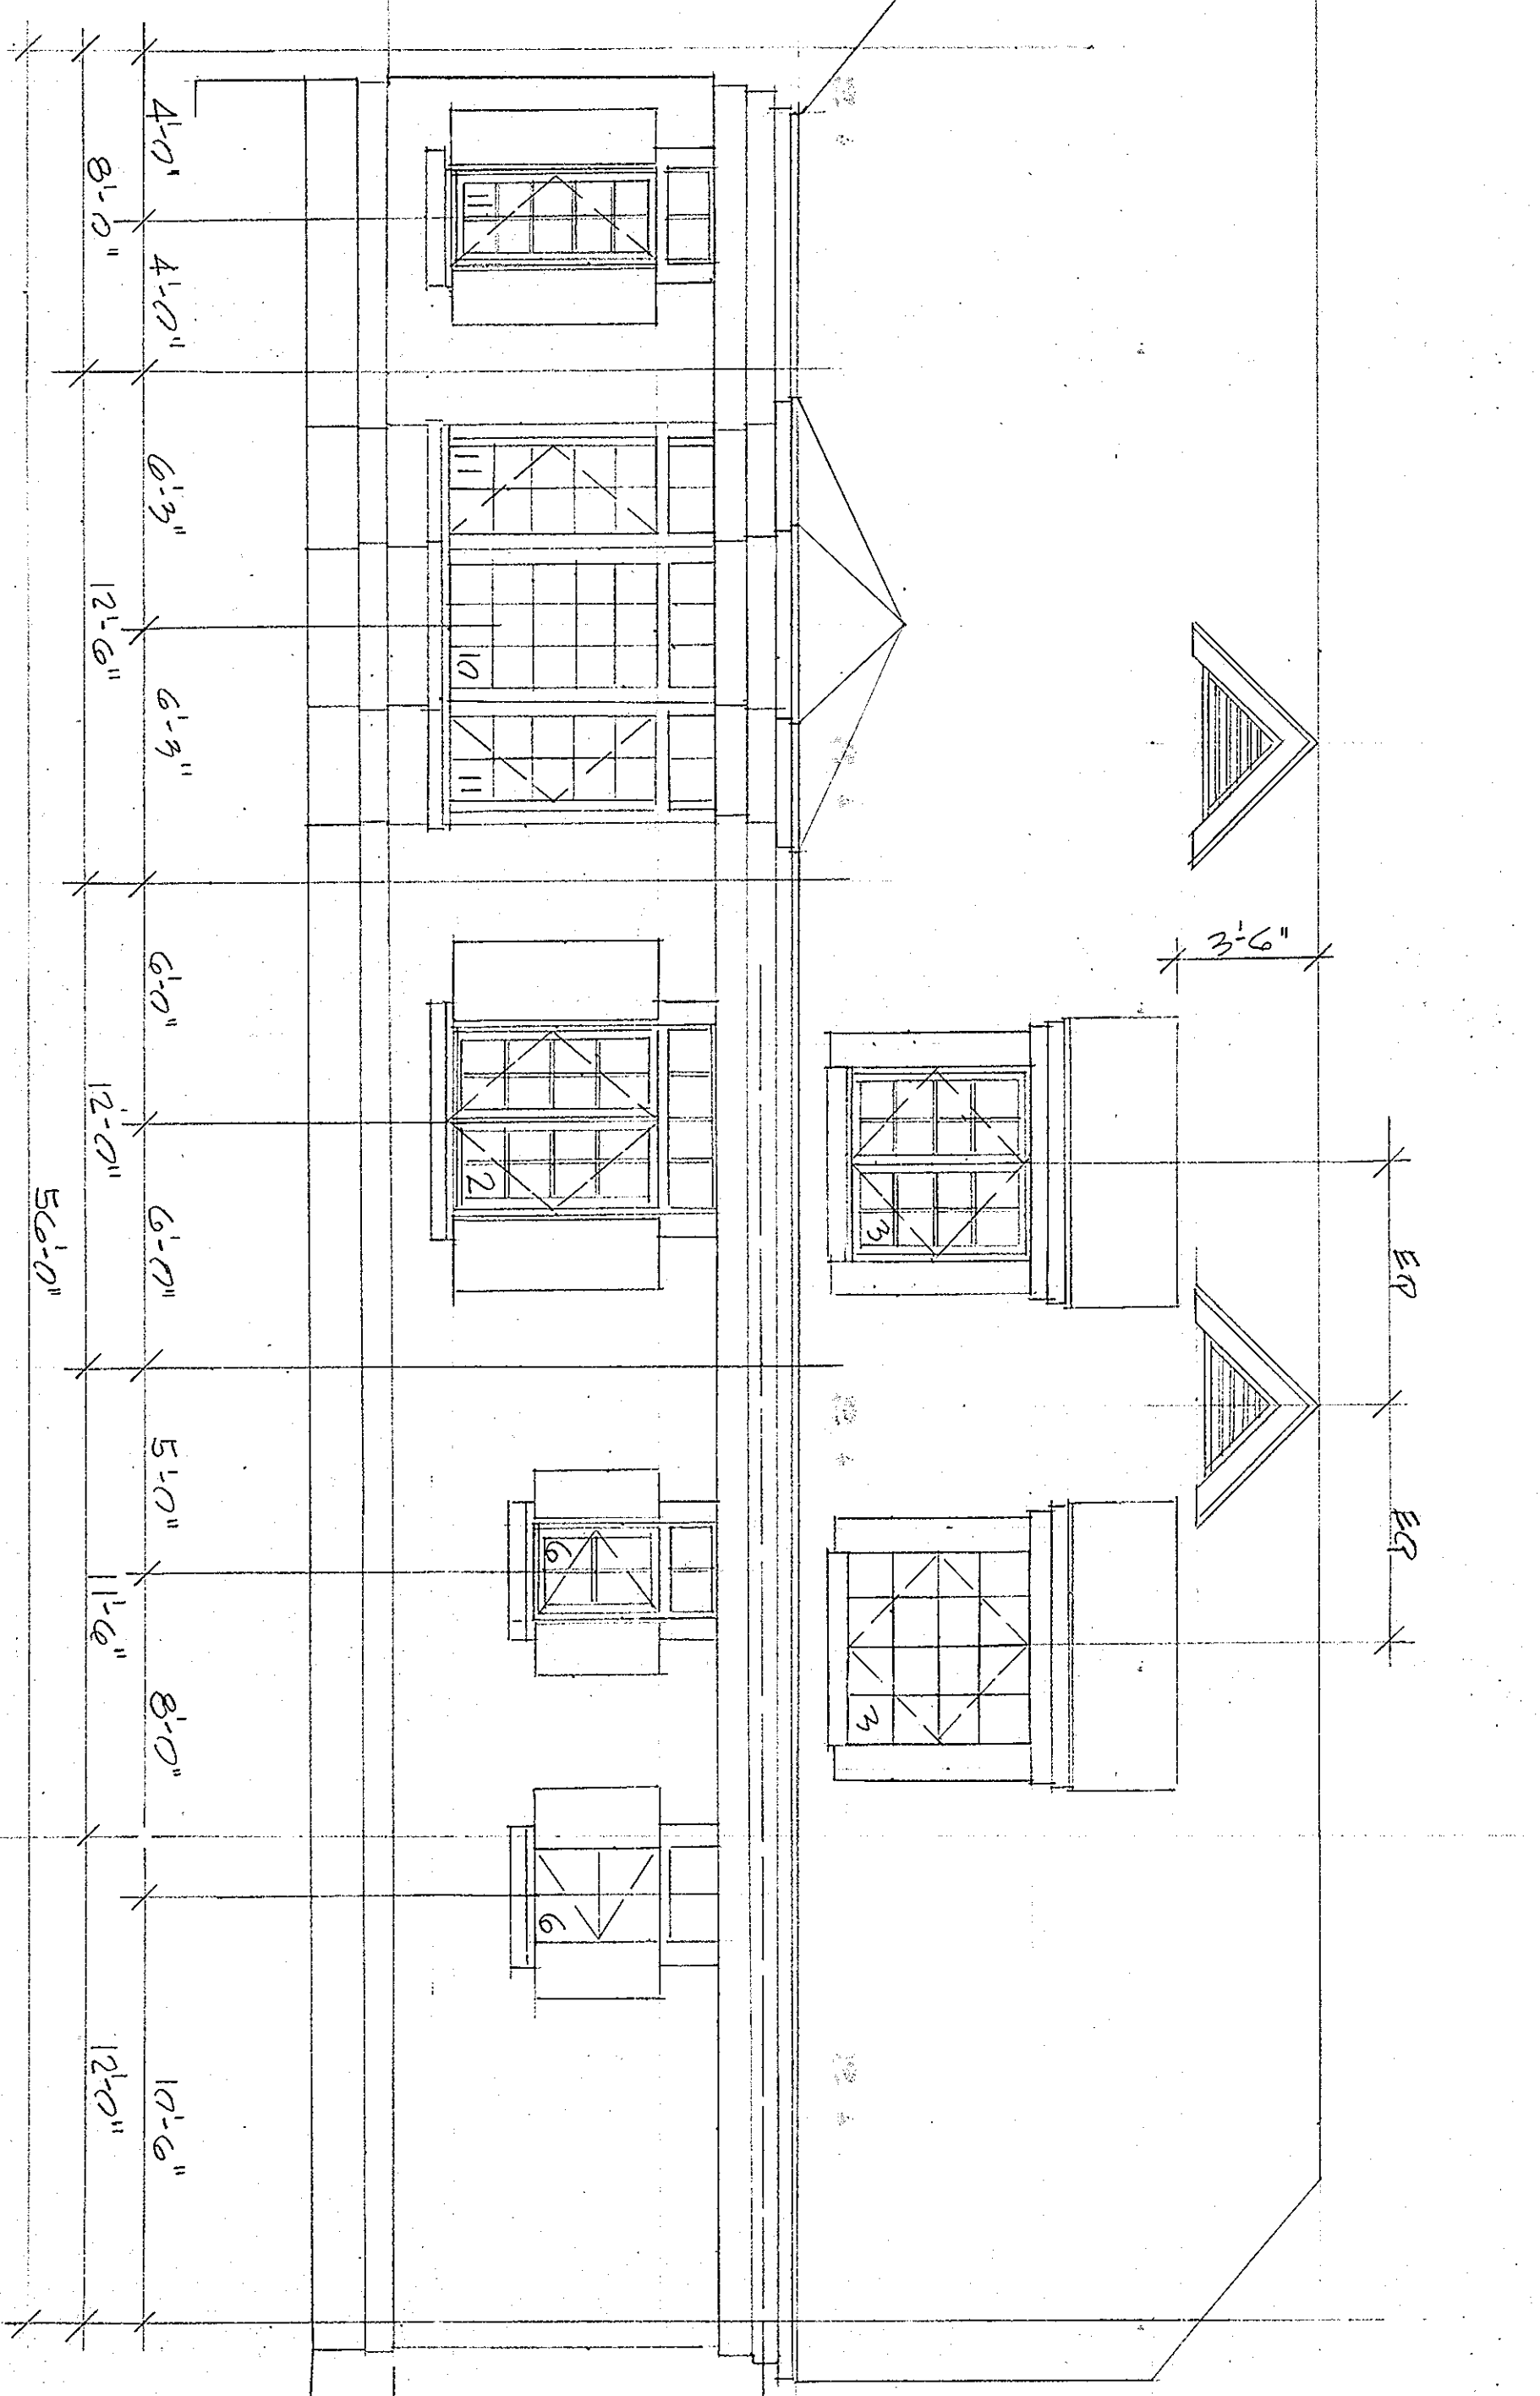


EAST ST. REFER TO SHEET E9

REVISIONS TO EXTERIOR ELEVATIONS 1/4-10"

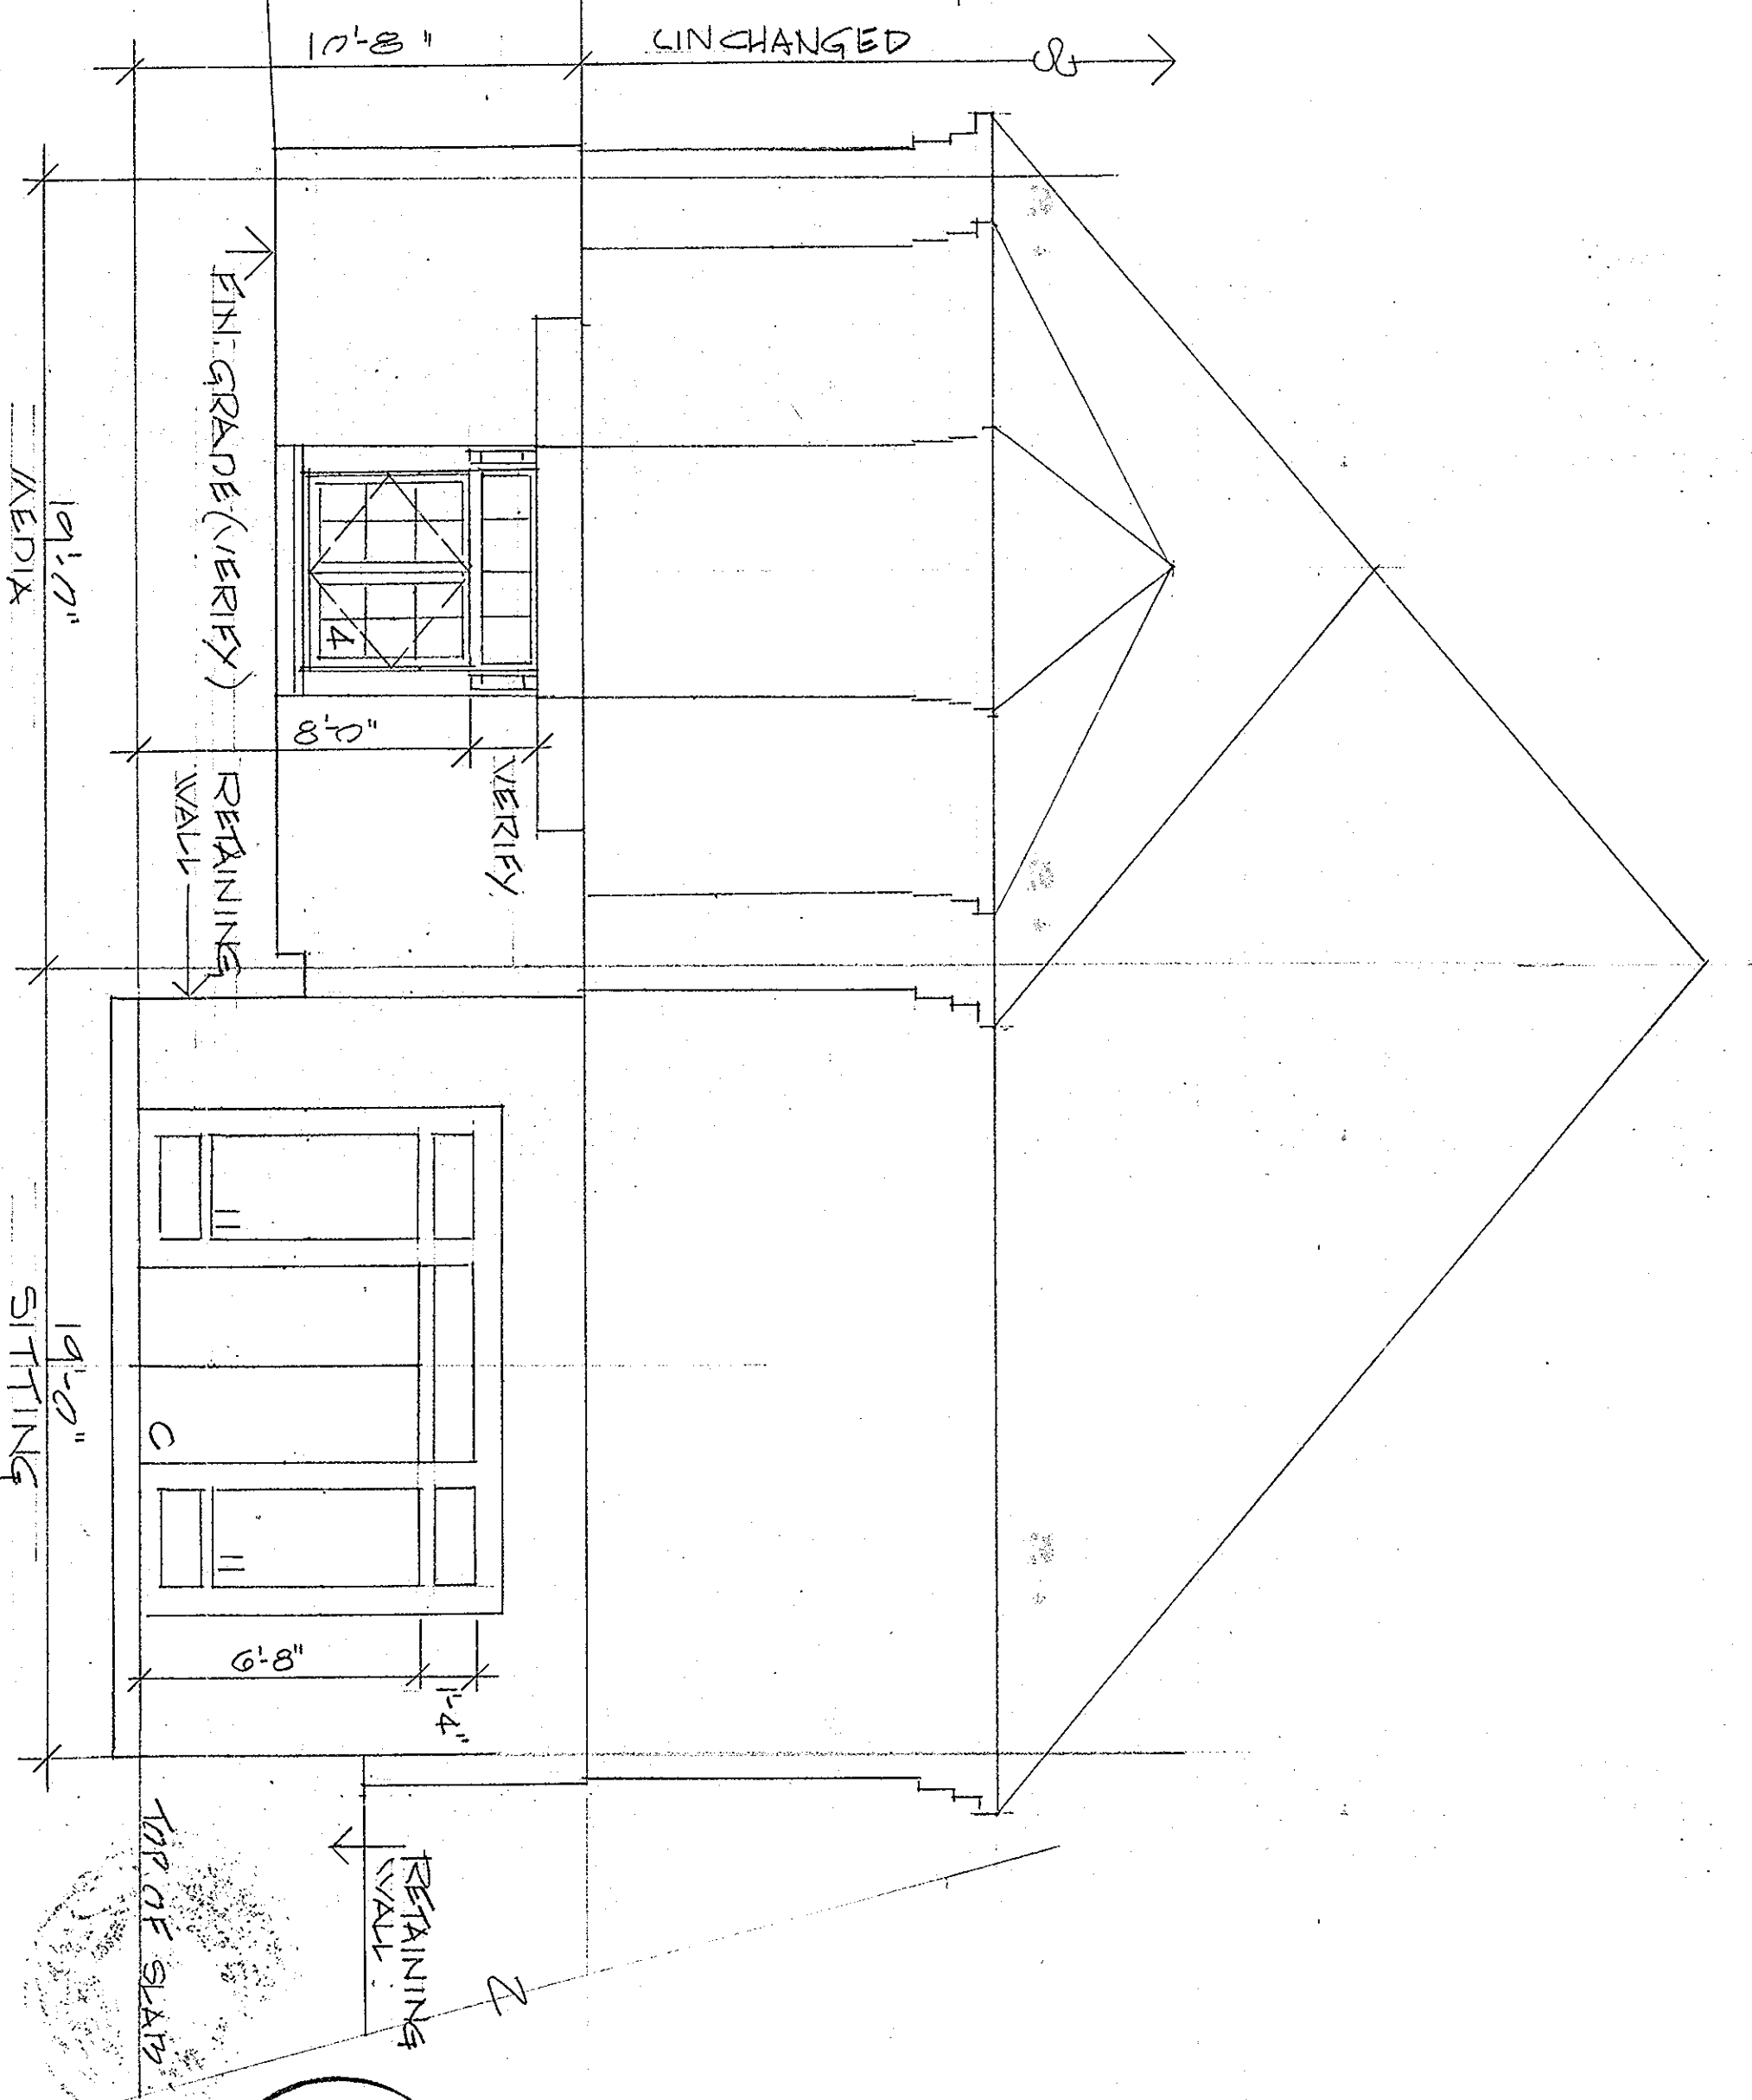

UNCHANGED

EAST: REFER TO SHEETS: S2 REVISION 1 & 12-1

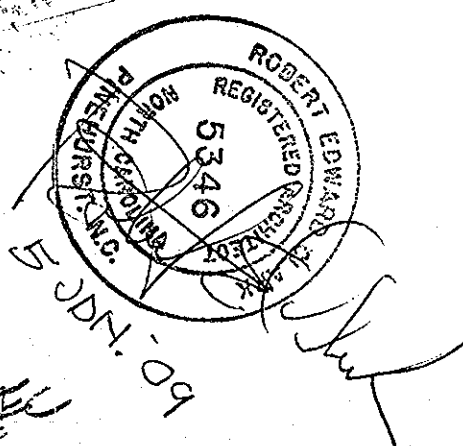


EPSTEIN/LATHAM RESIDENCE LOT 4 LINDEN TRAIL, PINEHURST, NC

THE ARCHITECT RETAINS THE RIGHT OF AUTHORSHIP FOR IDEAS EXPRESSED AS HIS WORK. AND AS SUCH ALL DRAWINGS AND SPECIFICATIONS REMAIN THE PROPERTY OF THE ARCHITECT WHETHER THE PROJECT FOR WHICH THEY ARE INTENDED IS EXECUTED OR NOT AND MAY NOT BE USED ON OTHER PROJECTS OR EXTENSIONS OF THIS PROJECT EXCEPT BY AGREEMENT WITH THE ARCHITECT.

ROBERT E. CLARK AIA ARCHITECT  
910 295 4683 FAX 910 295 5684  
65 COMMUNITY ROAD  
PINEHURST NORTH CAROLINA 28374



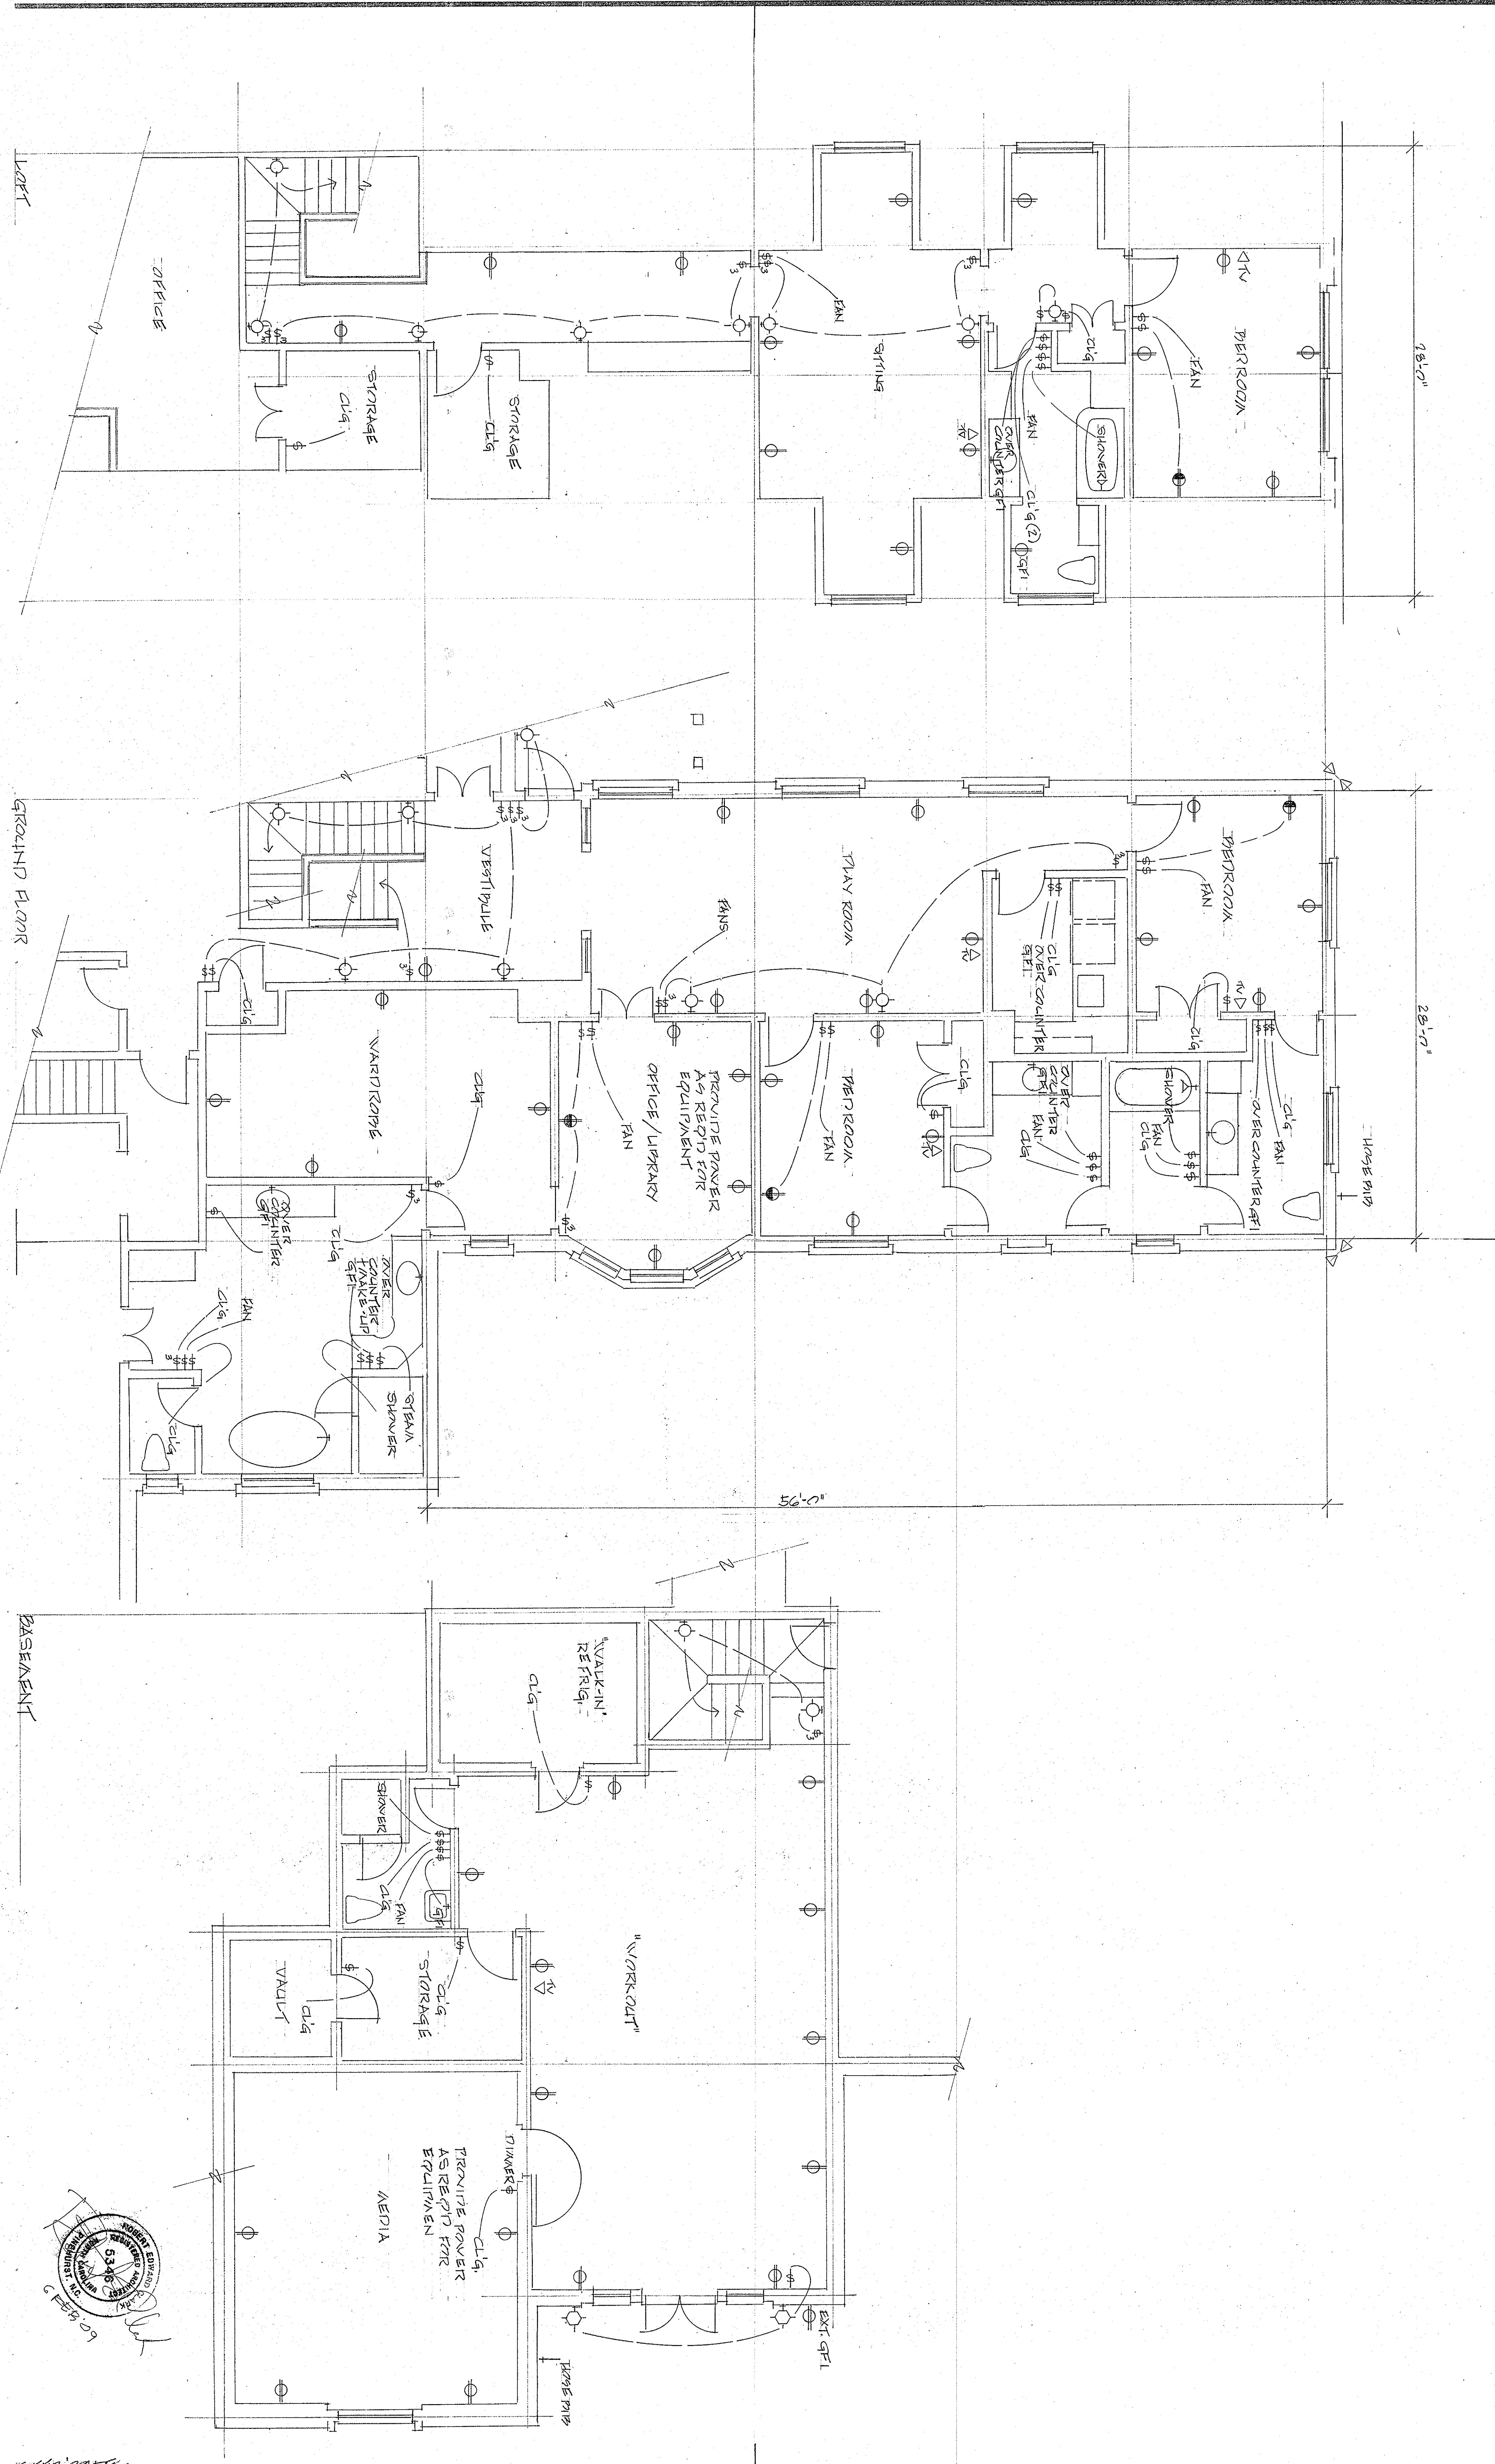

6 FEB 2002

4

EPSTEIN/LATHAM RESIDENCE

APPROVED & ACCEPTED

DATE

REVISIONS

THE ARCHITECT RETAINS THE RIGHT OF AUTHORSHIP FOR IDEAS EXPRESSED AS HIS WORK, AND AS SUCH ALL DRAWINGS AND SPECIFICATIONS REMAIN THE PROPERTY OF THE ARCHITECT WHETHER THE PROJECT FOR WHICH THEY ARE INTENDED IS EXECUTED OR NOT AND MAY NOT BE USED ON OTHER PROJECTS OR EXTENSIONS OF THIS PROJECT EXCEPT BY AGREEMENT WITH THE ARCHITECT.

ROBERT E. CLARK AIA ARCHITECT

910 295 4683

66 COMMUNITY ROAD  
PINEHURST NORTH CAROLINA 28374

FAX 910 295 5684

P O BOX 205



EPSTEIN/LATHAM


APPROVED & ACCEPTED DATE

REVISIONS

THE ARCHITECT RETAINS THE RIGHT OF AUTHORSHIP FOR IDEAS EXPRESSED AS HIS WORK, AND AS SUCH ALL DRAWINGS AND SPECIFICATIONS REMAIN THE PROPERTY OF THE ARCHITECT. WHETHER THE PROJECT FOR WHICH THEY ARE INTENDED IS EXECUTED OR NOT AND MAY NOT BE USED ON OTHER PROJECTS OR EXTENSIONS OF THIS PROJECT EXCEPT BY AGREEMENT WITH THE ARCHITECT.




ROBERT E. CLARK AIA ARCHITECT  
66 COMMUNITY ROAD  
PINEHURST NORTH CAROLINA 28374

910 295 4683  
910 295 5684  
P O BOX 205

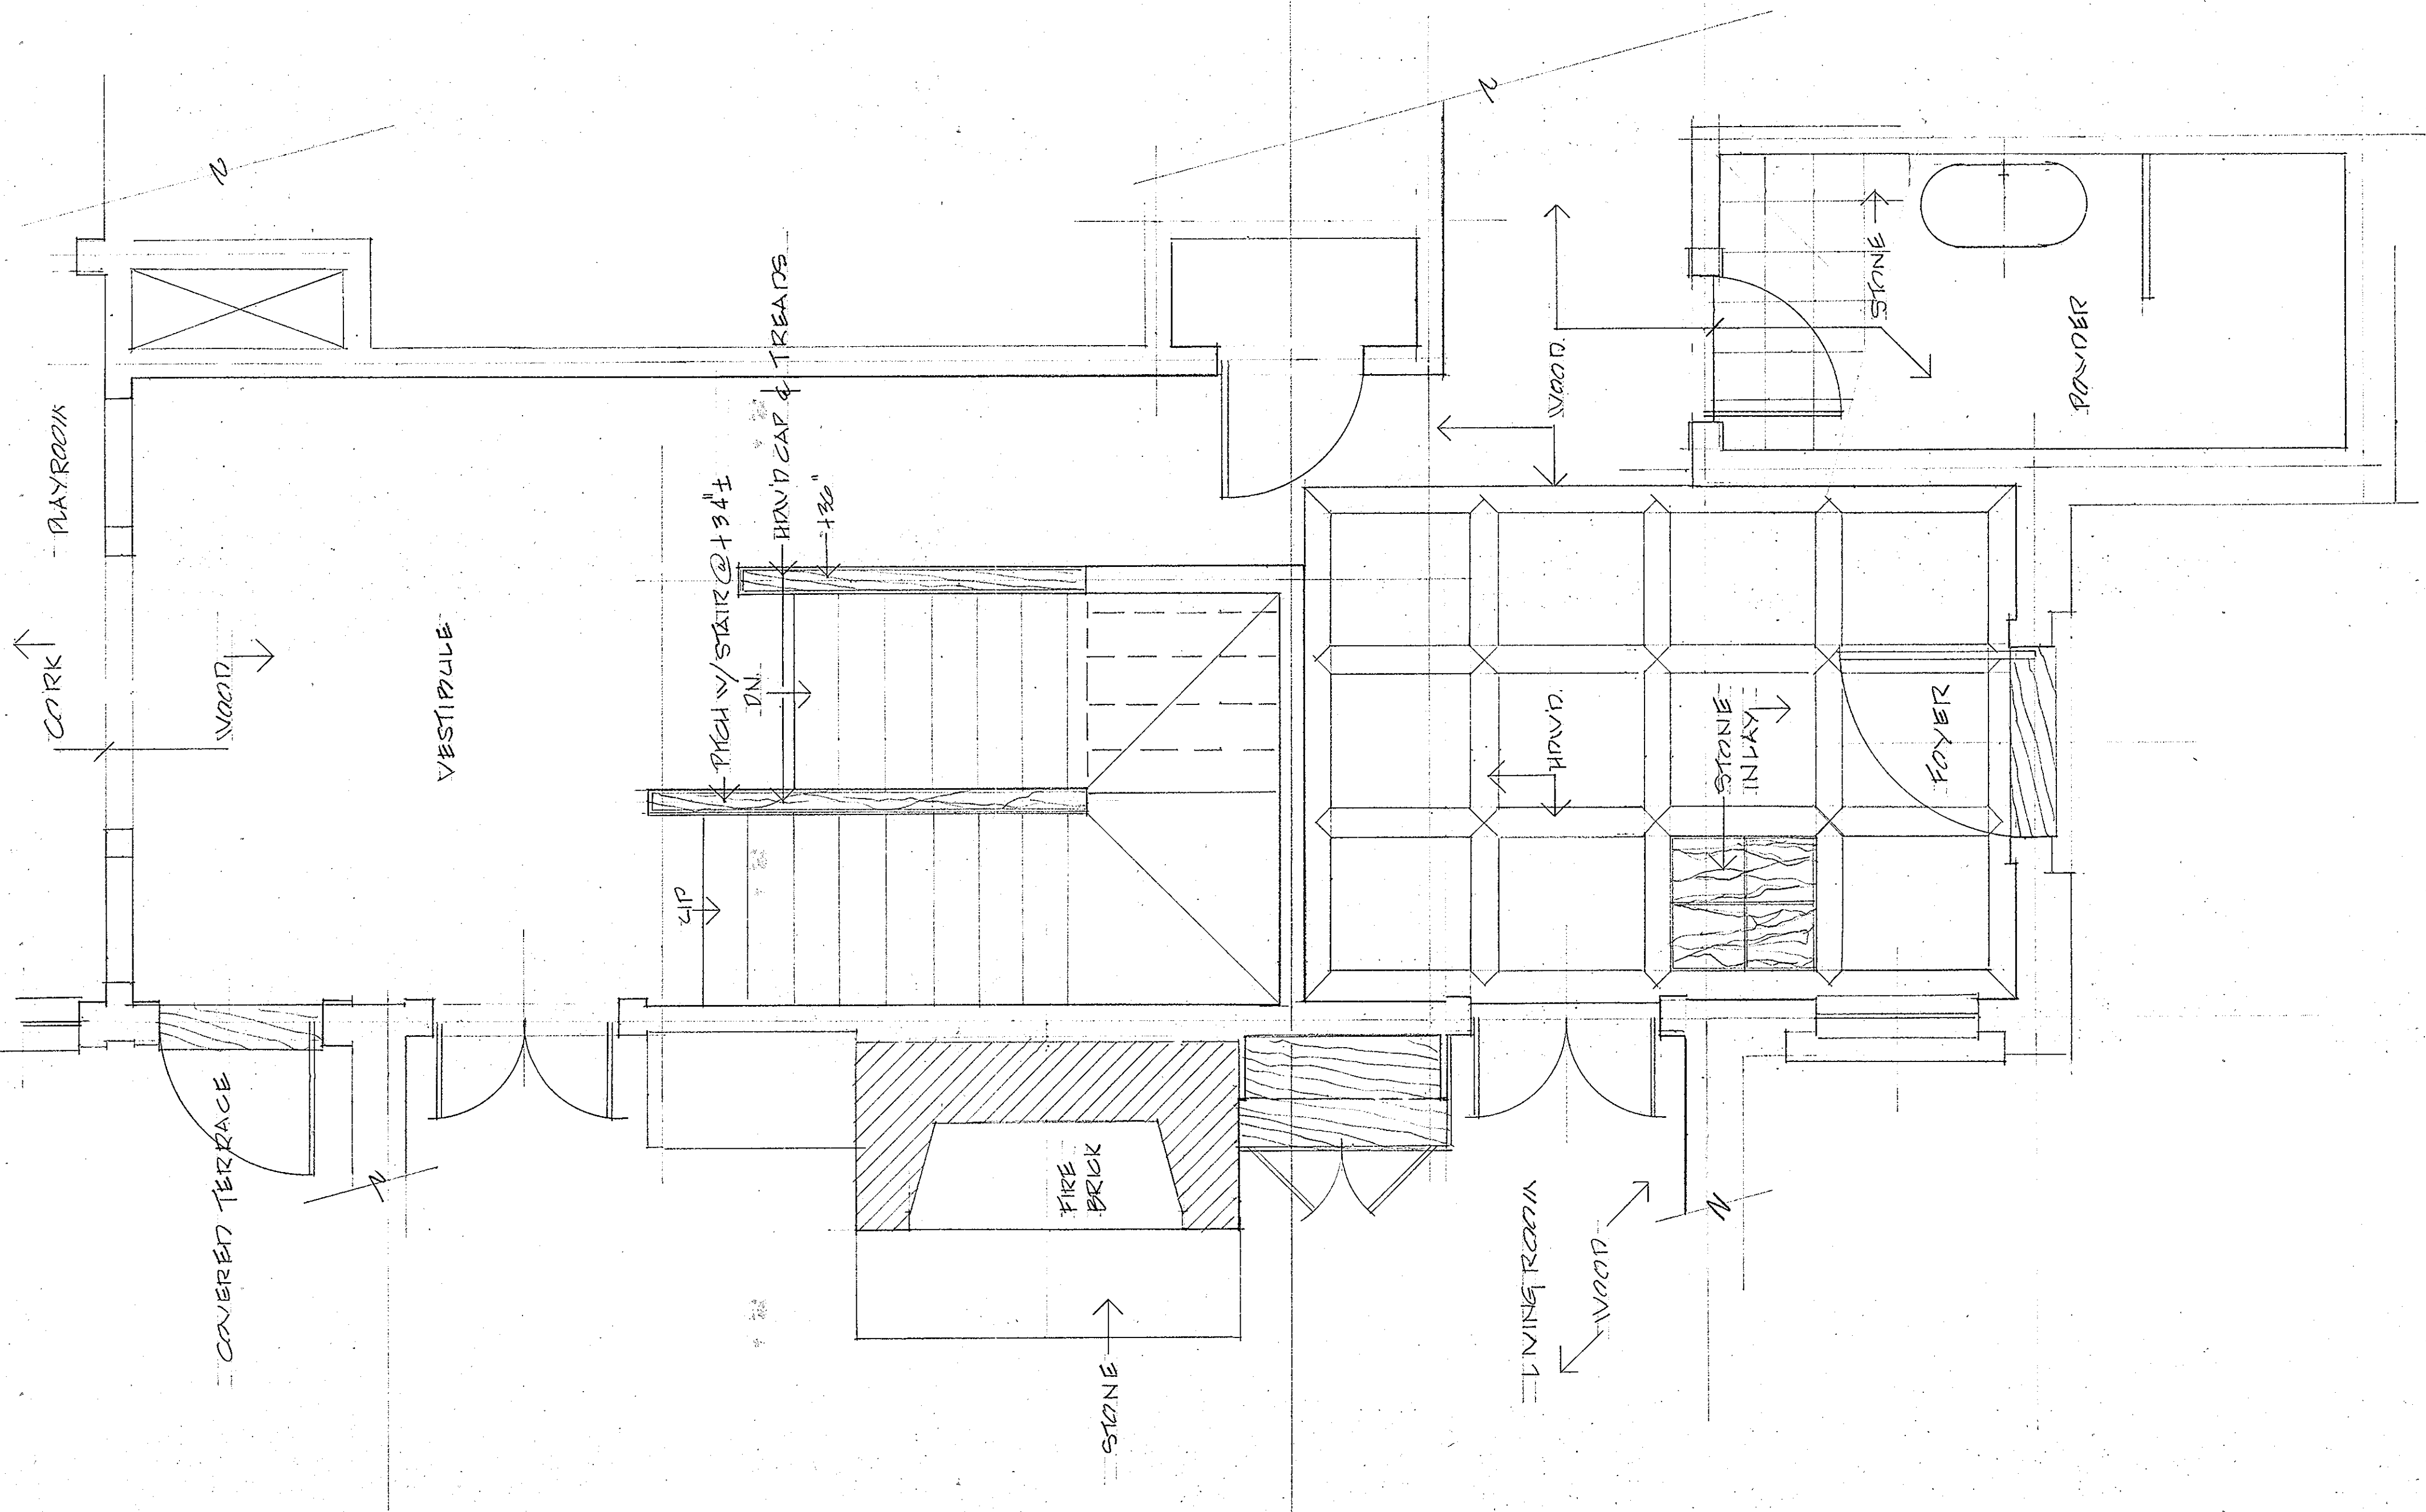



EPSTEIN/LATHAM RESIDENCE LOT 4 LINDEN TRAIL PINEHURST, NC

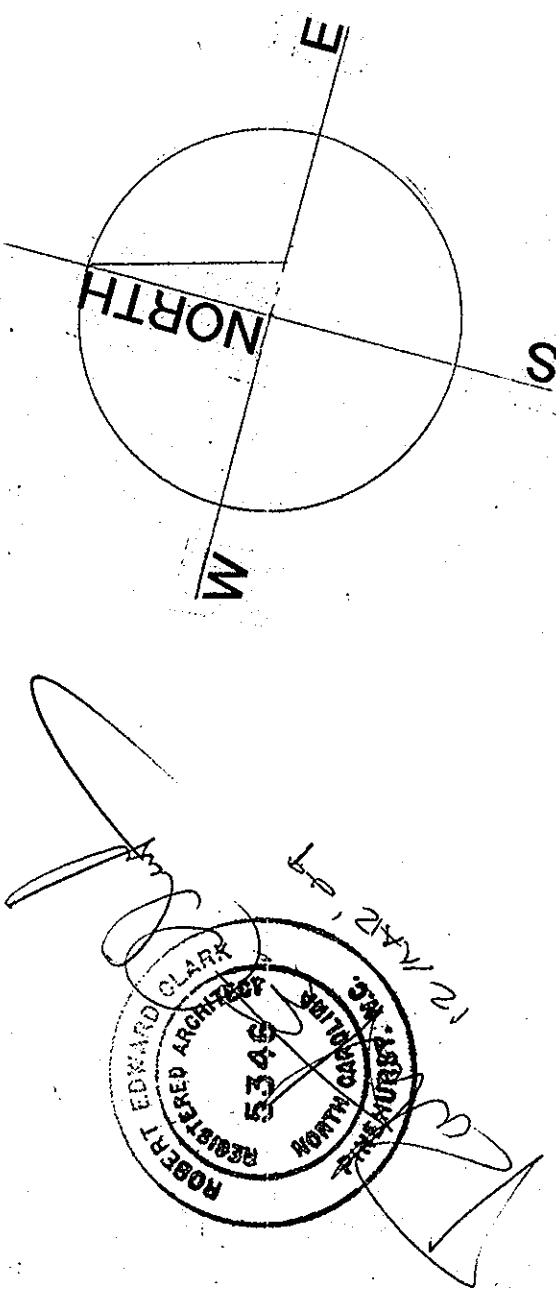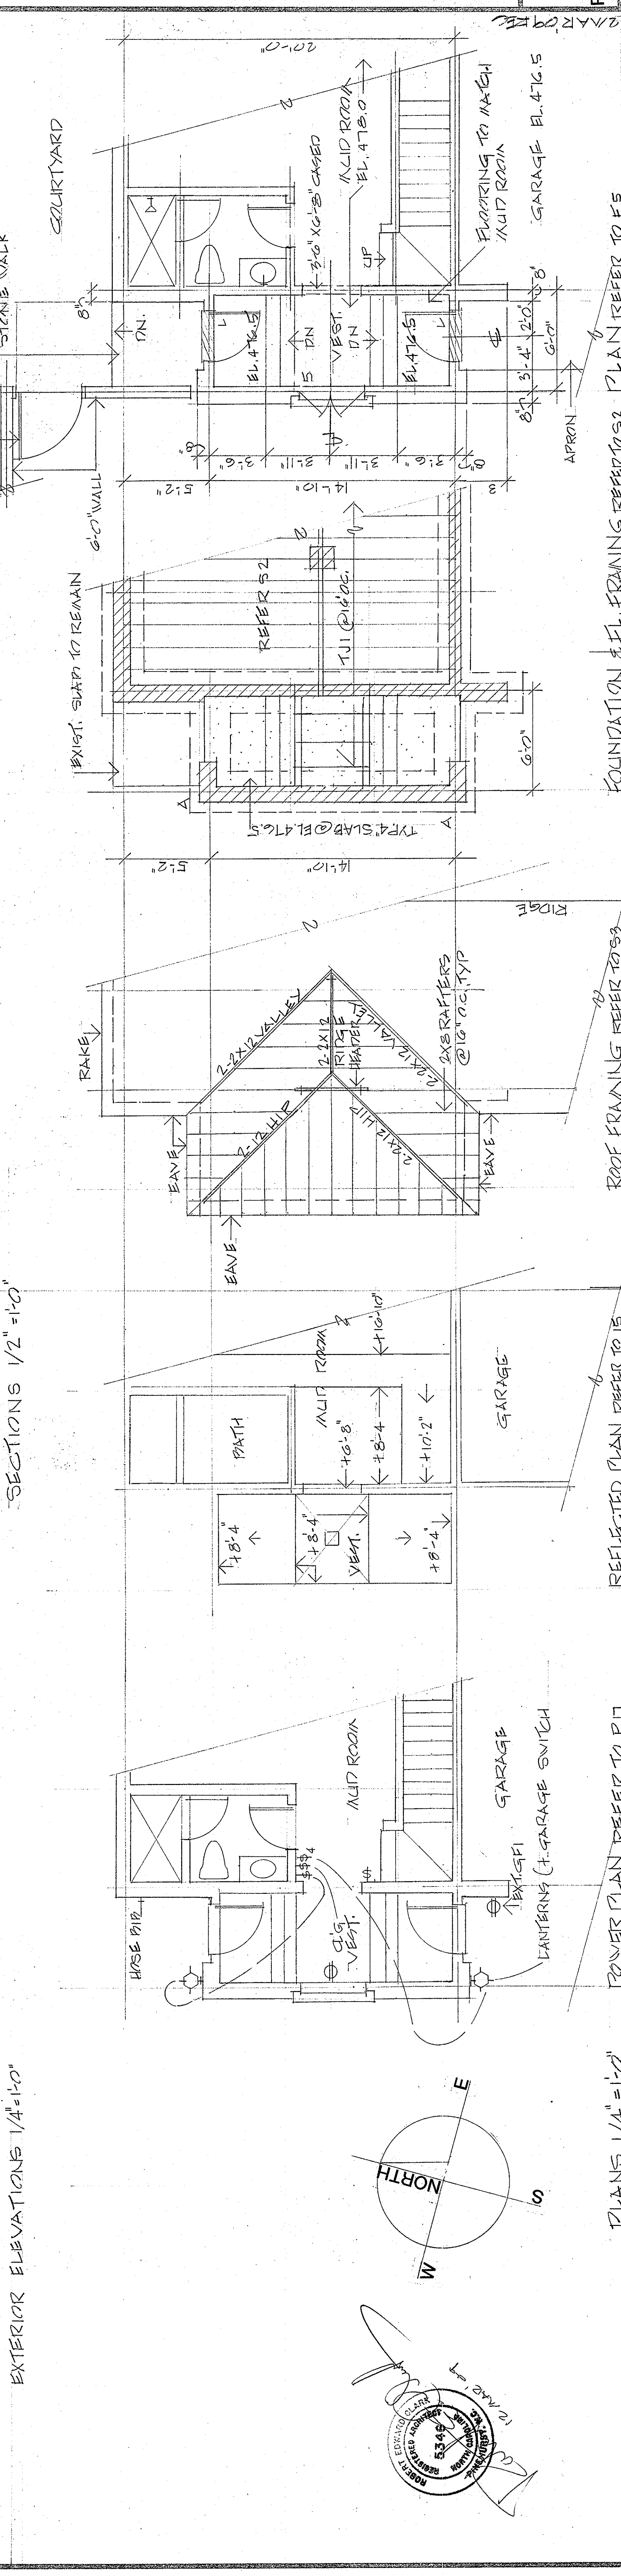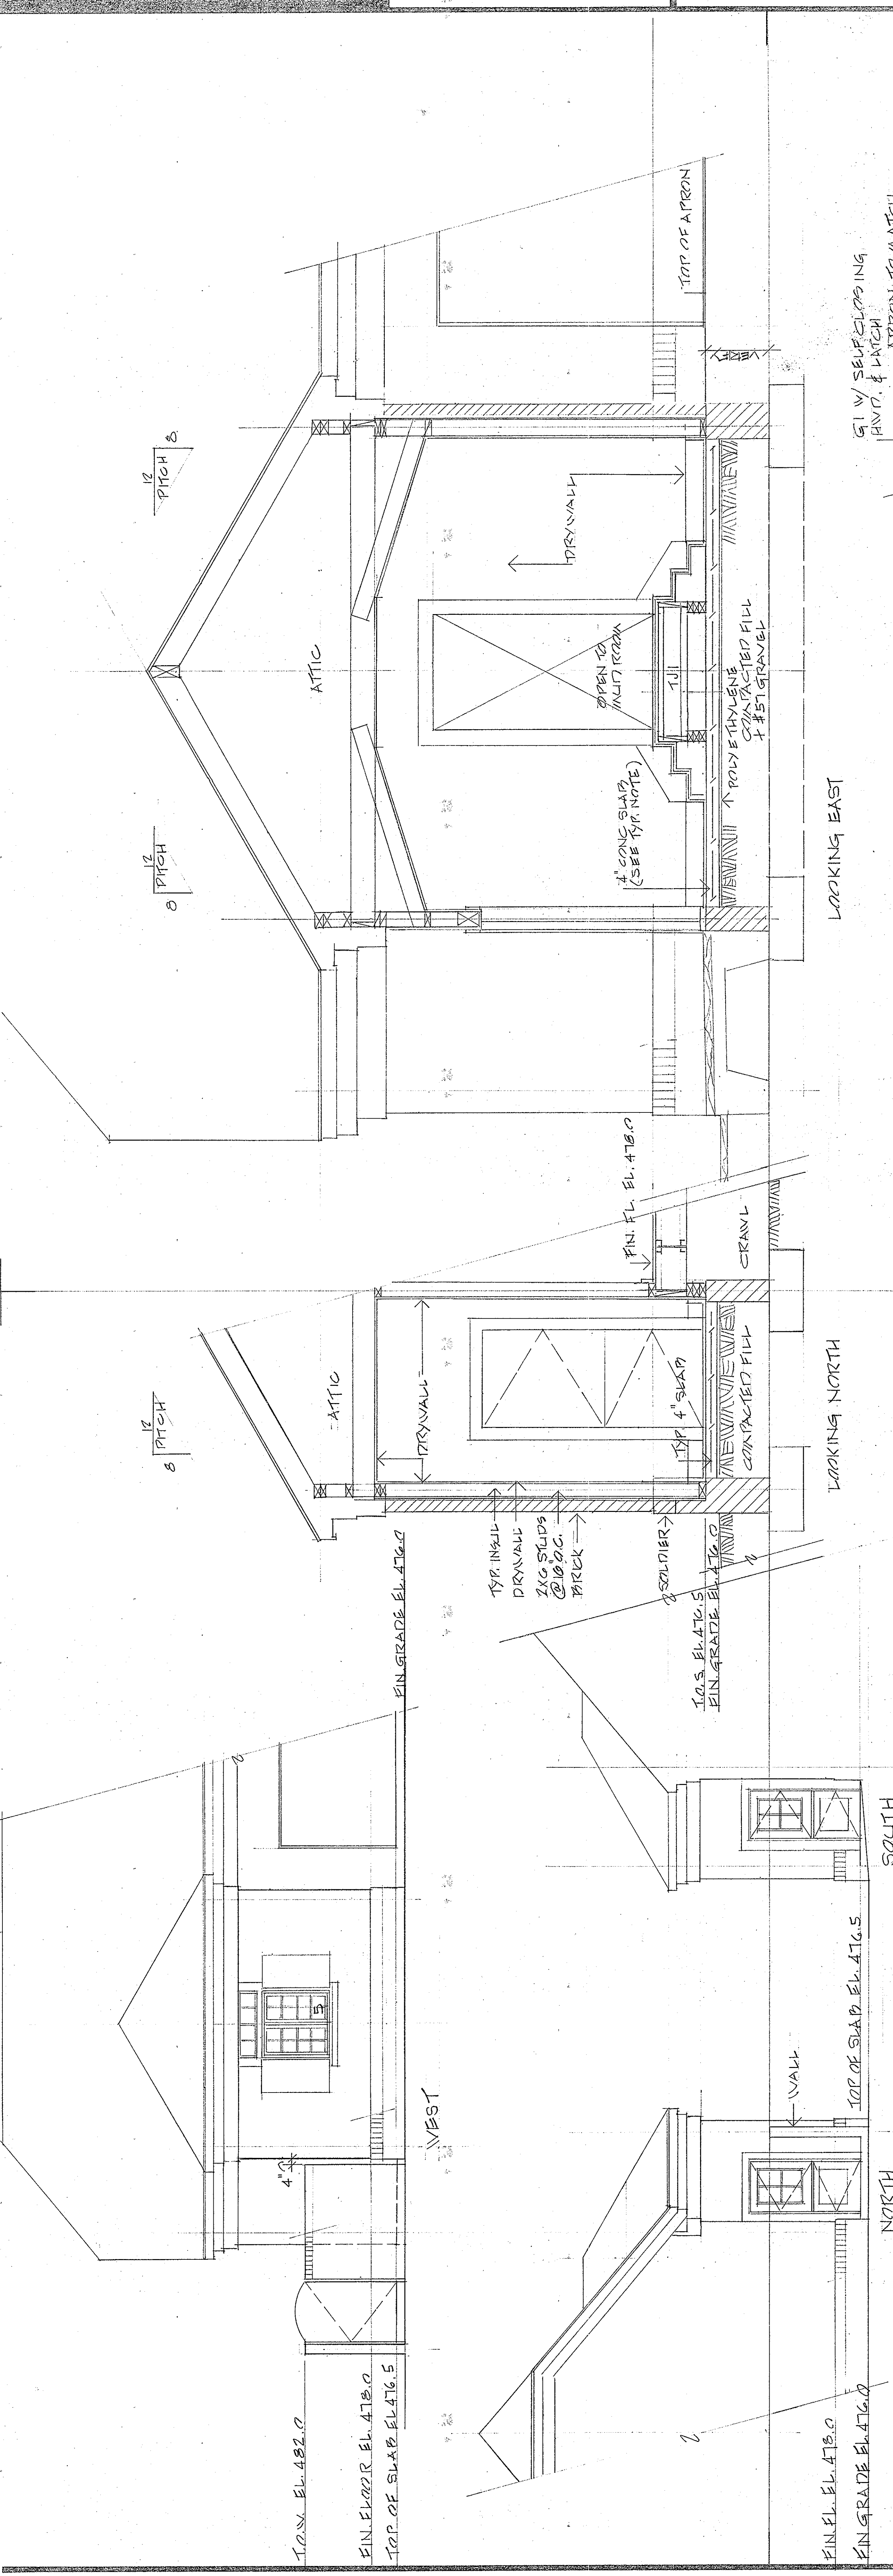



EPSTEIN/LATHAM

APPROVED & ACCEPTED

DATE

REVISIONS

THE ARCHITECT RETAINS THE RIGHT OF AUTHORSHIP FOR  
DRAWINGS AND SPECIFICATIONS REMAIN THE PROPERTY  
OF THE ARCHITECT WHETHER THE PROJECT FOR WHICH  
THEY ARE INTENDED IS EXECUTED OR NOT AND MAY NOT  
BE USED ON OTHER PROJECTS OR EXTENSIONS OF THIS  
PROJECT EXCEPT BY AGREEMENT WITH THE ARCHITECT.

IDEAS EXPRESSED AS HIS WORK AND AS SUCH ALL

ROBERT E. CLARK AIA ARCHITECT

910 295 4683

FAX

910 295 5684

P O BOX 205

66 COMMUNITY ROAD  
PINEHURST NORTH CAROLINA 28374

